



ARCHITECTURAL DETAIL DRAWINGS- GROUND FLOOR


TENDER DRAWINGS

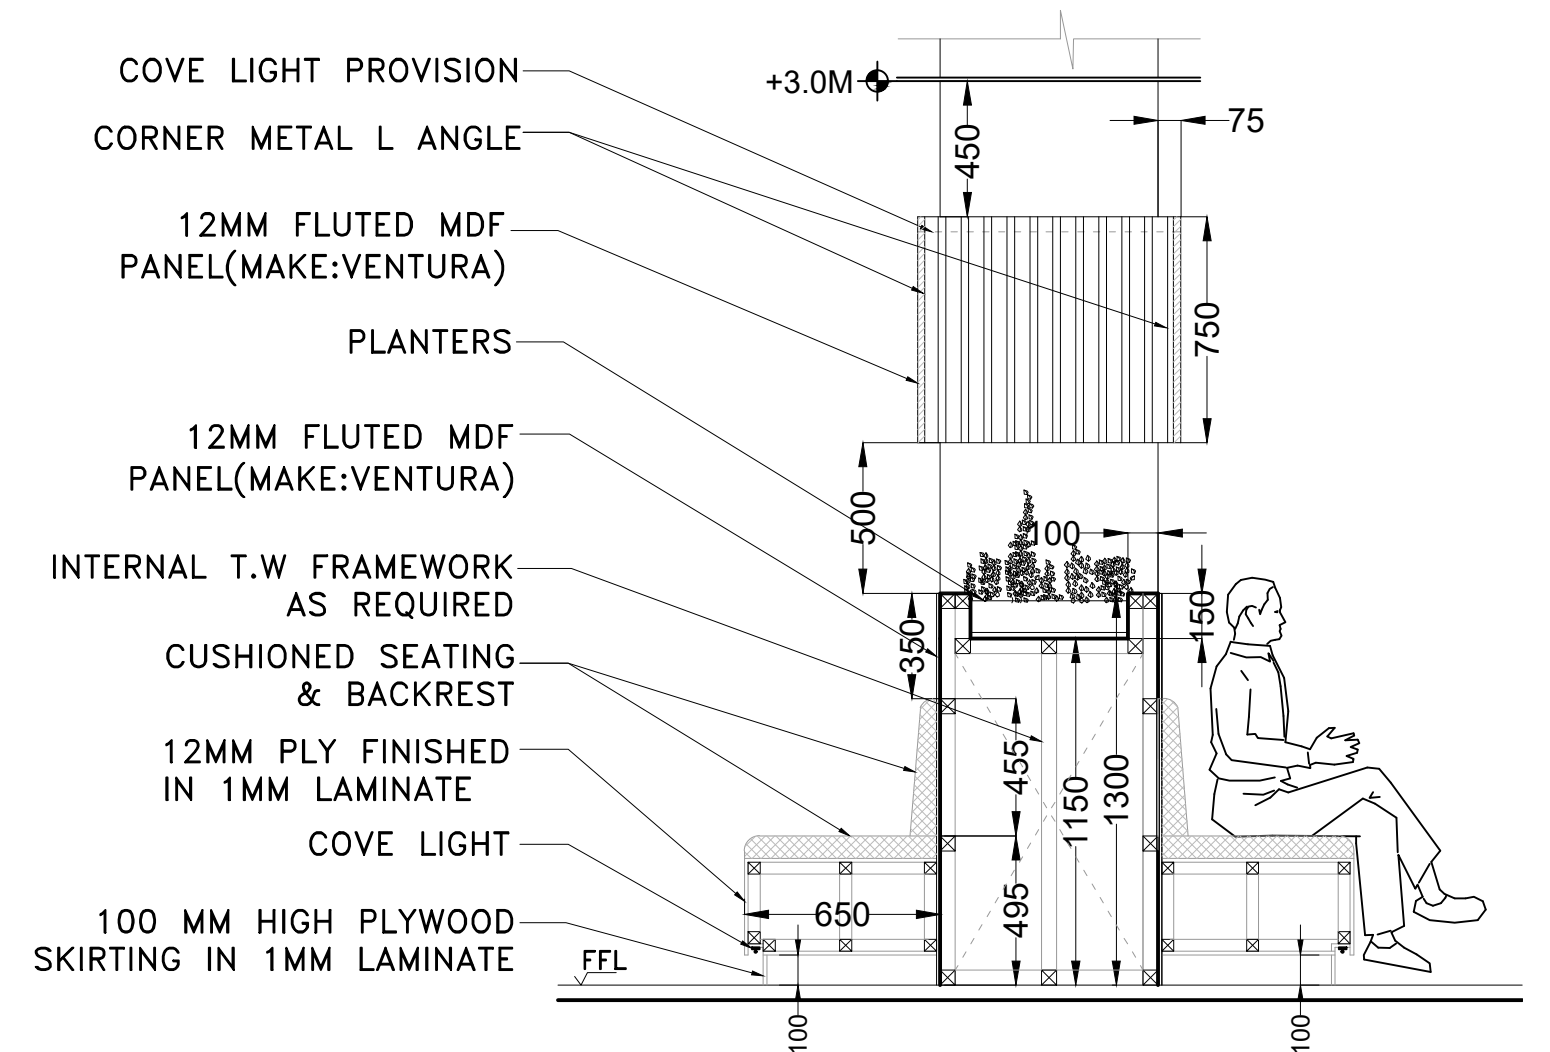


SECTION AA' C
SCALE= 1:25

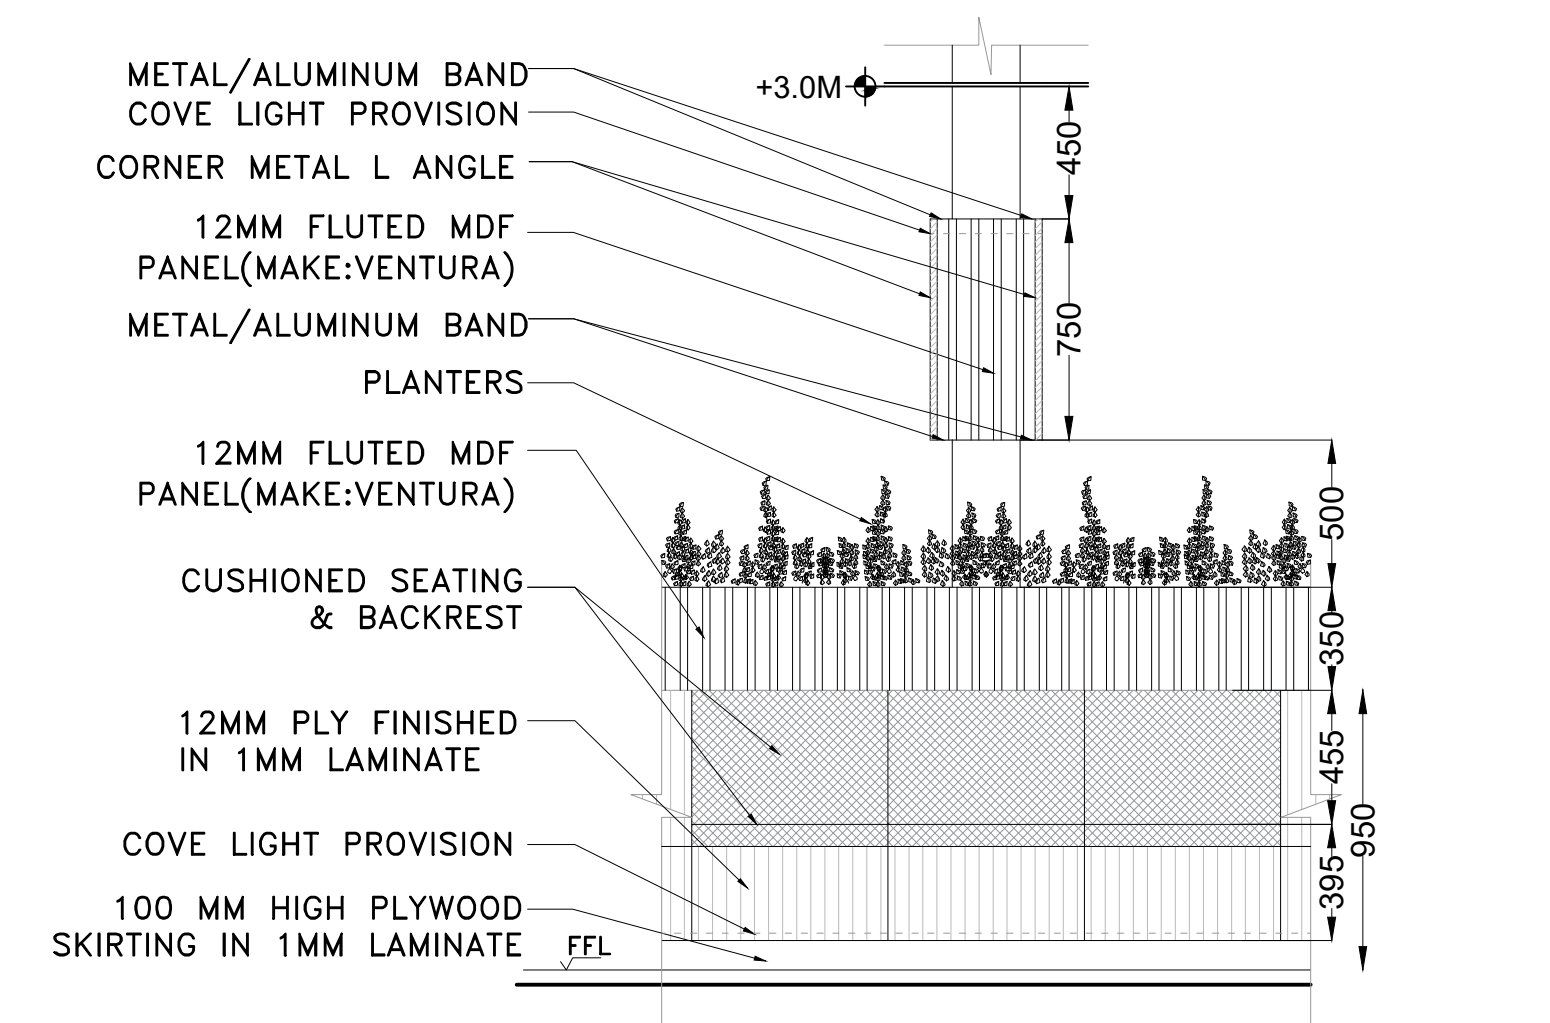

PART FRONT ELEVATION
SCALE= 1:25

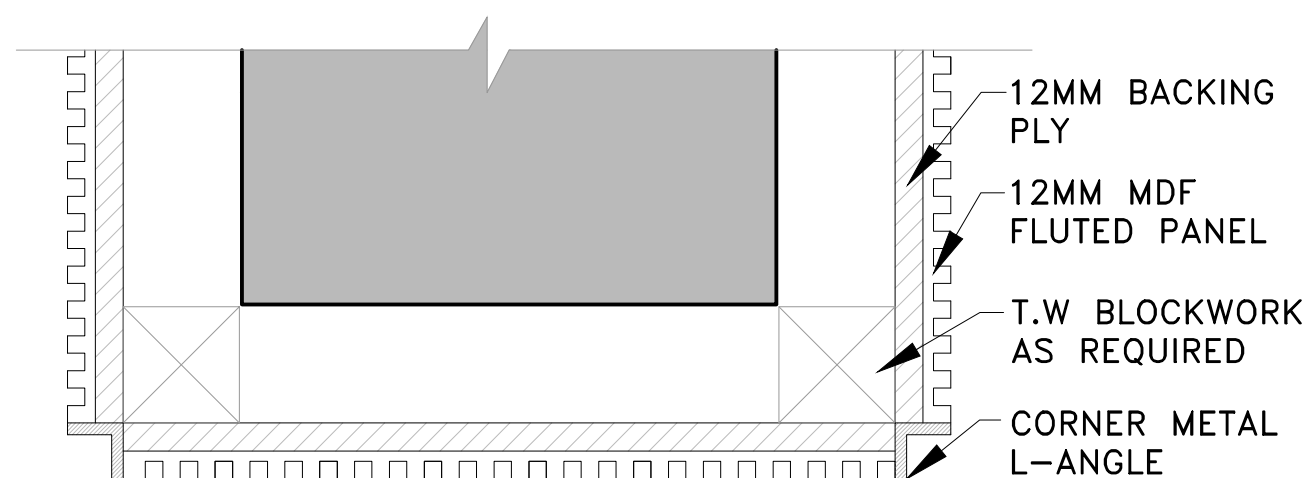


REFERENCE IMAGE 

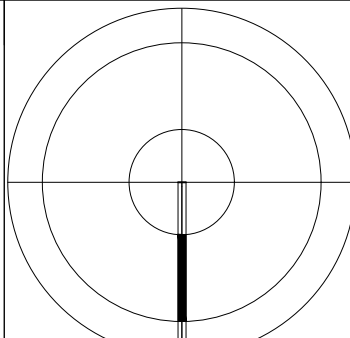
	2	02.08.22	TENDER DRAWING	
	No.	DATE	ISSUE/ REVISION	
	I I T BOMBAY: VANVIHAR GUEST HOUSE POWAI, MUMBAI - 400 076, INDIA			
	UPENDRA NAYAK & ASSOCIATES ARCHITECTS. INTERIOR DESIGNERS 1, SULBHA NIWAS. DILIP GUPTA MARG. MAHIM, MUMBAI 400016 TEL: 24458473 FAX:24446223			
	DATE:21.02.2022	SCALE:AS NOTED	DRAWN BY:HR	CHECKED BY:AB
				



REFERENCE IMAGE C

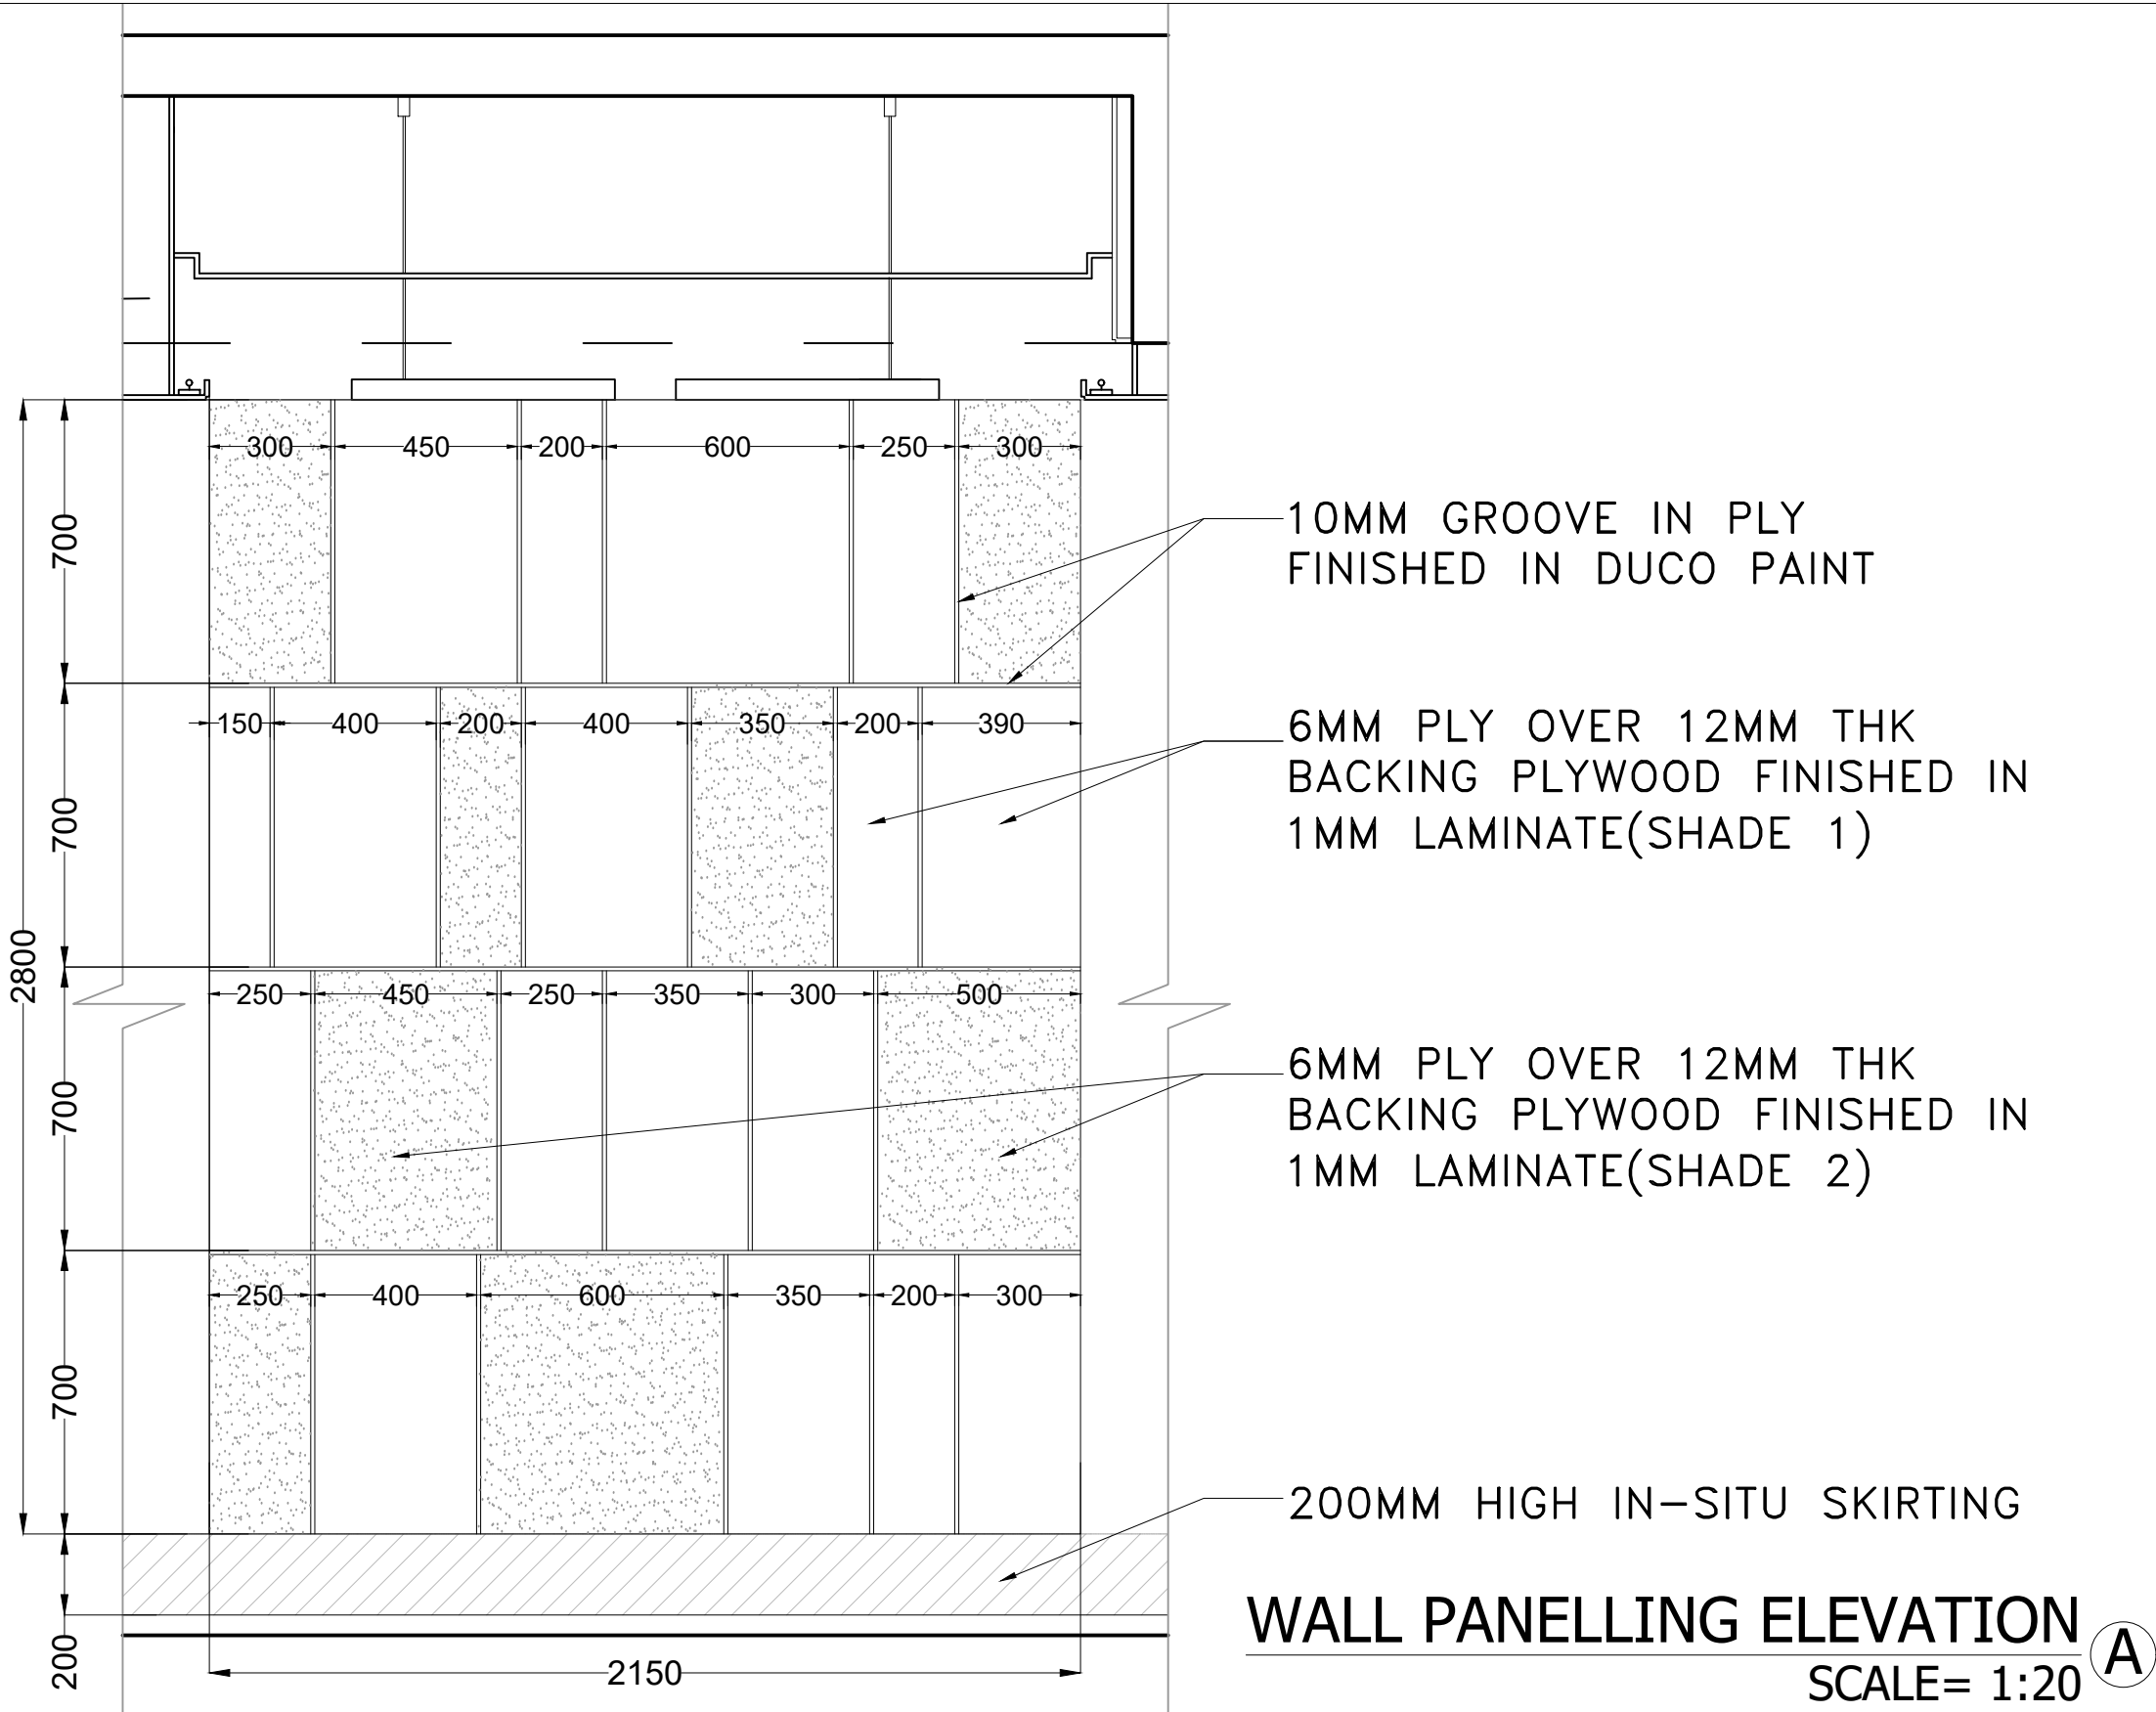

WALL PANELLING ELEVATION A
SCALE= 1:20

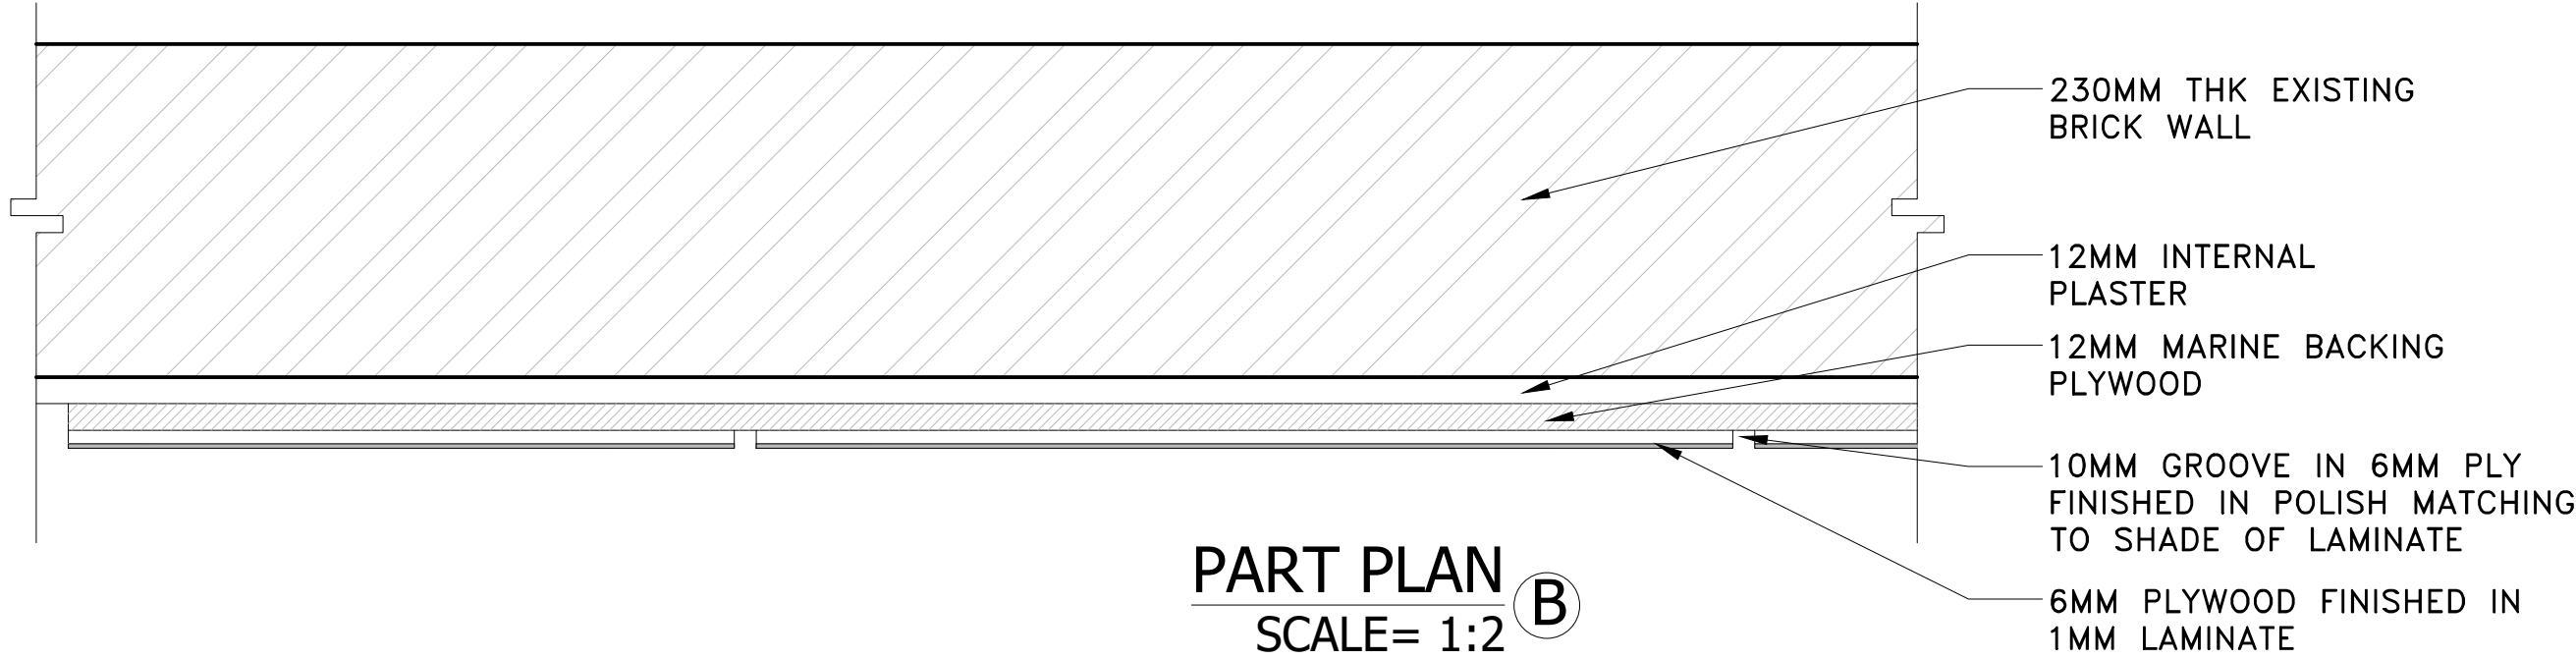






PART PLAN B
SCALE= 1:2

MULTIPURPOSE AREA WALL PANELLING DETAIL - 03

NOTES:

1. DRAWINGS SHALL NOT BE SCALED.
2. ALL DIMENSIONS ARE IN MM.
3. ANY DISCREPANCY IN DRAWINGS AND EXISTING CONDITIONS SHOULD BE BROUGHT TO THE NOTICE OF THE ARCHITECT PRIOR TO PROCEEDING WITH THE ITEM
4. FOR SIZE OF STRUCTURAL MEMBERS REFER STRUCTURAL ENGINEER'S DRAWINGS.
5. ALL DOOR & WINDOW DIMENSIONS LISTED IN SCHEDULES MUST BE VERIFIED WITH SITE CONDITIONS BEFORE FABRICATION.
6. ALL DOOR AND WINDOW DIMENSIONS ARE MASONARY DIMENSIONS
7. CORELATE STRUCTURAL & ARCHITECT'S DWGS. AND GET BACK TO ARCHITECT WITH DISCREPANCIES IF ANY.

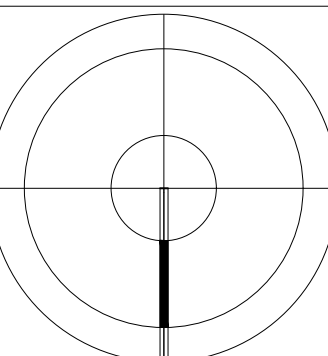	2	02.08.22	TENDER DRAWING		
	No.	DATE	ISSUE/ REVISION		
	<u>I I T BOMBAY: VANVIHAR GUEST HOUSE</u>				
	POWAI, MUMBAI - 400 076, INDIA				
	UPENDRA NAYAK & ASSOCIATES				
	ARCHITECTS. INTERIOR DESIGNERS				
	1, SULBHA NIWAS. DILIP GUPTA MARG. MAHIM. MUMBAI 400016				
TEL: 24458473 FAX:24446223					
DATE:21.02.2022		SCALE:AS NOTED	DRAWN BY:HR	CHECKED BY:AB	

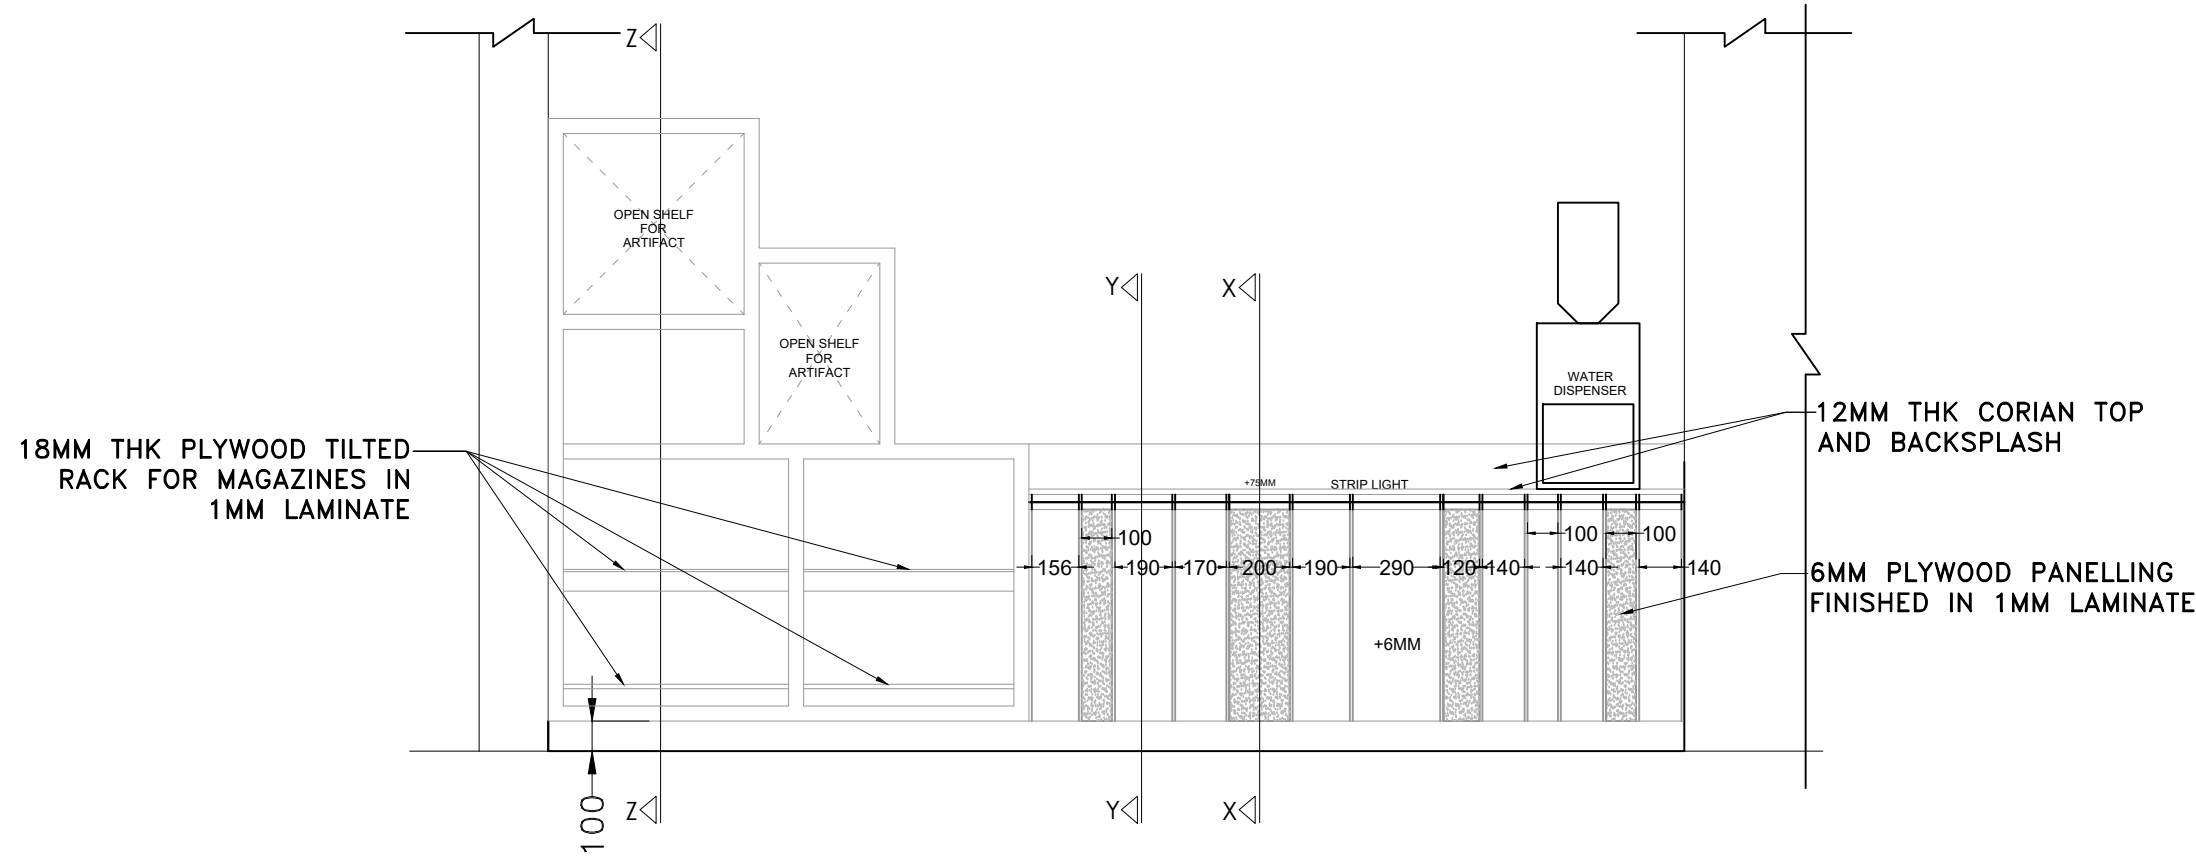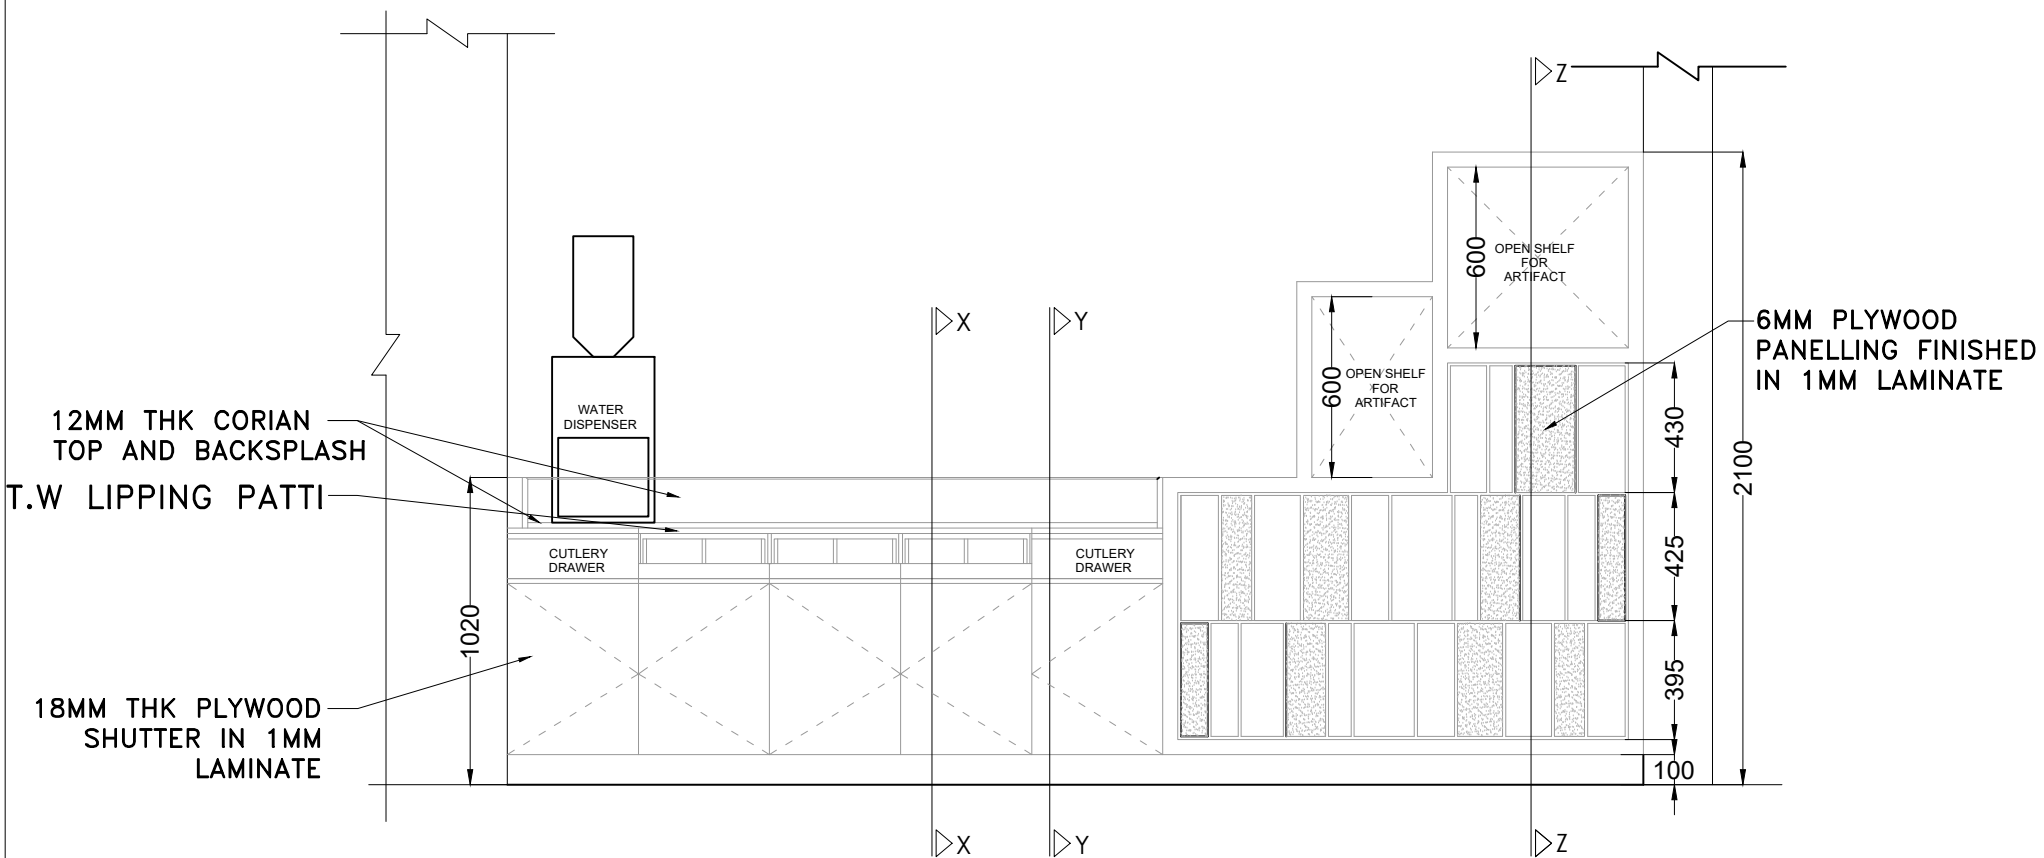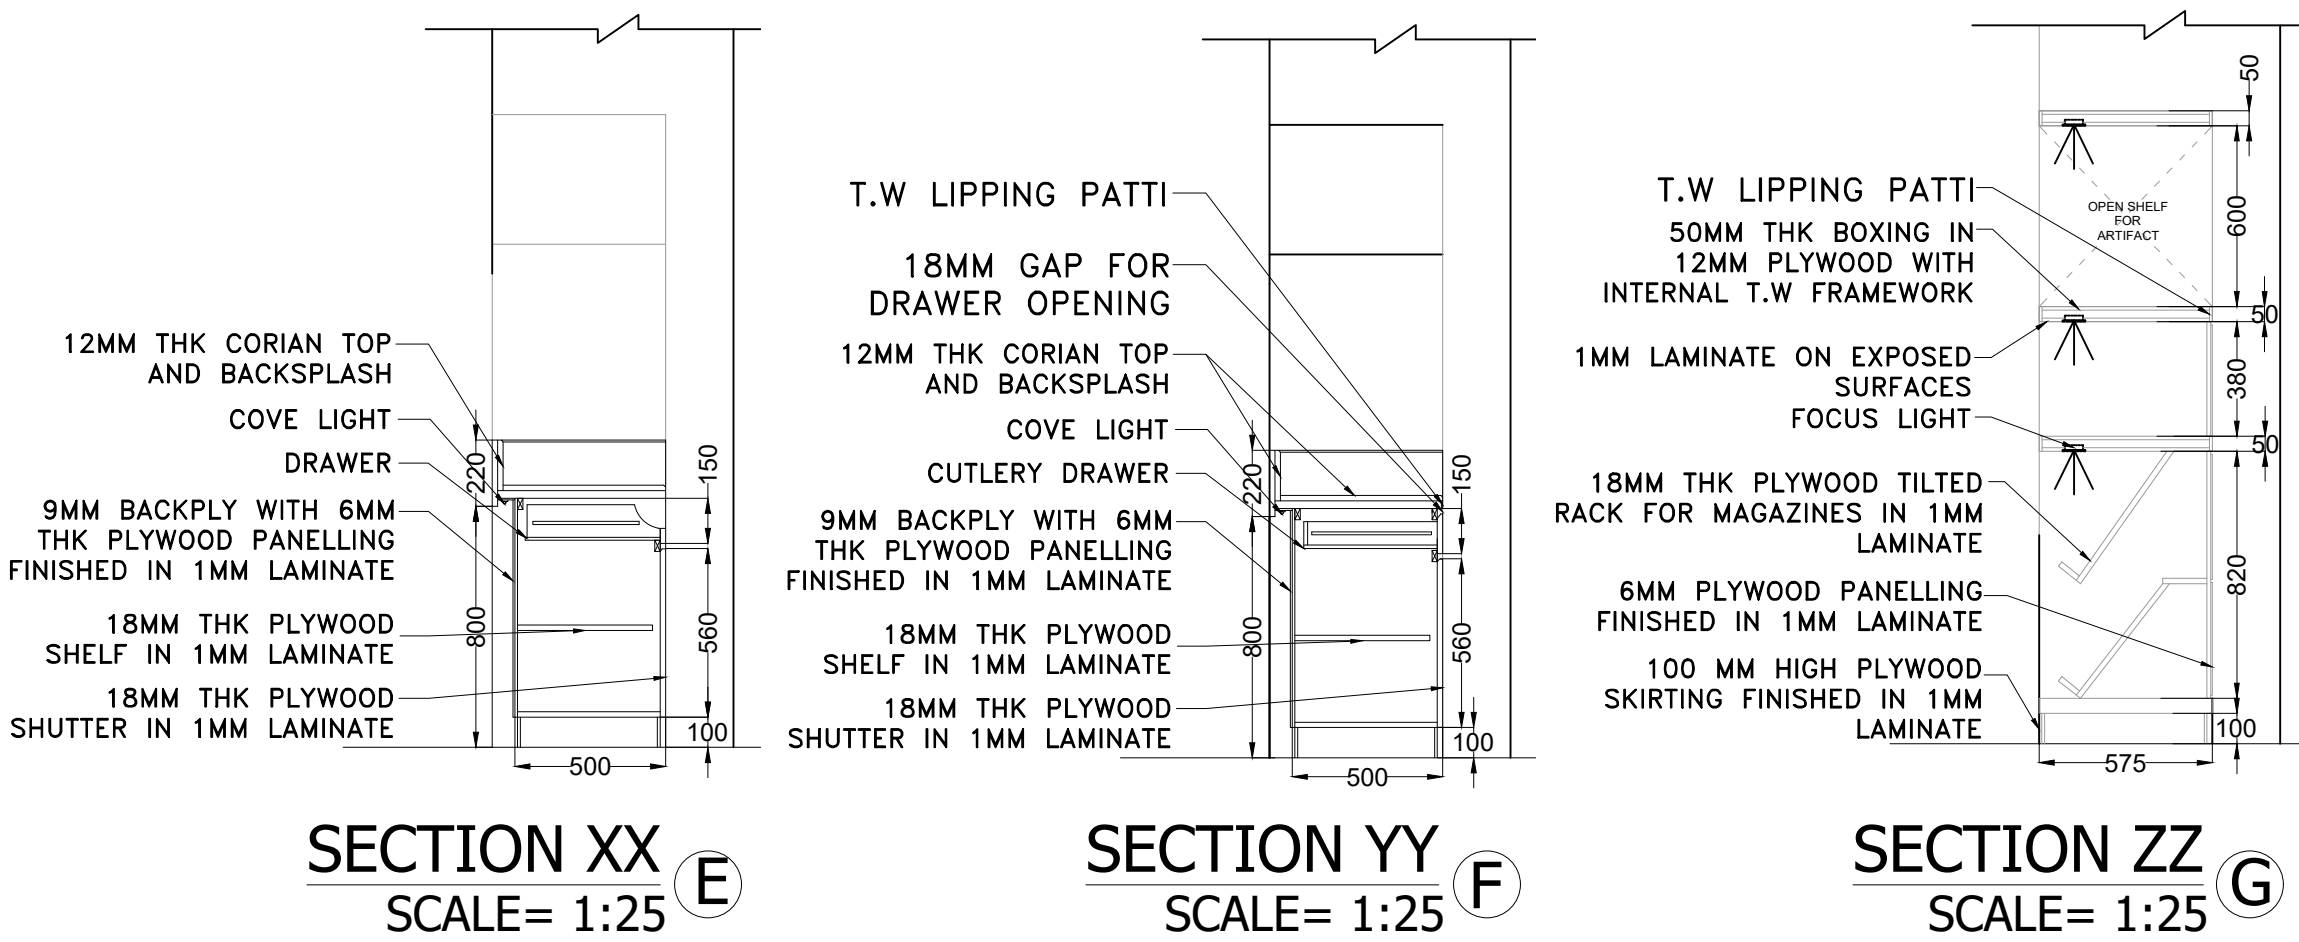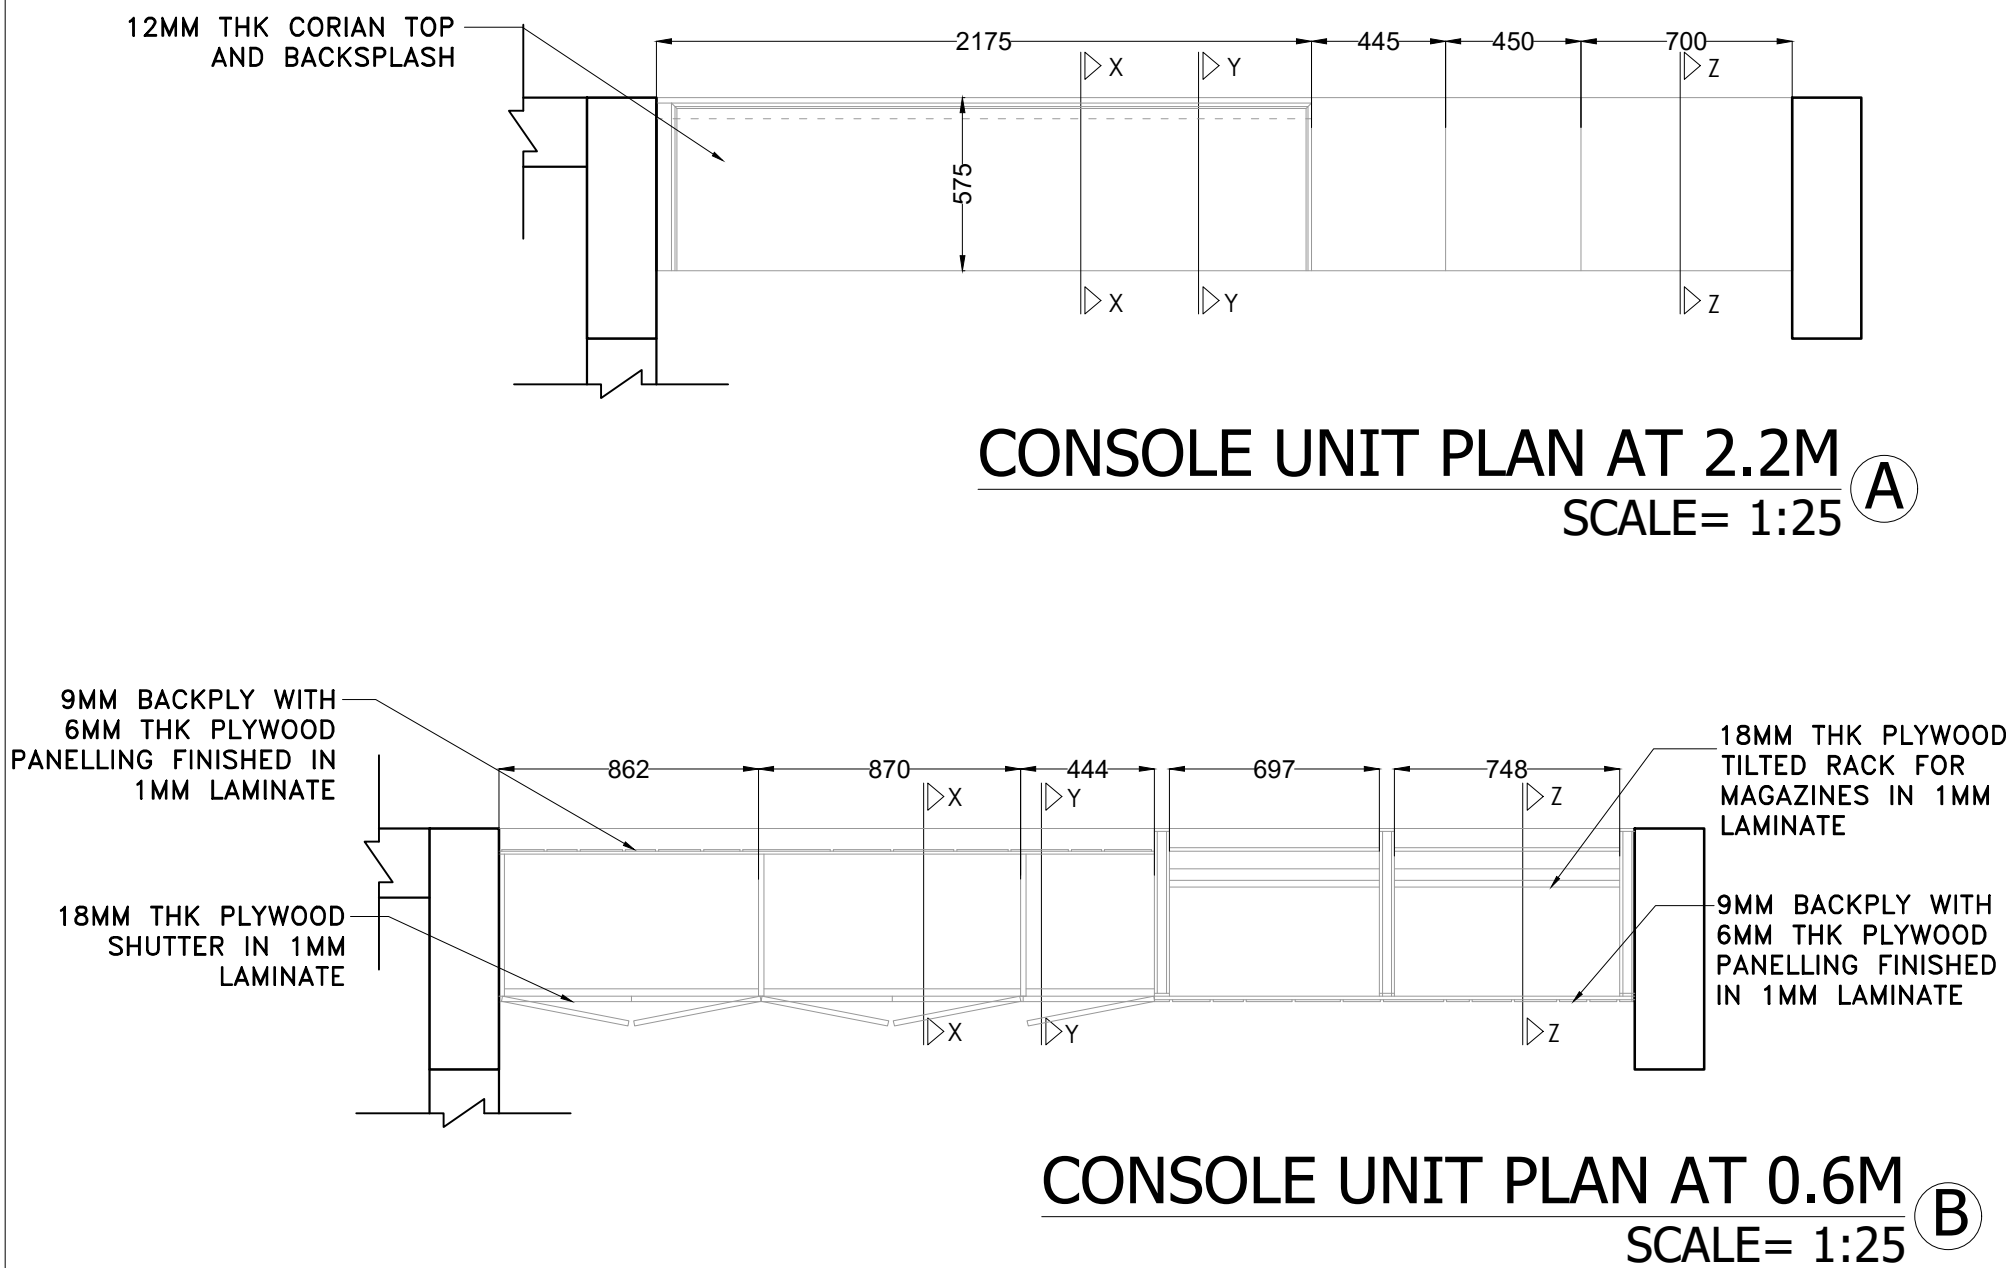


CONSOLE TABLE DETAIL - 04

NOTES:


1. DRAWINGS SHALL NOT BE SCALED.
2. ALL DIMENSIONS ARE IN MM.
3. ANY DISCREPANCY IN DRAWINGS AND EXISTING CONDITIONS SHOULD BE BROUGHT TO THE NOTICE OF THE ARCHITECT PRIOR TO PROCEEDING WITH THE ITEM
4. FOR SIZE OF STRUCTURAL MEMBERS REFER STRUCTURAL ENGINEER'S DRAWINGS.
5. ALL DOOR & WINDOW DIMENSIONS LISTED IN SCHEDULES MUST BE VERIFIED WITH SITE CONDITIONS BEFORE FABRICATION.
6. ALL DOOR AND WINDOW DIMENSIONS ARE MASONARY DIMENSIONS
7. CORELATE STRUCTURAL & ARCHITECT'S DWGS. AND GET BACK TO ARCHITECT WITH DISCREPANCIES IF ANY.

una

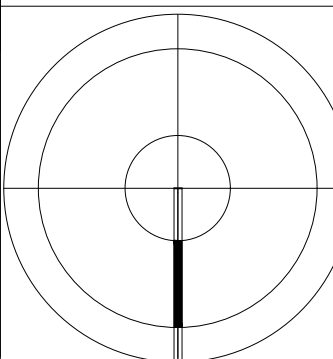


2	02.08.22	TENDER DRAWING	
No.	DATE	ISSUE/ REVISION	
<u>I I T BOMBAY: VANVIHAR GUEST HOUSE</u> POWAI, MUMBAI - 400 076, INDIA			
UPENDRA NAYAK & ASSOCIATES ARCHITECTS. INTERIOR DESIGNERS 1, SULBHA NIWAS. DILIP GUPTA MARG. MAHIM. MUMBAI 400016 TEL: 24458473 FAX:24446223			A8
DATE:21.02.2022	SCALE:AS NOTED	DRAWN BY:HR	


A8

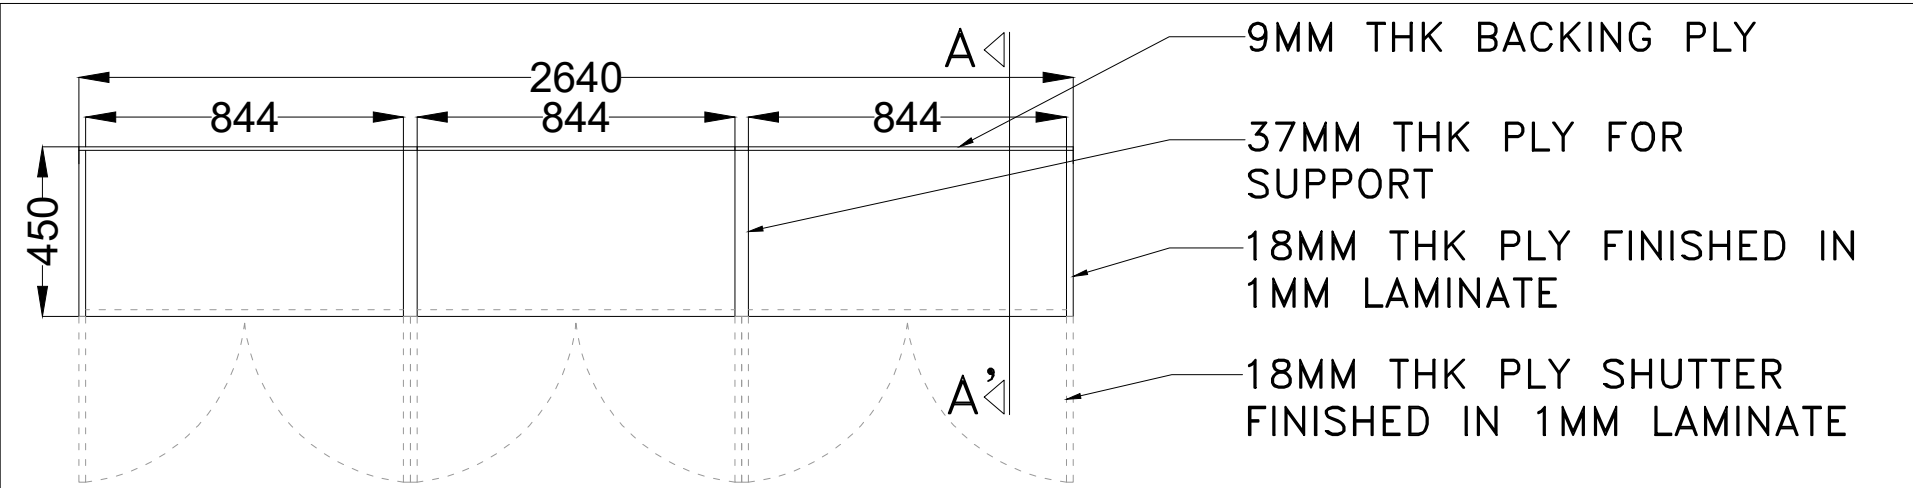

STORAGE UNIT PLAN AT 0.75M
SCALE= 1:20 **(A)**

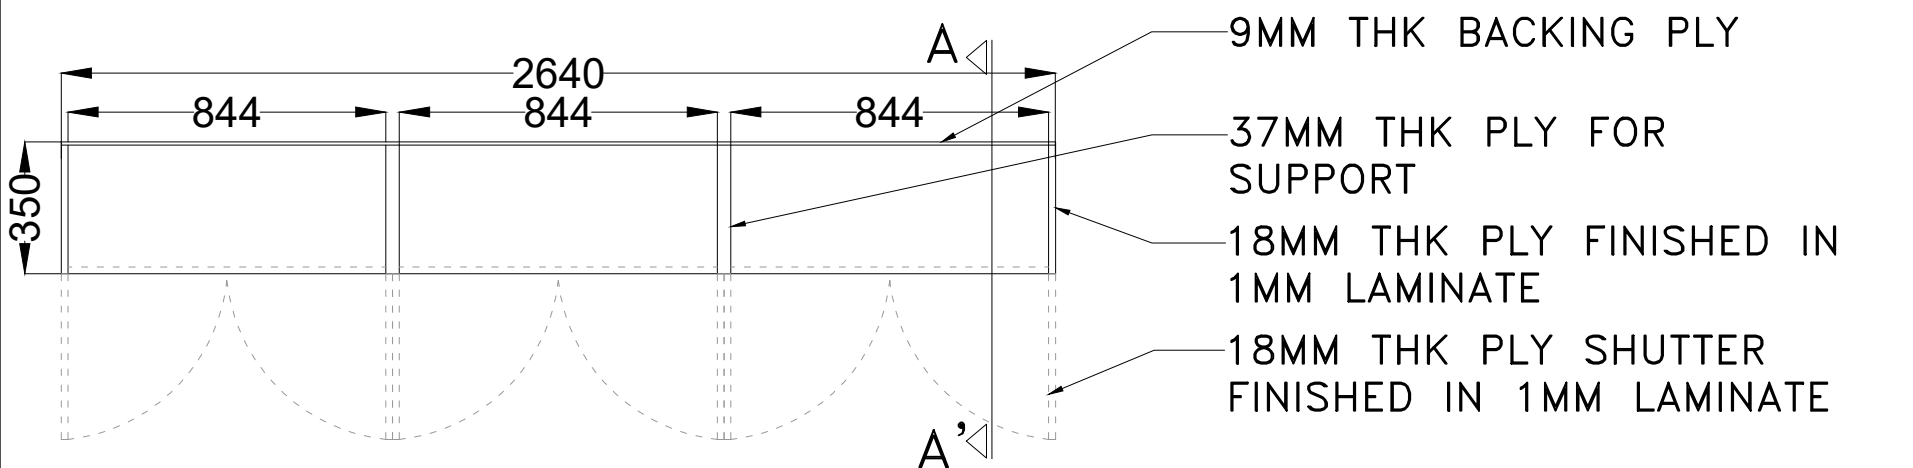

STORAGE UNIT PLAN AT 2.2M
SCALE= 1:20 **(B)**

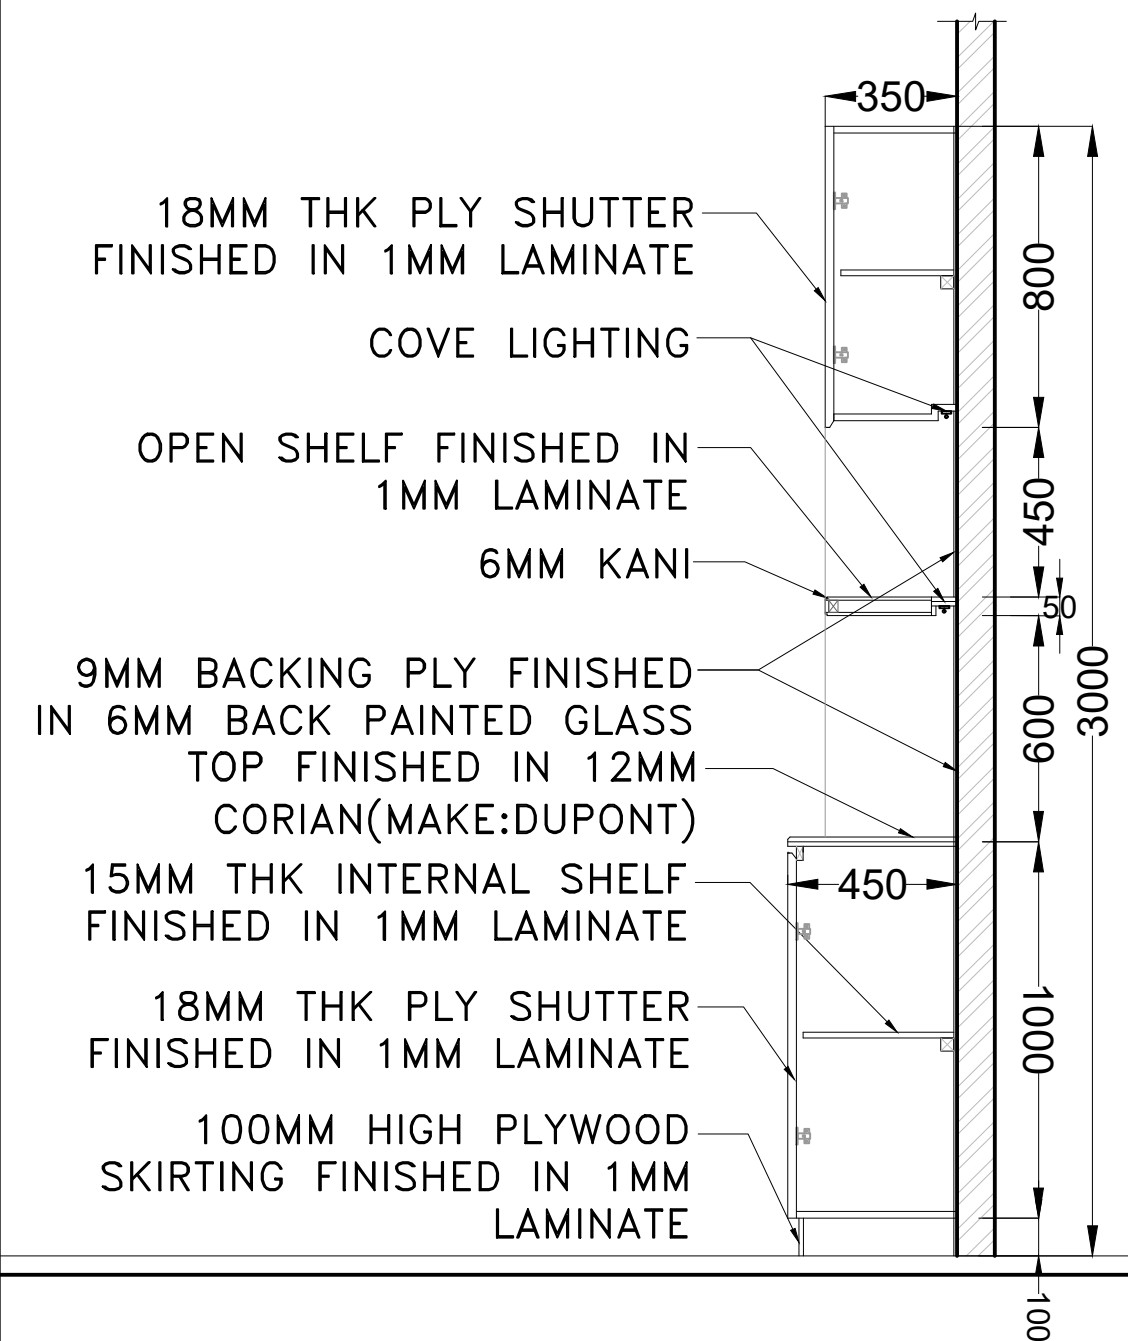


SECTION AA'
SCALE= 1:20 **(D)**

MANAGER CABIN-STORAGE UNIT DETAIL-05


NOTES:

- DRAWINGS SHALL NOT BE SCALED.
- ALL DIMENSIONS ARE IN MM.
- ANY DISCREPANCY IN DRAWINGS AND EXISTING CONDITIONS SHOULD BE BROUGHT TO THE NOTICE OF THE ARCHITECT PRIOR TO PROCEEDING WITH THE ITEM
- FOR SIZE OF STRUCTURAL MEMBERS REFER STRUCTURAL ENGINEER'S DRAWINGS.
- ALL DOOR & WINDOW DIMENSIONS LISTED IN SCHEDULES MUST BE VERIFIED WITH SITE CONDITIONS BEFORE FABRICATION.
- ALL DOOR AND WINDOW DIMENSIONS ARE MASONARY DIMENSIONS
- CORELATE STRUCTURAL & ARCHITECT'S DWGS. AND GET BACK TO ARCHITECT WITH DISCREPANCIES IF ANY.

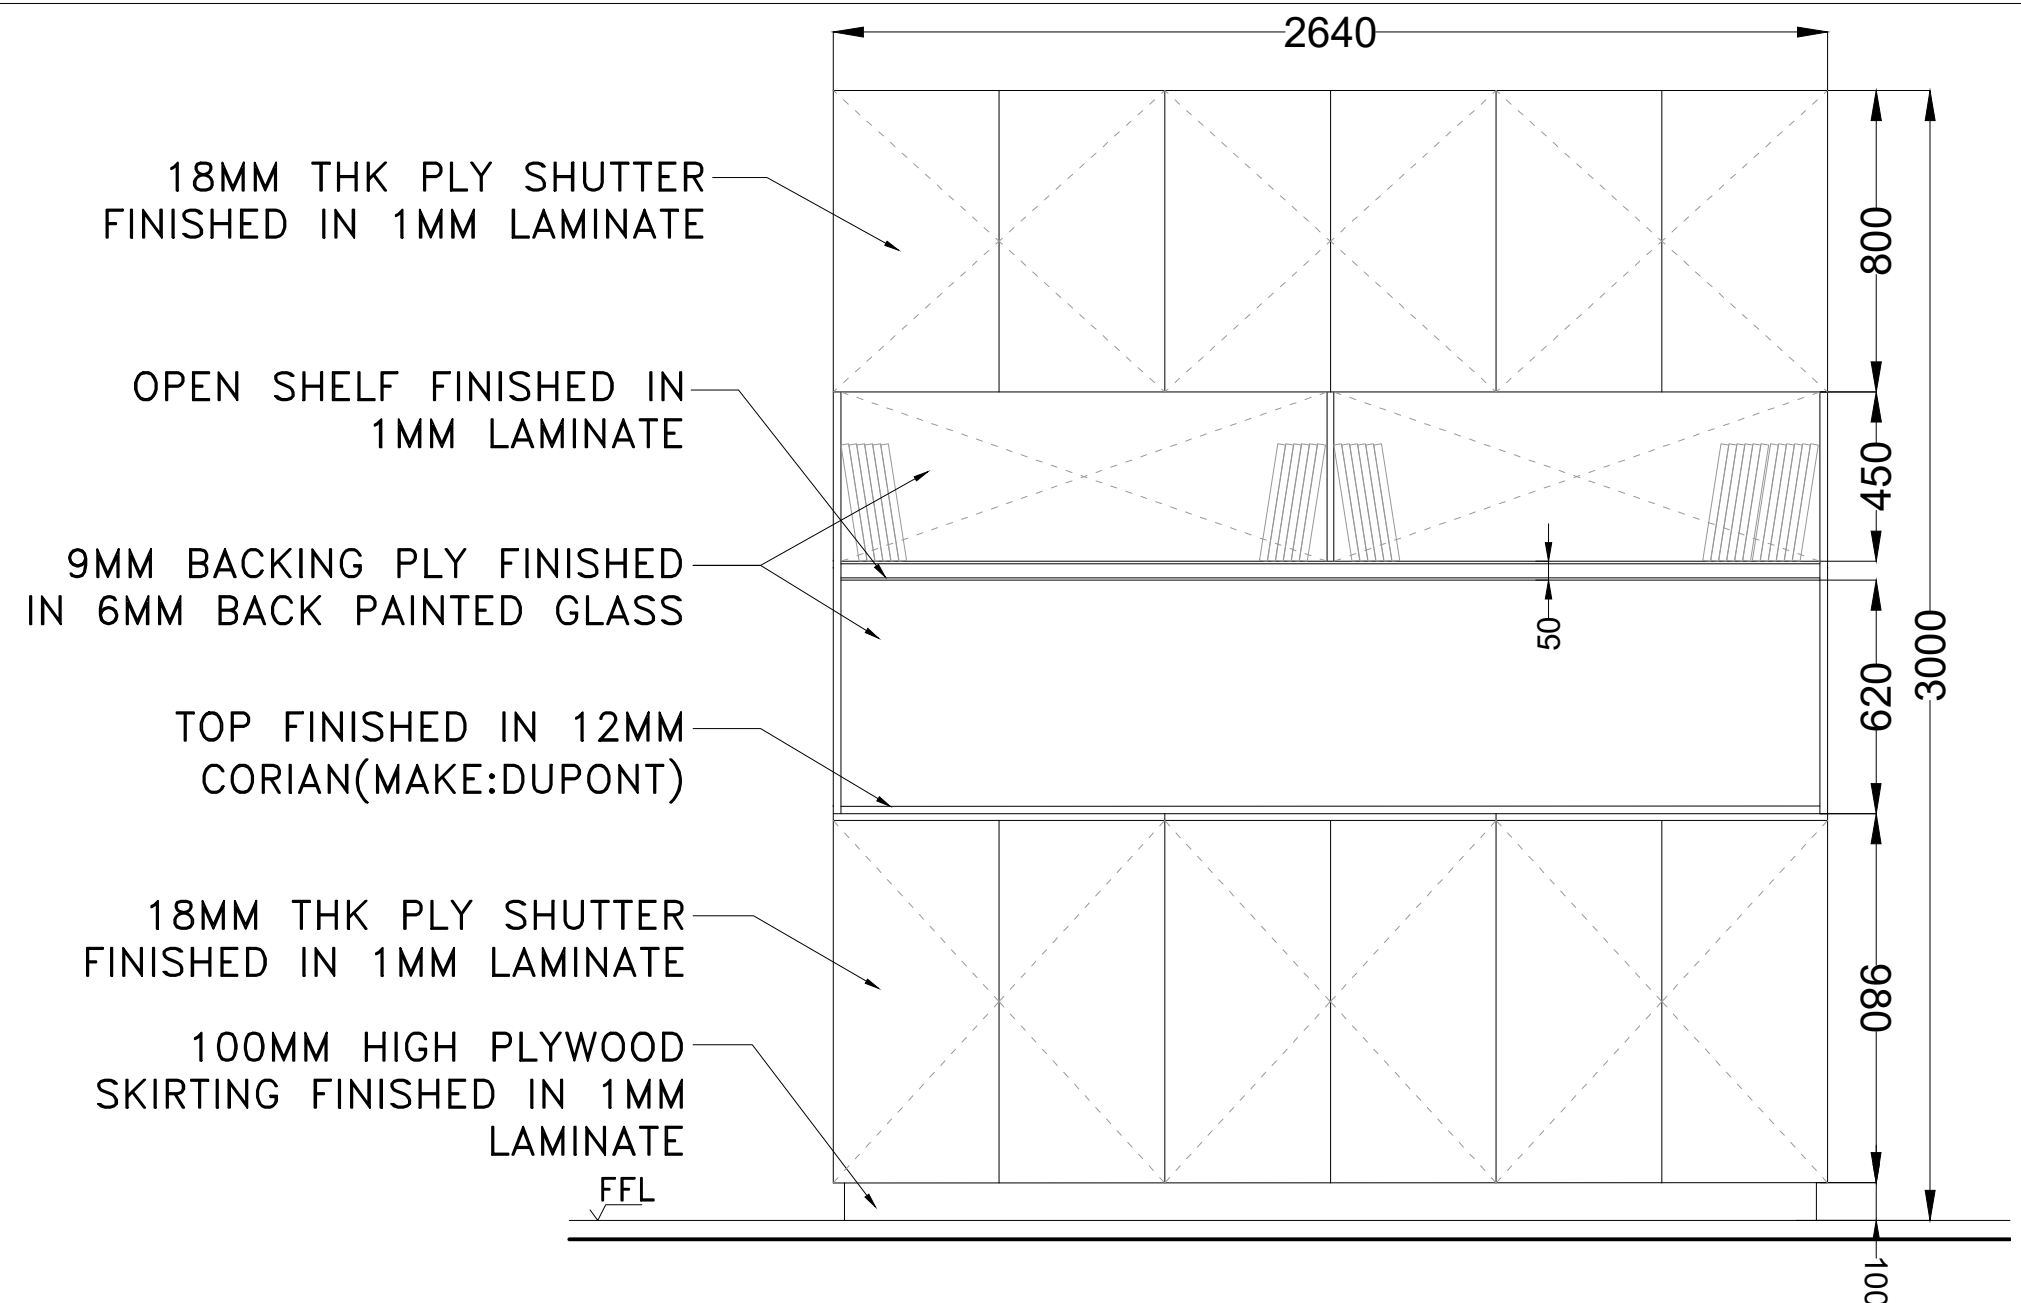


FRONT ELEVATION
SCALE= 1:20 **(C)**

una

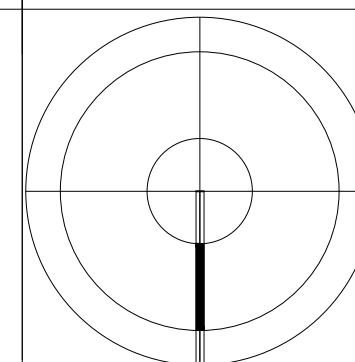


2	02.08.22	TENDER DRAWING
No.	DATE	ISSUE/ REVISION
I I T BOMBAY: VANVIHAR GUEST HOUSE POWAI, MUMBAI - 400 076, INDIA		
UPENDRA NAYAK & ASSOCIATES ARCHITECTS. INTERIOR DESIGNERS 1, SULBHA NIWAS. DILIP GUPTA MARG. MAHIM. MUMBAI 400016 TEL: 24458473 FAX:24446223		
DATE:21.02.2022	SCALE:AS NOTED	DRAWN BY:HR
		CHECKED BY:AB

A9

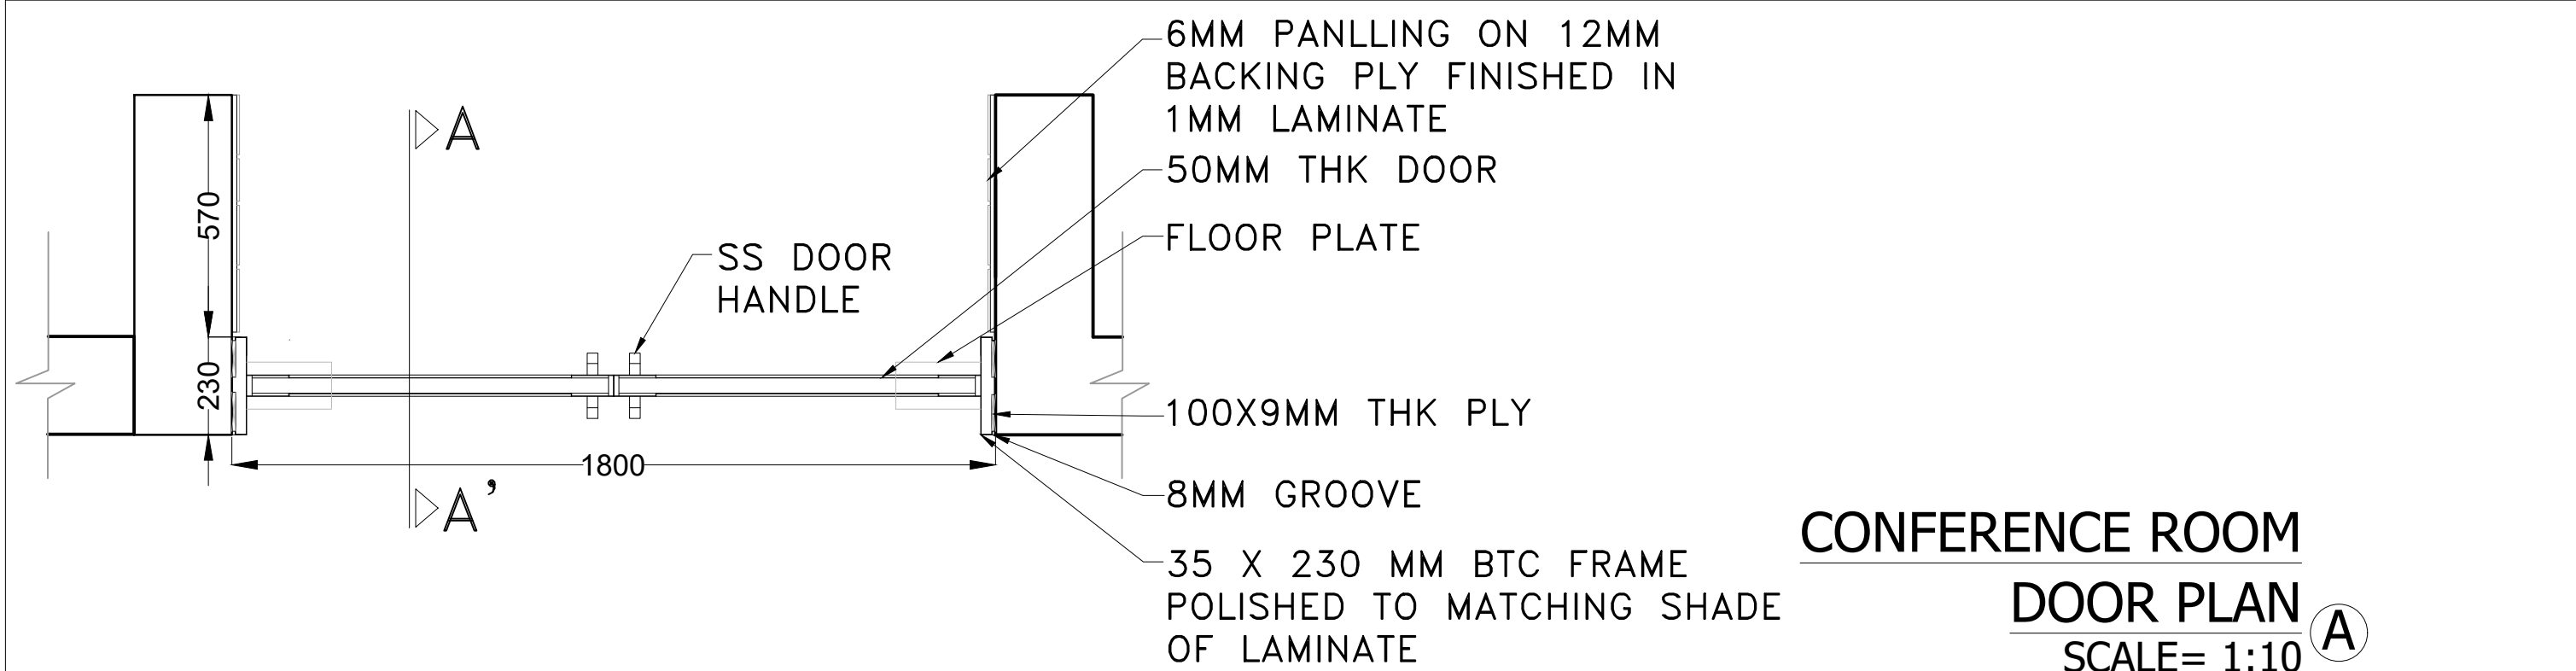


CONFERENCE ROOM
DOOR PLAN A
SCALE= 1:10

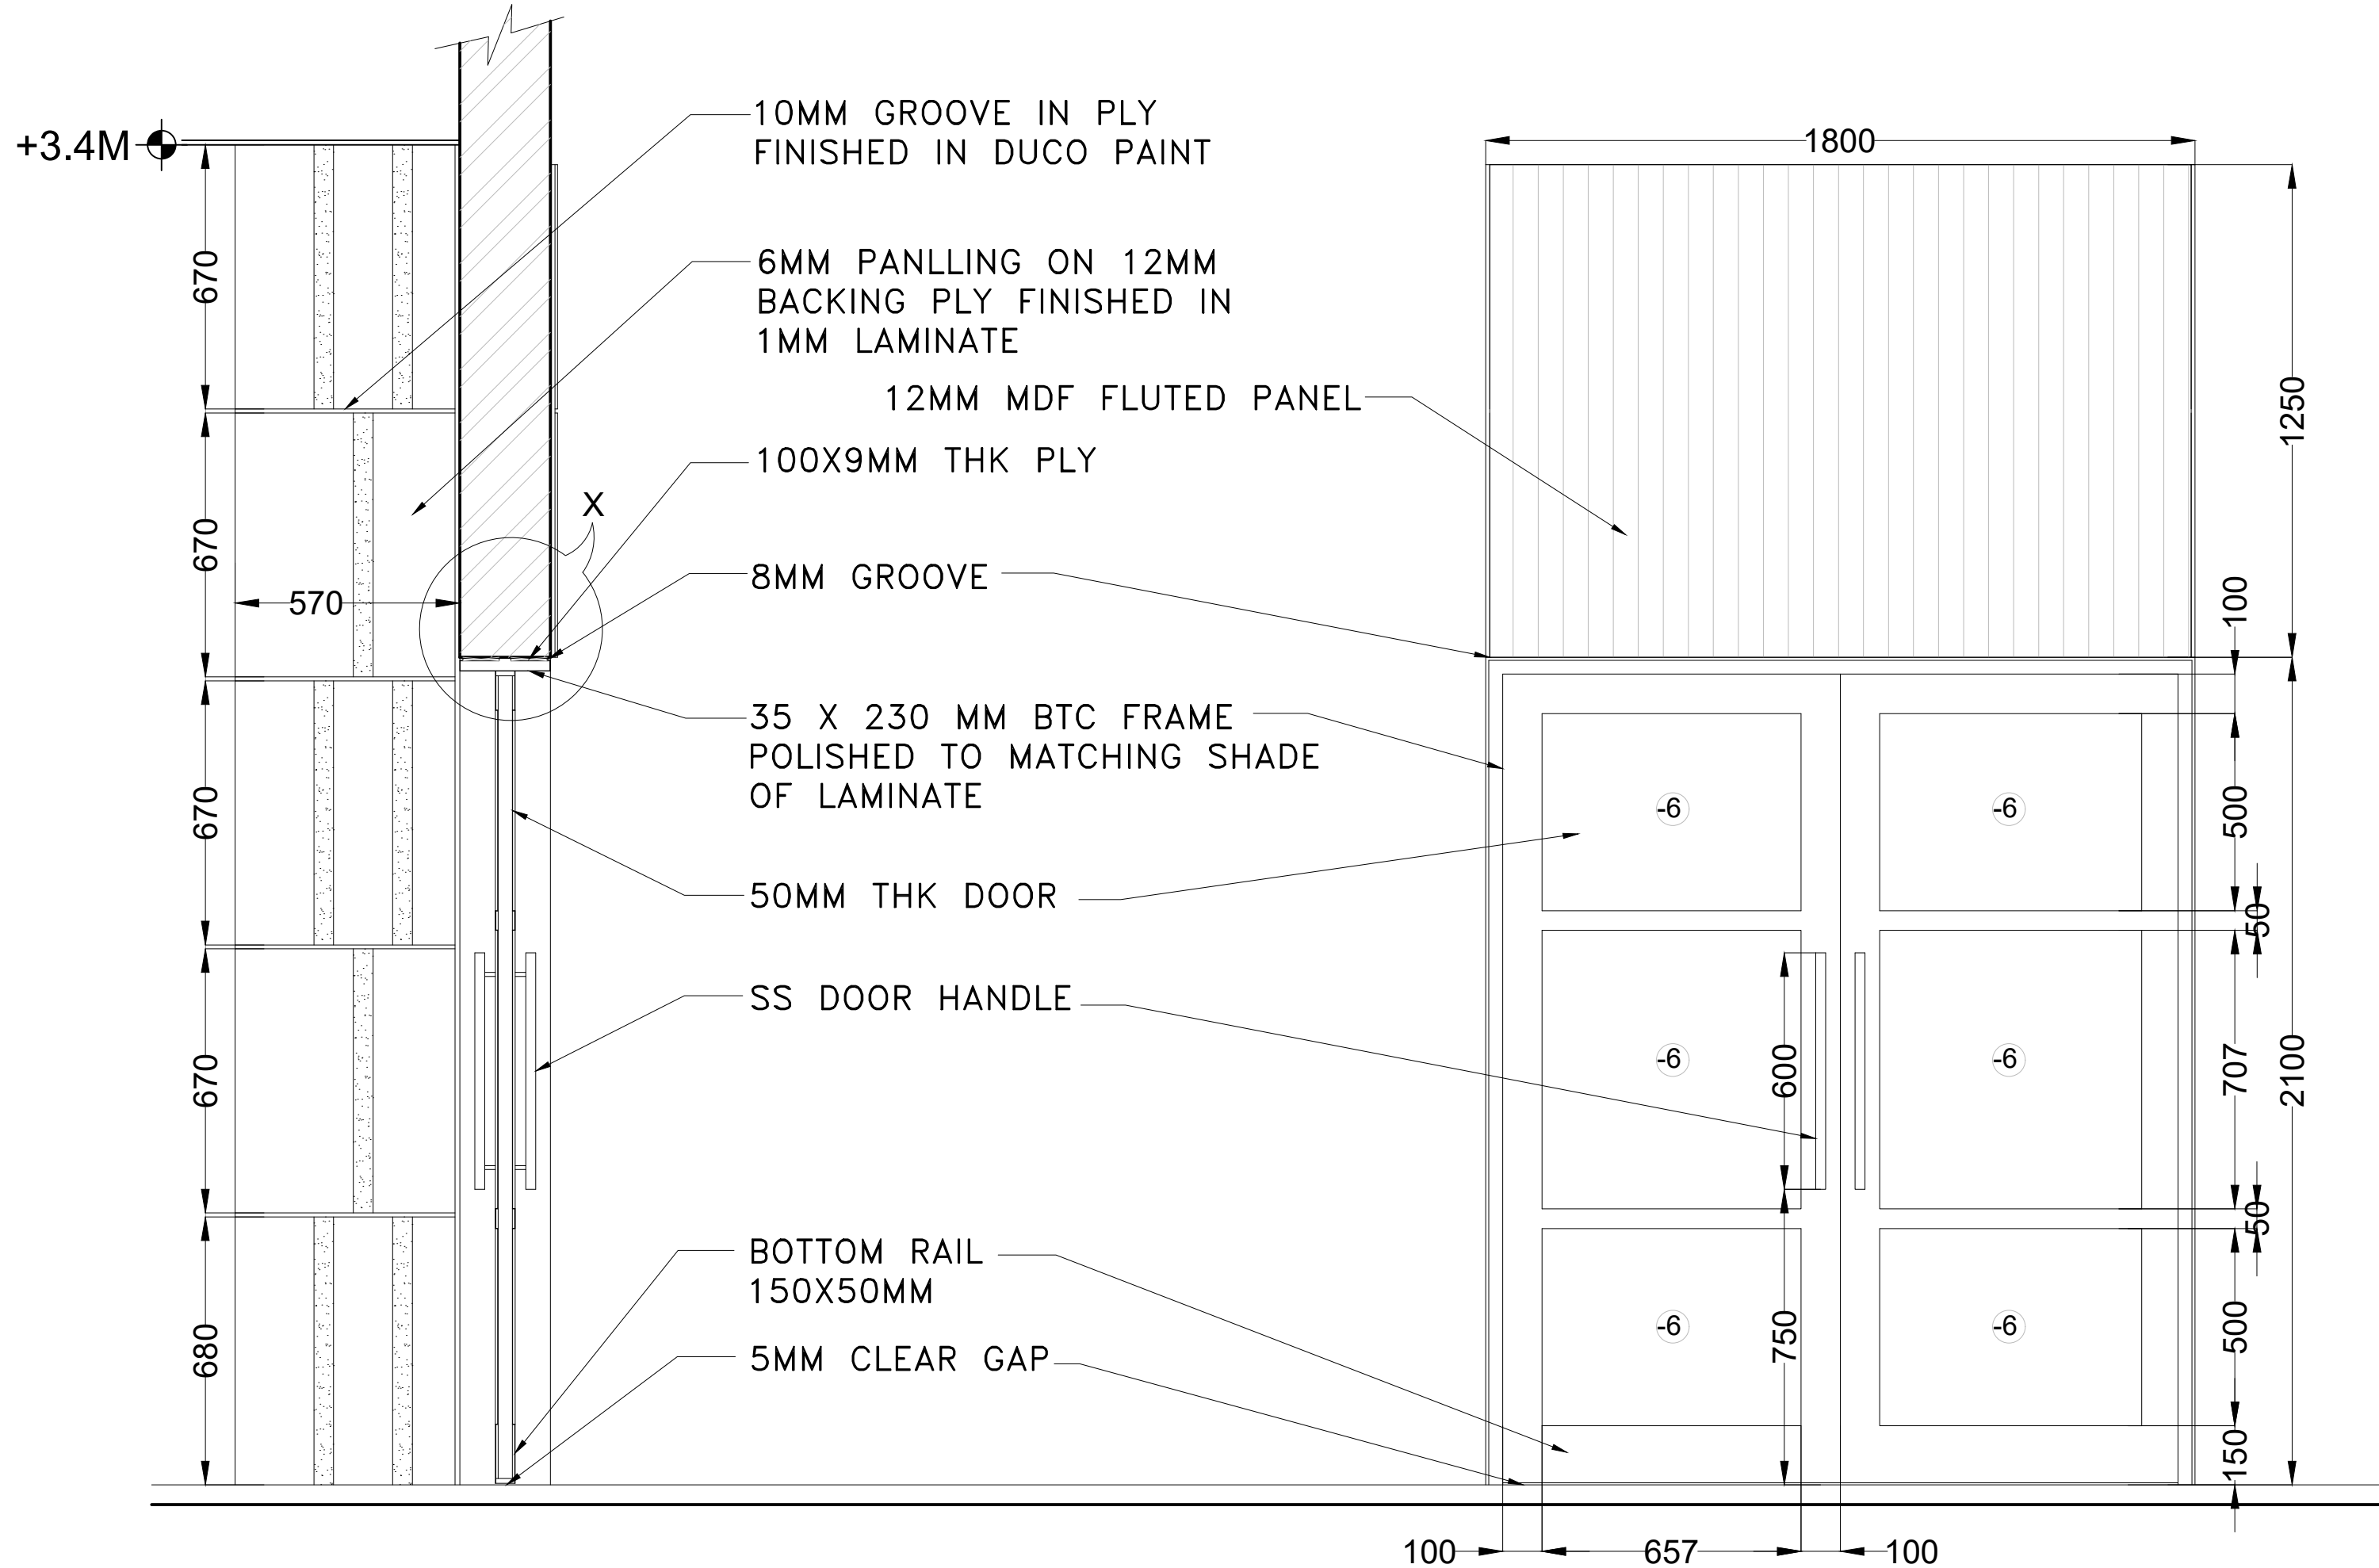

SECTION AA' B
SCALE= 1:15

FRONT ELEVATION C
SCALE= 1:15

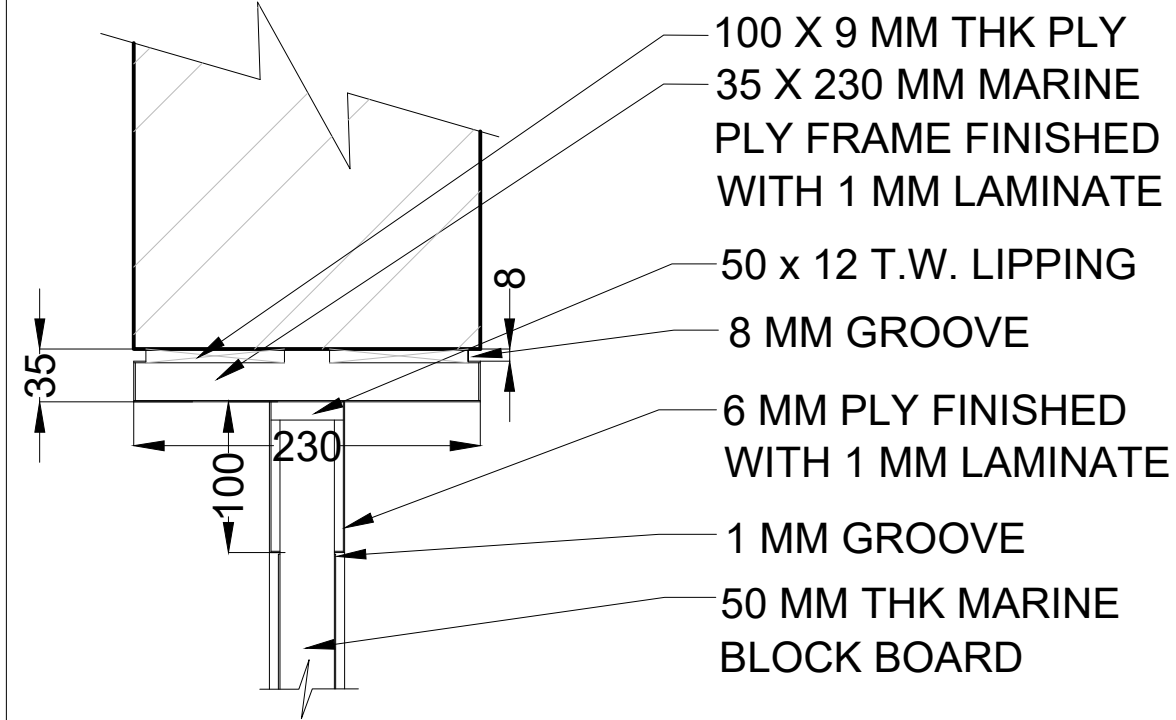


DETAIL AT A D
SCALE= 1:5

CONFERENCE ROOM DOOR DETAIL-06

NOTES:


- DRAWINGS SHALL NOT BE SCALED.
- ALL DIMENSIONS ARE IN MM.
- ANY DISCREPANCY IN DRAWINGS AND EXISTING CONDITIONS SHOULD BE BROUGHT TO THE NOTICE OF THE ARCHITECT PRIOR TO PROCEEDING WITH THE ITEM
- FOR SIZE OF STRUCTURAL MEMBERS REFER STRUCTURAL ENGINEER'S DRAWINGS.
- ALL DOOR & WINDOW DIMENSIONS LISTED IN SCHEDULES MUST BE VERIFIED WITH SITE CONDITIONS BEFORE FABRICATION.
- ALL DOOR AND WINDOW DIMENSIONS ARE MASONARY DIMENSIONS
- CORELATE STRUCTURAL & ARCHITECT'S DWGS. AND GET BACK TO ARCHITECT WITH DISCREPANCIES IF ANY.

una

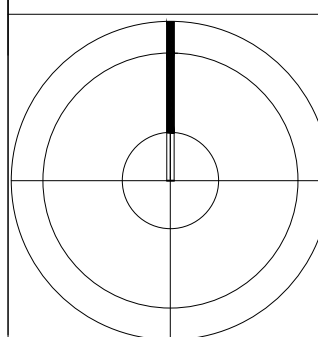

1	02.08.2022	TENDER DRAWINGS
No.	DATE	ISSUE/ REVISION
I I T BOMBAY: VANVIHAR GUEST HOUSE		
POWAI, MUMBAI - 400 076, INDIA		
UPENDRA NAYAK & ASSOCIATES		
ARCHITECTS. INTERIOR DESIGNERS		
1, SULBHA NIWAS, DILIP GUPTA MARG. MAHIM. MUMBAI 400016		
TEL: 24458473 FAX:24446223		
DATE: 21.02.22	SCALE: AS NOTED	DRAWN BY: HR

A10

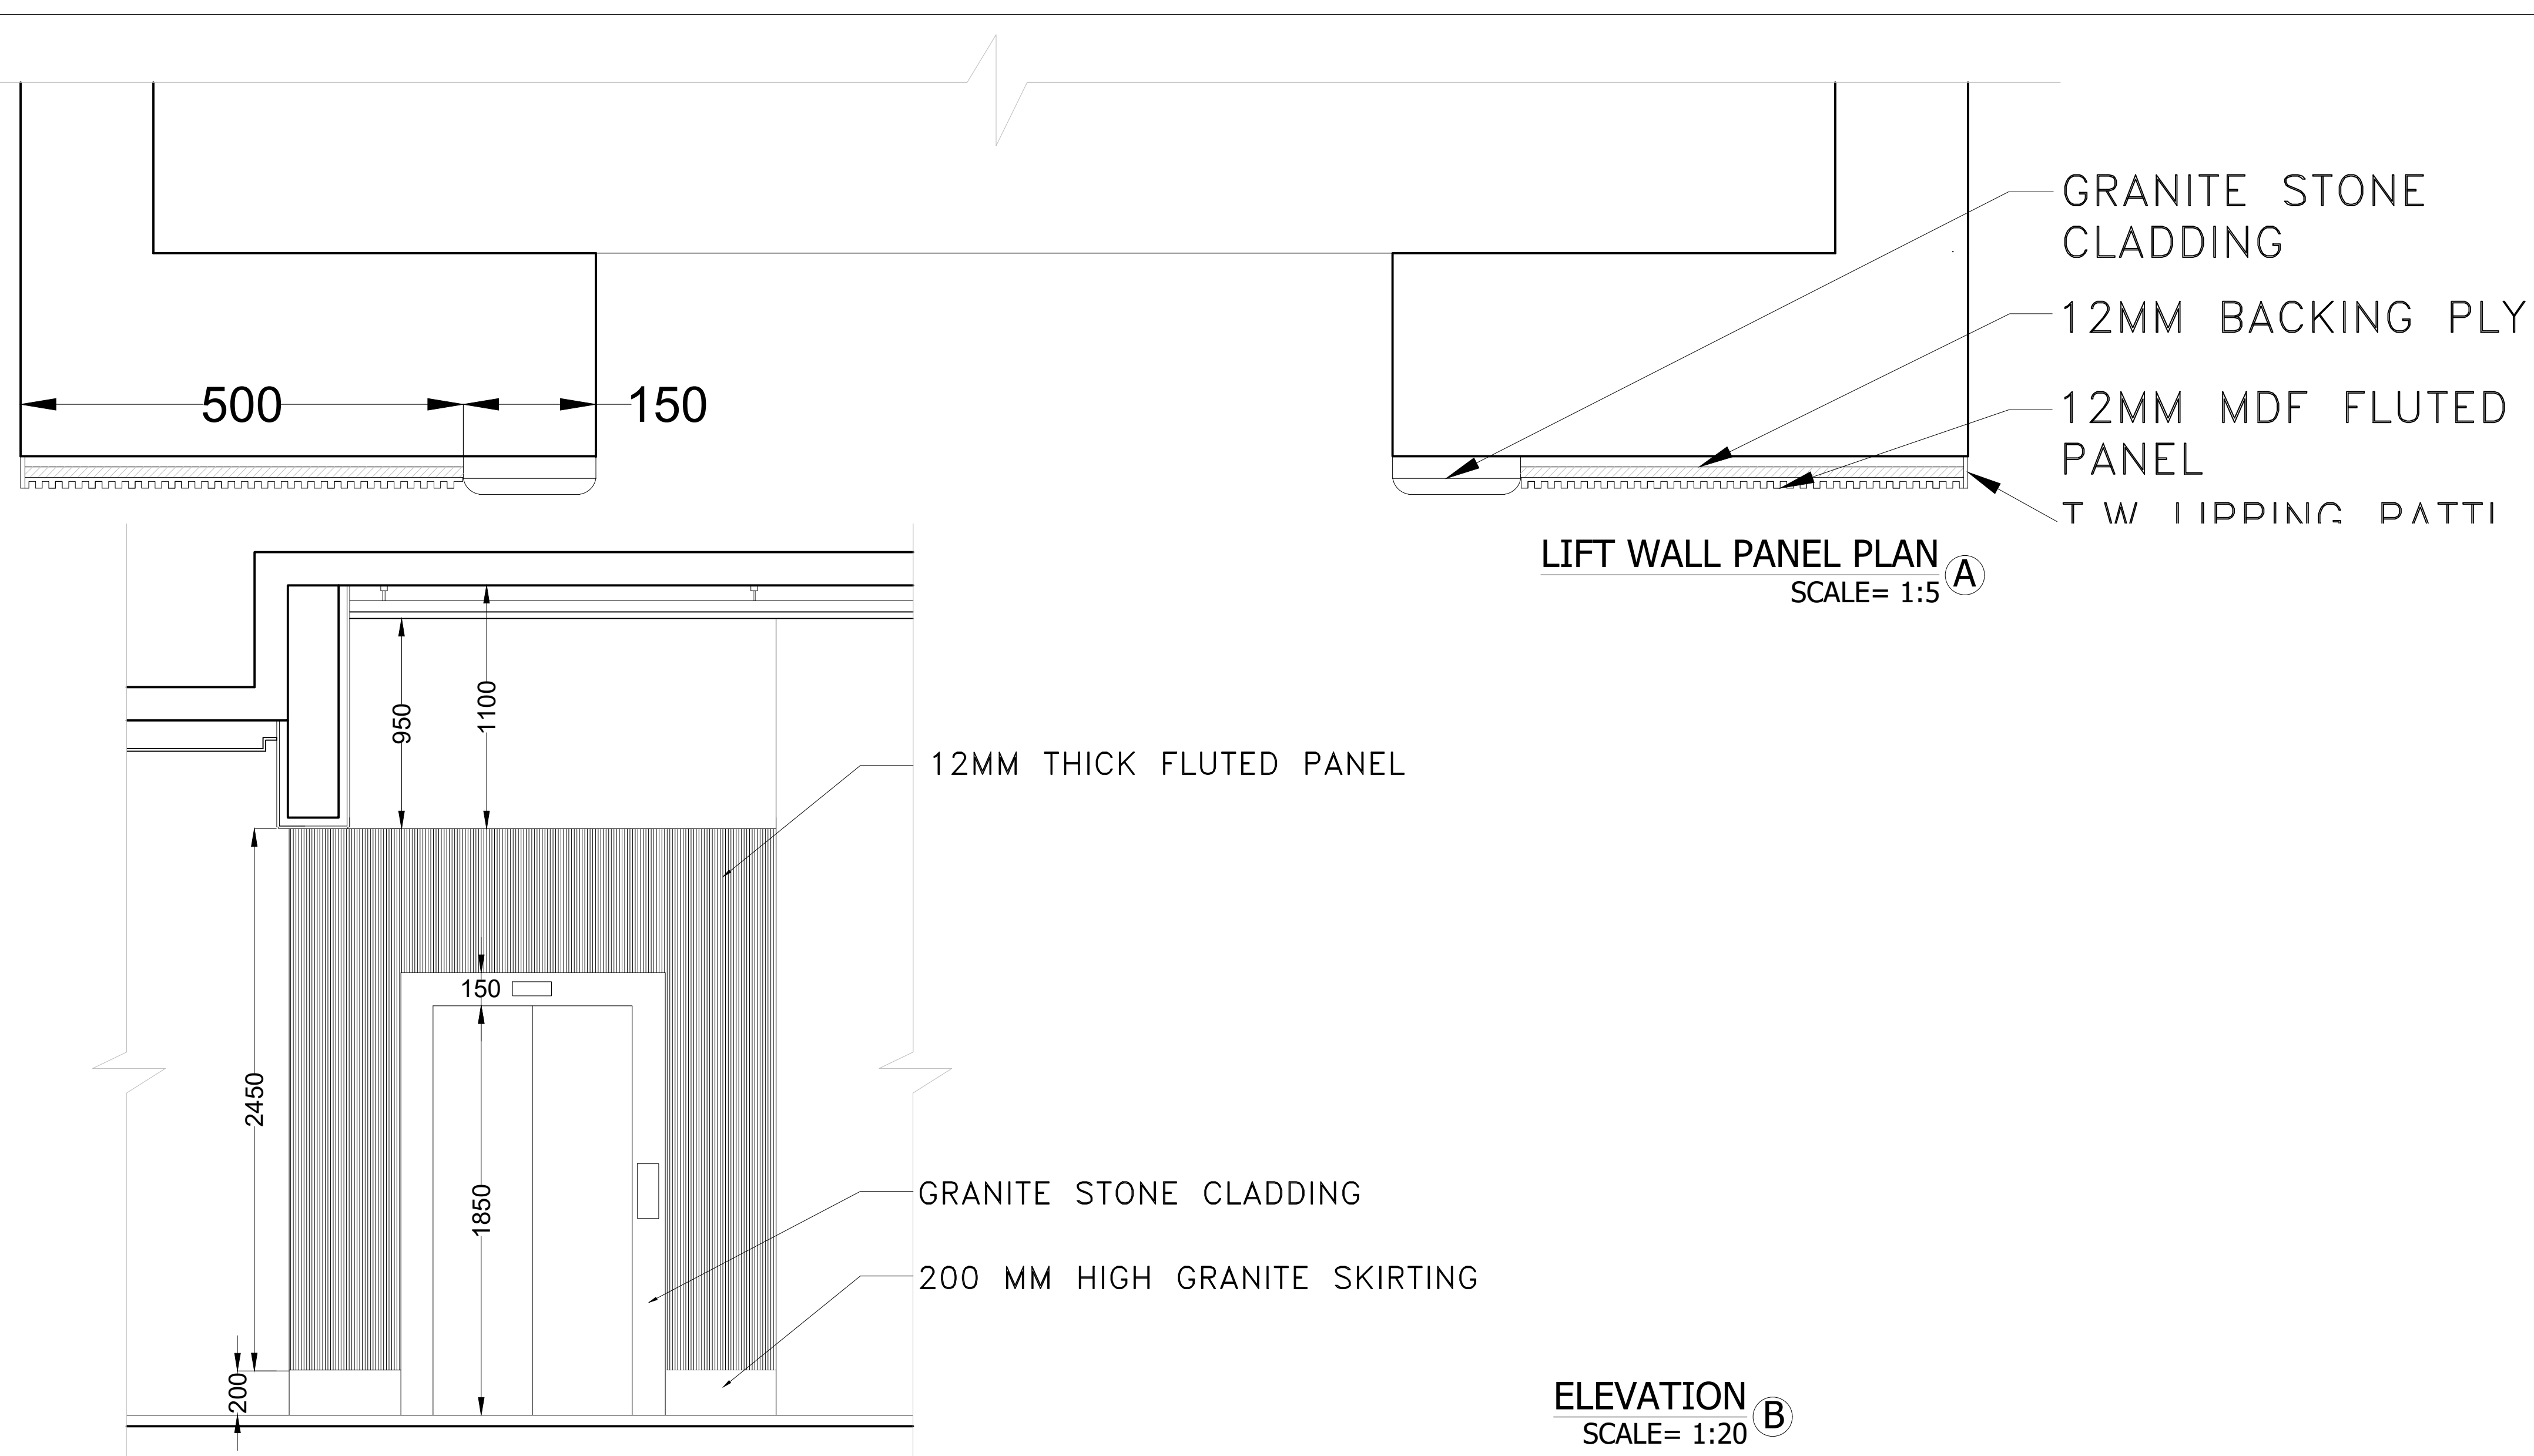


LIFT WALL PANEL DETAIL-08


NOTES:

- 1. DRAWINGS SHALL NOT BE SCALED.
- 2. ALL DIMENSIONS ARE IN MM.
- 3. ANY DISCREPANCY IN DRAWINGS AND EXISTING CONDITIONS SHOULD BE BROUGHT TO THE NOTICE OF THE ARCHITECT PRIOR TO PROCEEDING WITH THE ITEM
- 4. FOR SIZE OF STRUCTURAL MEMBERS REFER STRUCTURAL ENGINEER'S DRAWINGS.
- 5. ALL DOOR & WINDOW DIMENSIONS LISTED IN SCHEDULES MUST BE VERIFIED WITH SITE CONDITIONS BEFORE FABRICATION.
- 6. ALL DOOR AND WINDOW DIMENSIONS ARE MASONARY DIMENSIONS
- 7.CORELATE STRUCTURAL & ARCHITECT'S DWGS. AND GET BACK TO ARCHITECT WITH DISCREPANCIES IF ANY.


ELEVATION B
SCALE= 1:20

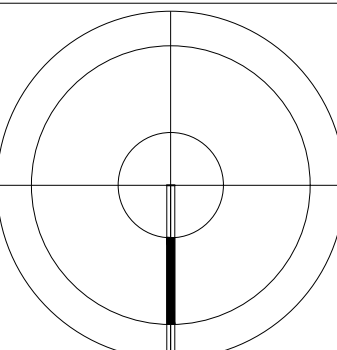

2	02.08.22	TENDER DRAWING	
No.	DATE	ISSUE/ REVISION	
I I T BOMBAY: VANVIHAR GUEST HOUSE POWAI, MUMBAI - 400 076, INDIA			
UPENDRA NAYAK & ASSOCIATES ARCHITECTS. INTERIOR DESIGNERS 1, SULBHA NIWAS. DILIP GUPTA MARG. MAHIM. MUMBAI 400016 TEL: 24458473 FAX:24446223			A12
DATE:21.02.2022	SCALE:AS NOTED	DRAWN BY:HR	

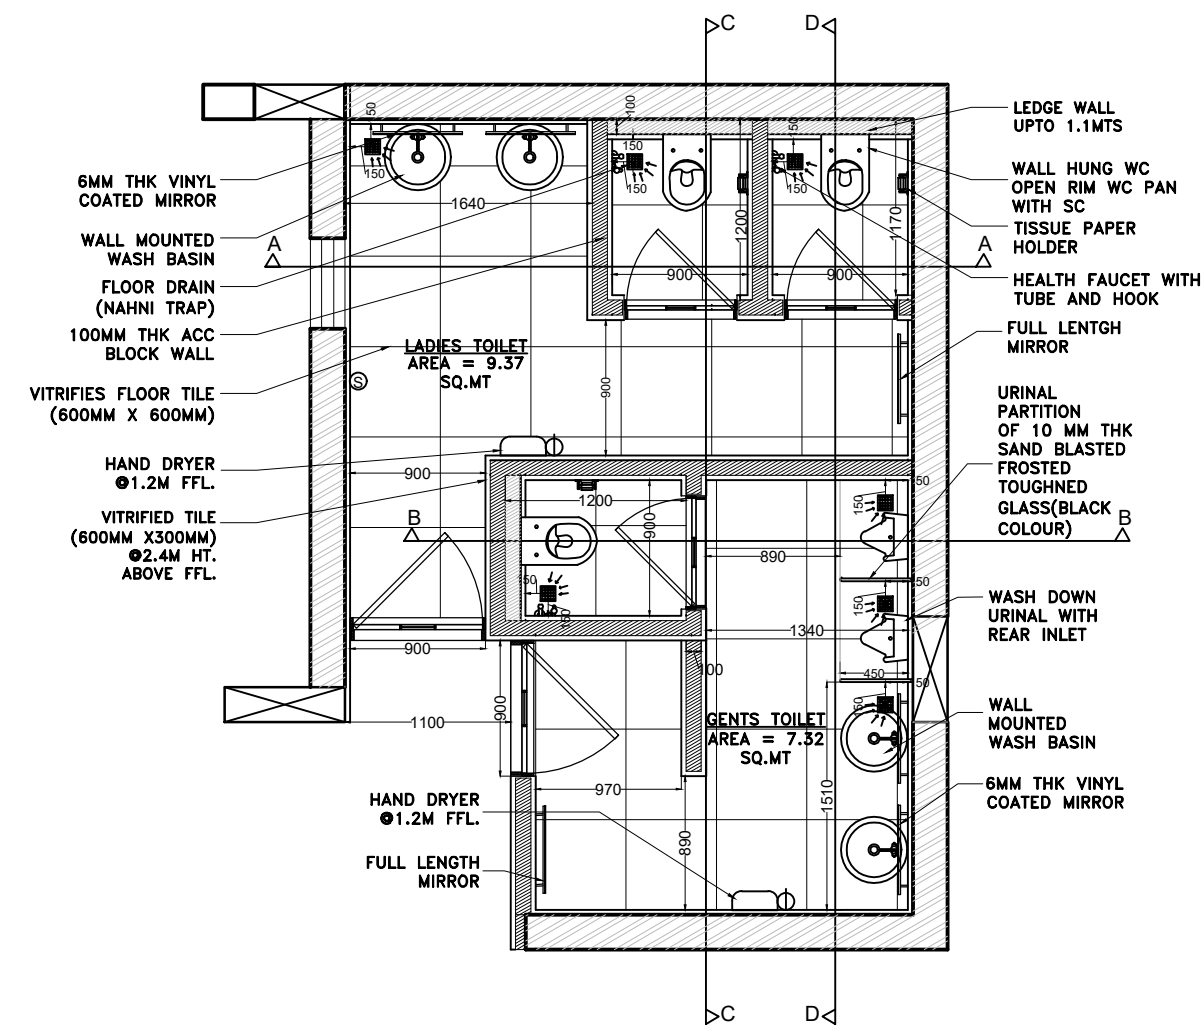


TOILET PLAN
SCALE= 1:50

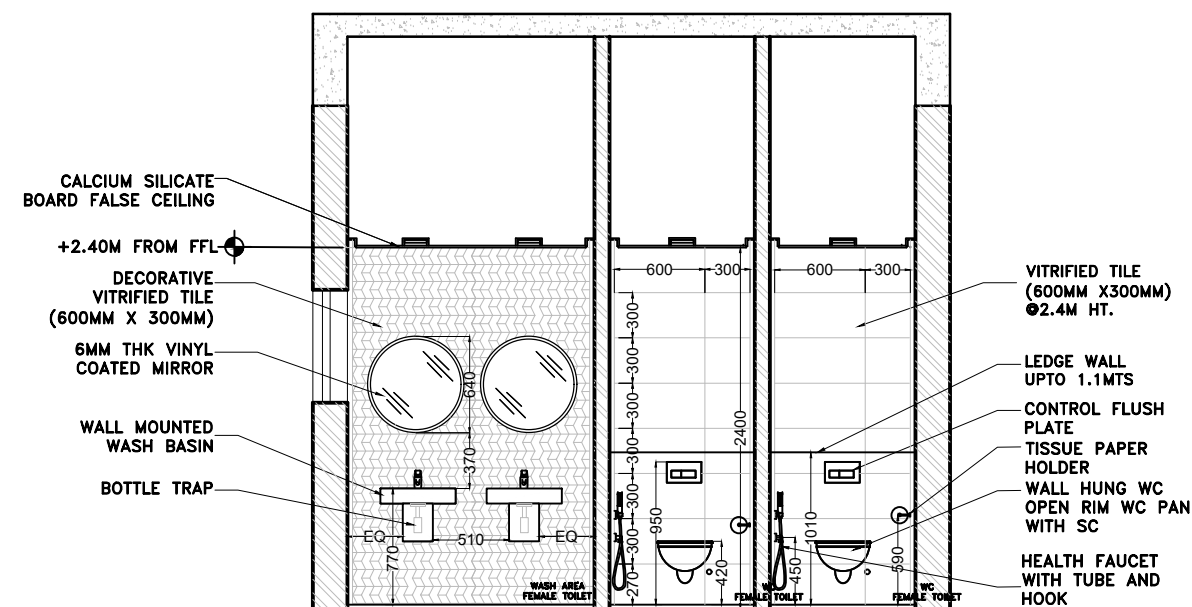


SECTION AA'
SCALE= 1:50


ELEVATION

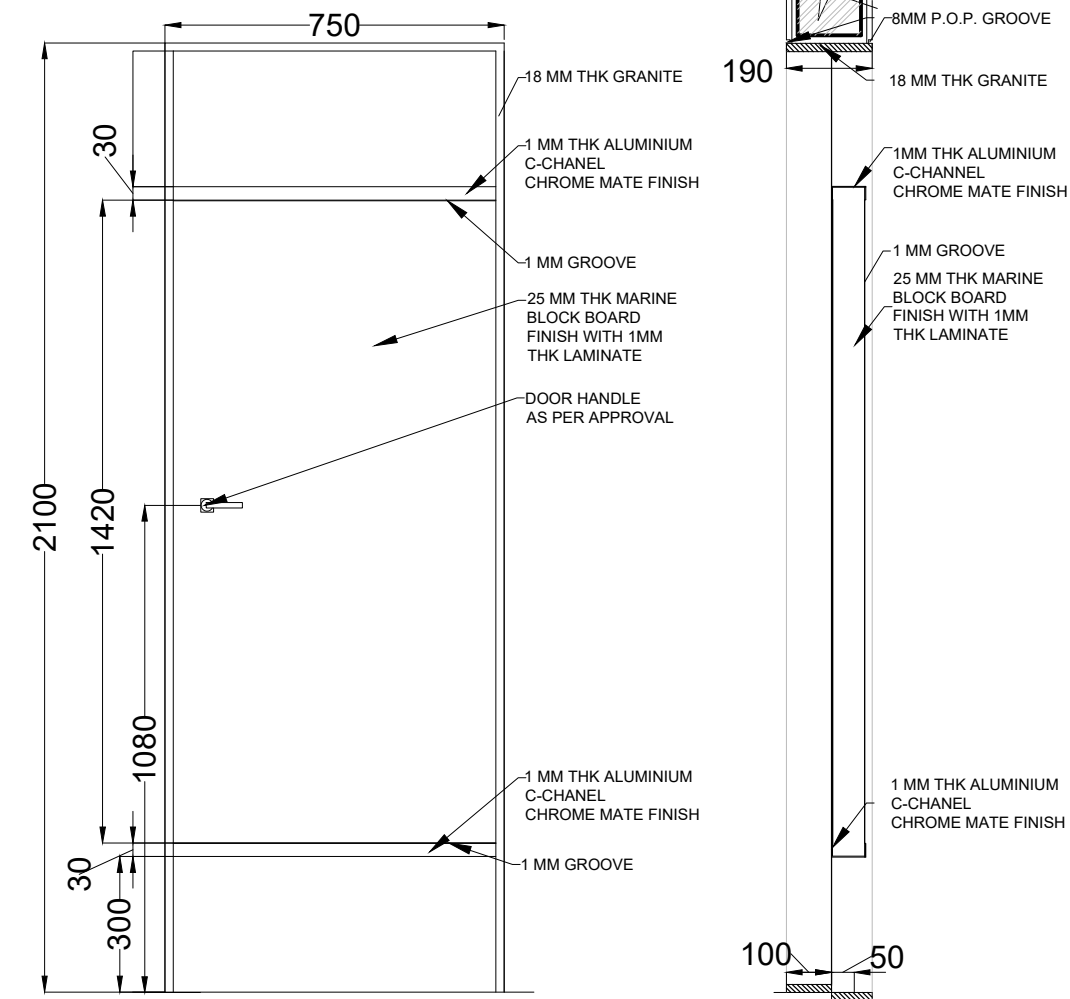


SECTION EE'

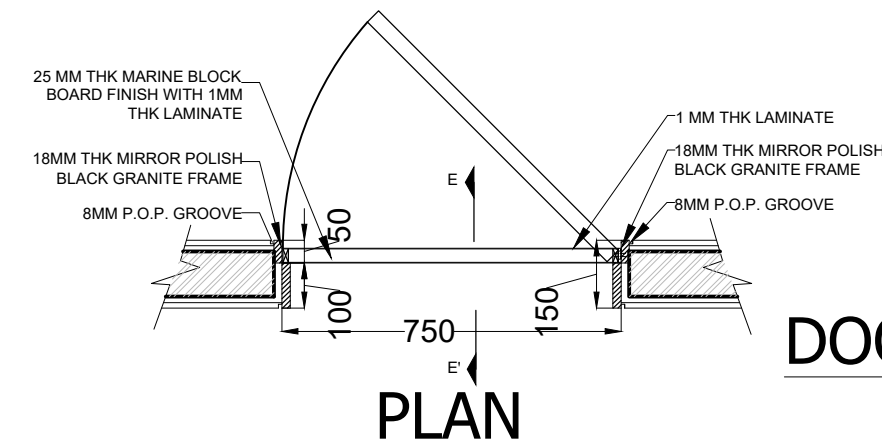


DOOR DETAIL
SCALE= 1:15

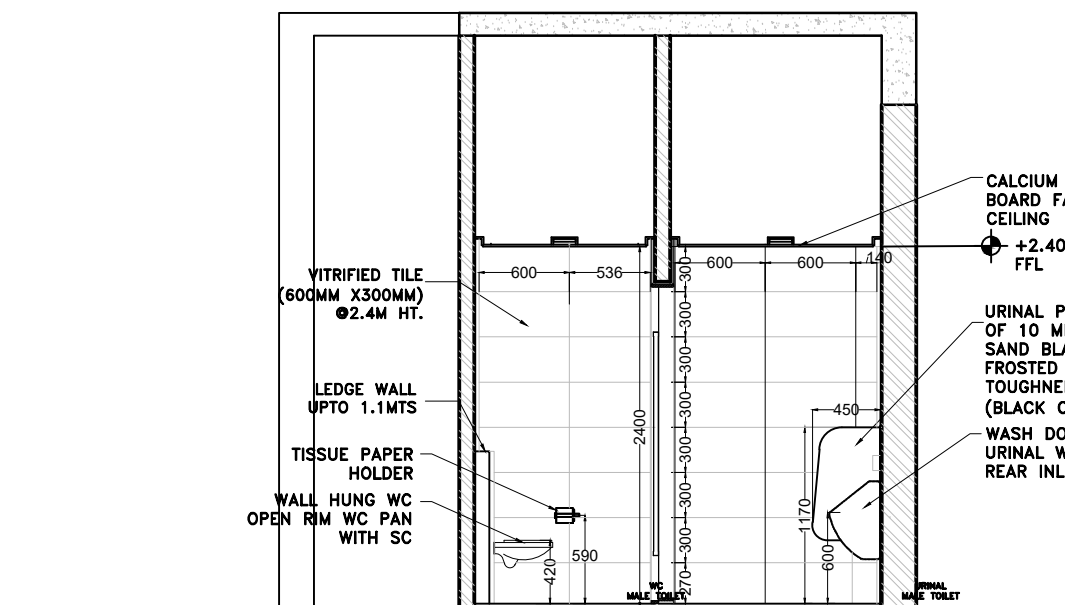

SECTION BB'
SCALE= 1:50

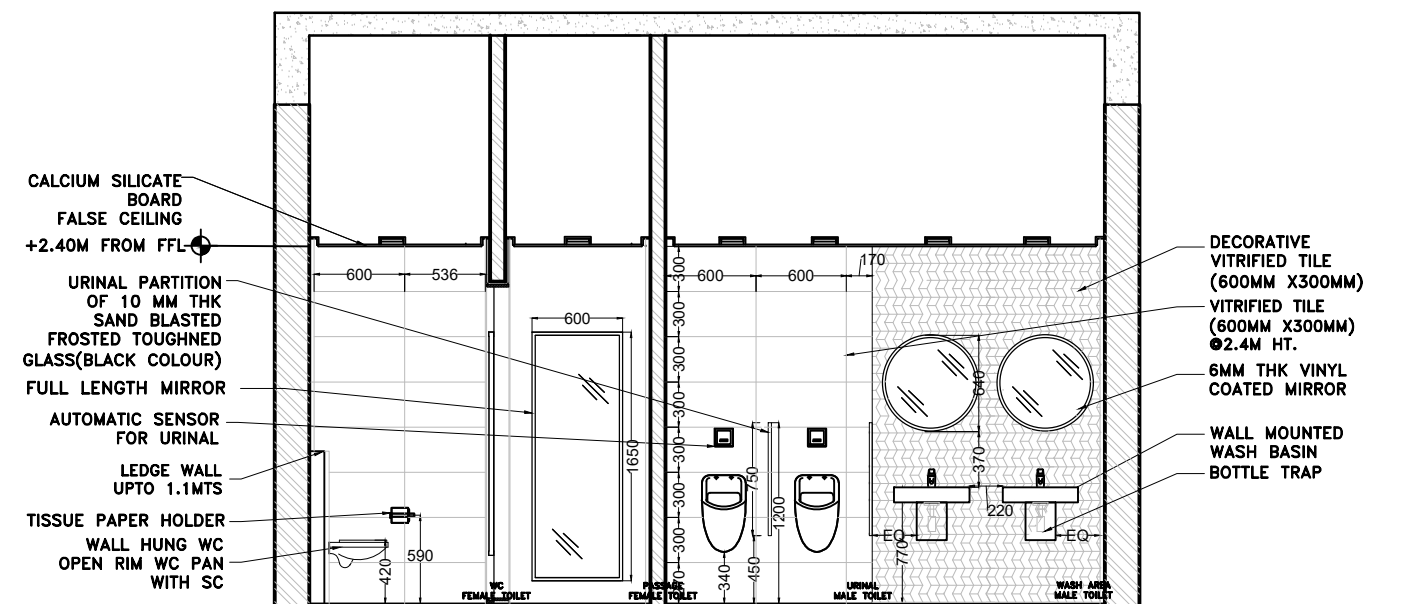

SECTION CC'
SCALE= 1:50

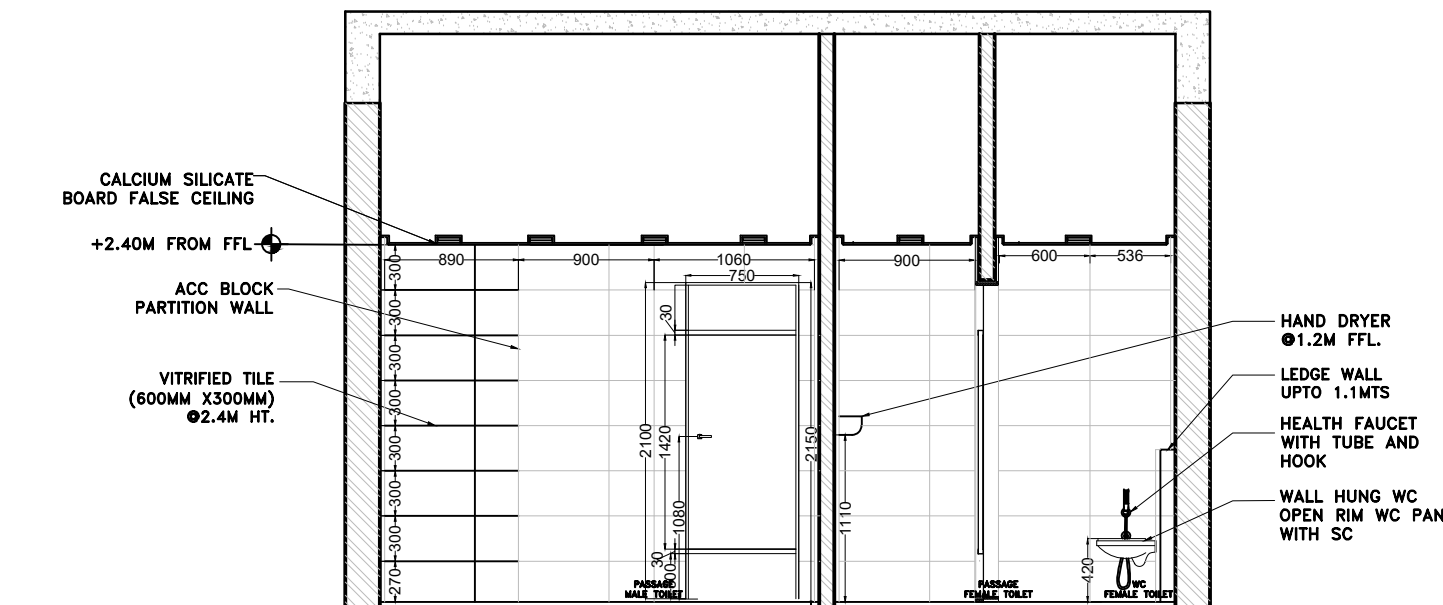

SECTION DD'
SCALE= 1:50

NOTES:


1. DRAWINGS SHALL NOT BE SCALED.
2. ALL DIMENSIONS ARE IN MM.
3. ANY DISCREPANCY IN DRAWINGS AND EXISTING CONDITIONS SHOULD BE BROUGHT TO THE NOTICE OF THE ARCHITECT PRIOR TO PROCEEDING WITH THE ITEM
4. FOR SIZE OF STRUCTURAL MEMBERS REFER STRUCTURAL ENGINEER'S DRAWINGS.
5. ALL DOOR & WINDOW DIMENSIONS LISTED IN SCHEDULES MUST BE VERIFIED WITH SITE CONDITIONS BEFORE FABRICATION.
6. ALL DOOR AND WINDOW DIMENSIONS ARE MASONARY DIMENSIONS
7. CORELATE STRUCTURAL & ARCHITECT'S DWGS. AND GET BACK TO ARCHITECT WITH DISCREPANCIES IF ANY.

una

2	12.08.22	TENDER DRAWING
No.	DATE	ISSUE/ REVISION
I I T BOMBAY: VANVIHAR GUEST HOUSE POWAI, MUMBAI - 400 076, INDIA		
UPENDRA NAYAK & ASSOCIATES ARCHITECTS. INTERIOR DESIGNERS 1, SULBHA NIWAS. DILIP GUPTA MARG. MAHIM. MUMBAI 400016 TEL: 24458473 FAX:24446223		
DATE:21.02.2022	SCALE:AS NOTED	DRAWN BY:HR
CHECKED BY:AB		


A13

ARCHITECTURAL DETAIL DRAWINGS- FIRST FLOOR TENDER DRAWINGS

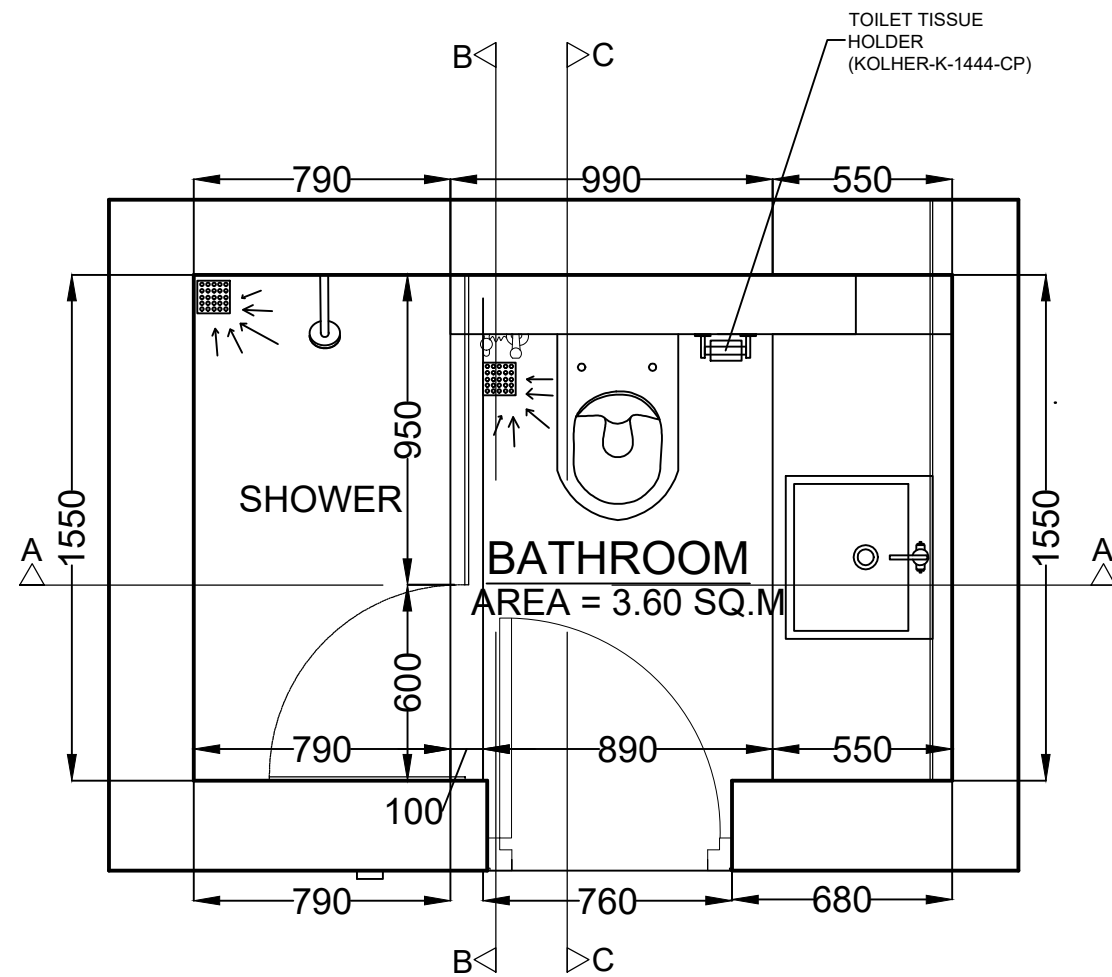

DADO TILE DETAIL		
SIZE	SIZE	TYPE
600MM X300MM	VITRIFIED TILES	DT1
AS PER DESIGN	GLASS MOSAIC	DT2


BATHROOM PLAN
SCALE=1:30


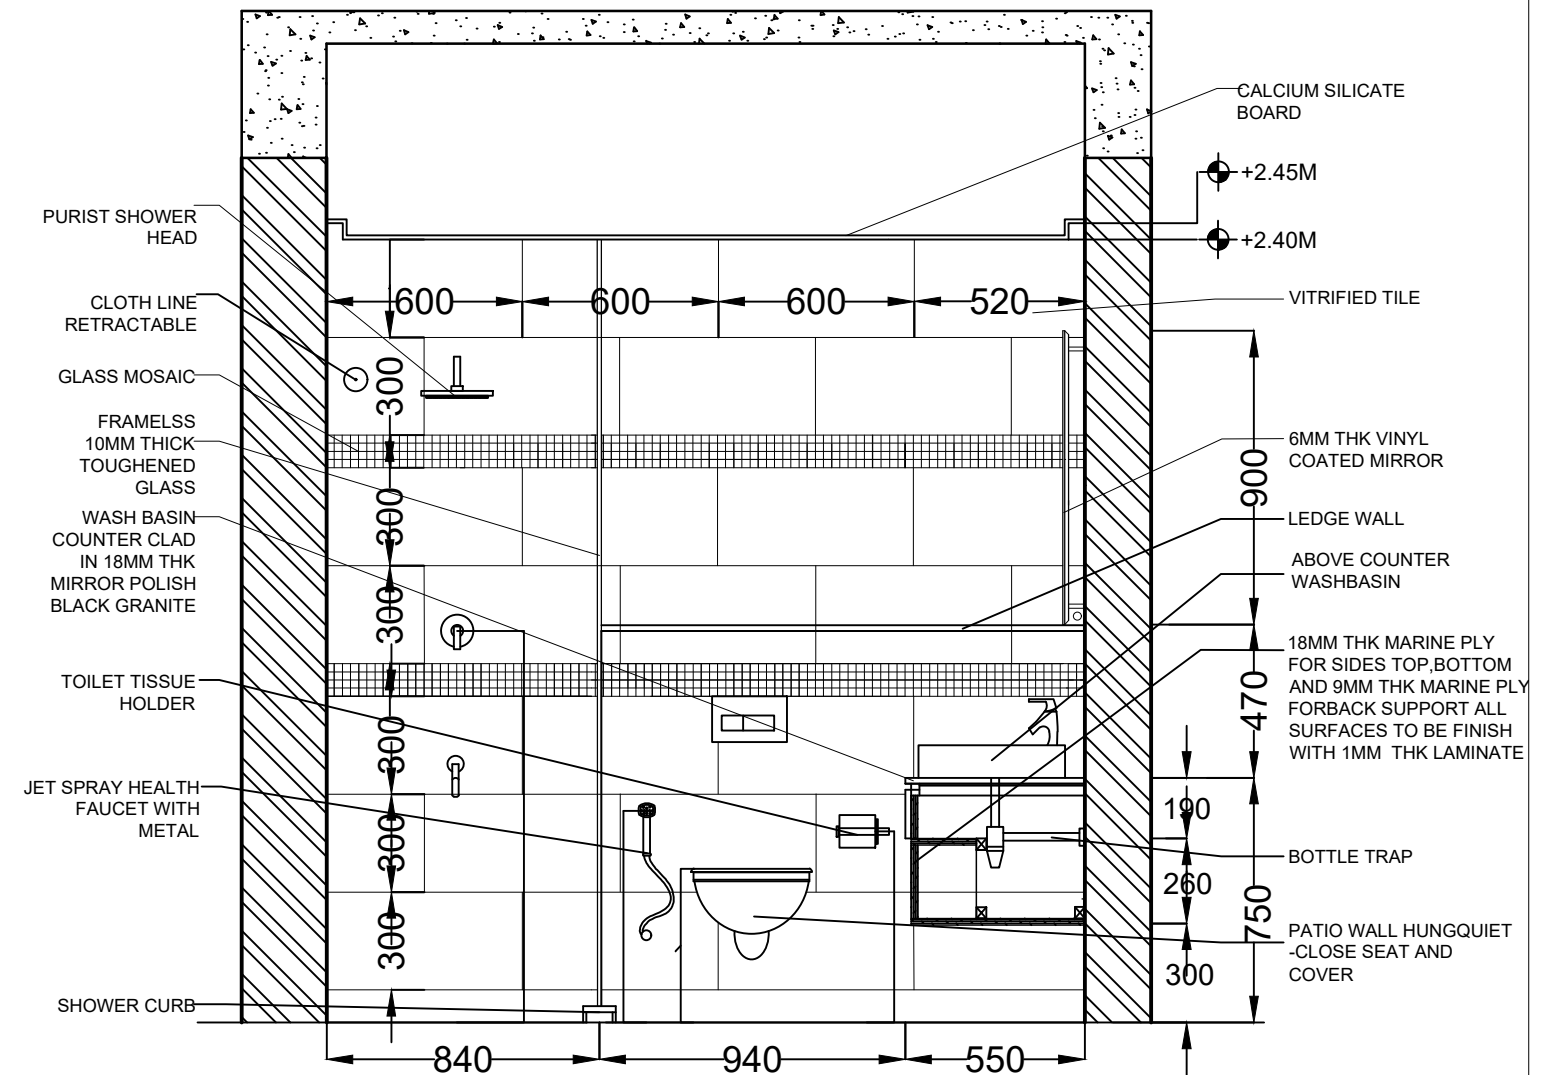


SECTION AA'
SCALE=1:30

NOTES:

- DRAWINGS SHALL NOT BE SCALED.
- ALL DIMENSIONS ARE IN MM.
- ANY DISCREPANCY IN DRAWINGS AND EXISTING CONDITIONS SHOULD BE BROUGHT TO THE NOTICE OF THE ARCHITECT PRIOR TO PROCEEDING WITH THE ITEM
- FOR SIZE OF STRUCTURAL MEMBERS REFER STRUCTURAL ENGINEER'S DRAWINGS.
- ALL DOOR & WINDOW DIMENSIONS LISTED IN SCHEDULES MUST BE VERIFIED WITH SITE CONDITIONS BEFORE FABRICATION.
- ALL DOOR AND WINDOW DIMENSIONS ARE MASONARY DIMENSIONS
- CORELATE STRUCTURAL & ARCHITECT'S DWGS. AND GET BACK TO ARCHITECT WITH DISCREPANCIES IF ANY.

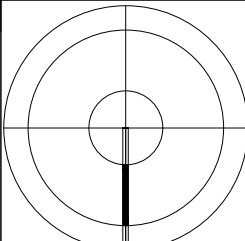una			
	1	12.08.2022	ISSUE FOR TENDER PURPOSE
	No.	DATE	ISSUE/ REVISION
	I I T BOMBAY: VANVIHAR GUEST HOUSE		
	POWAI, MUMBAI - 400 076, INDIA		
	UPENDRA NAYAK & ASSOCIATES		A5a
	ARCHITECTS. INTERIOR DESIGNERS		
	1, SULBHA NIWAS. DILIP GUPTA MARG. MAHIM. MUMBAI 400016		
	TEL: 24458473 FAX:24446223		
	DATE: 21.02.2022	SCALE: AS NOTED	DRAWN BY: HR
		CHECKED BY: AB	

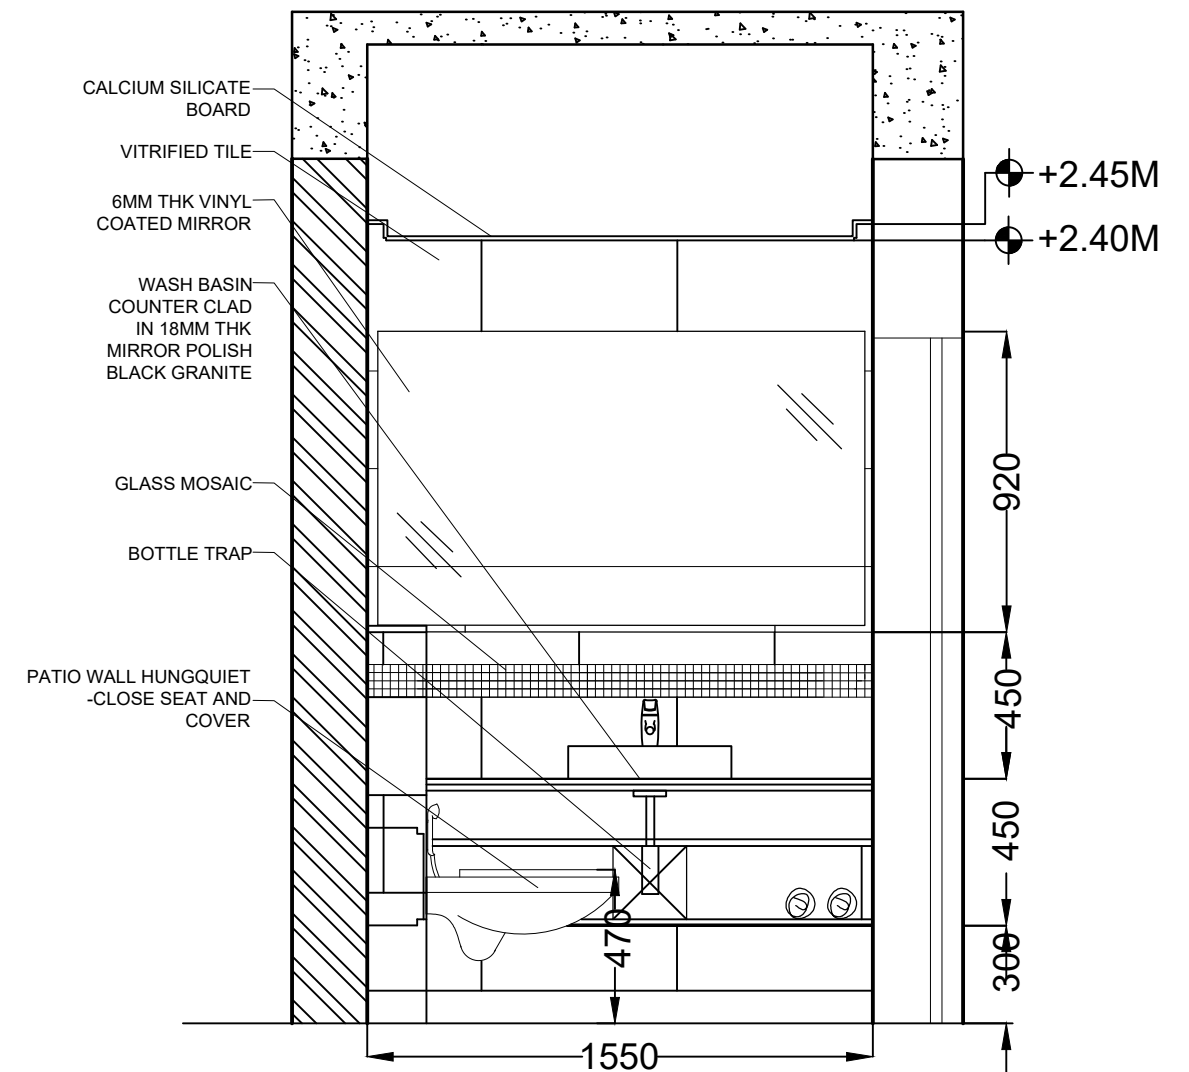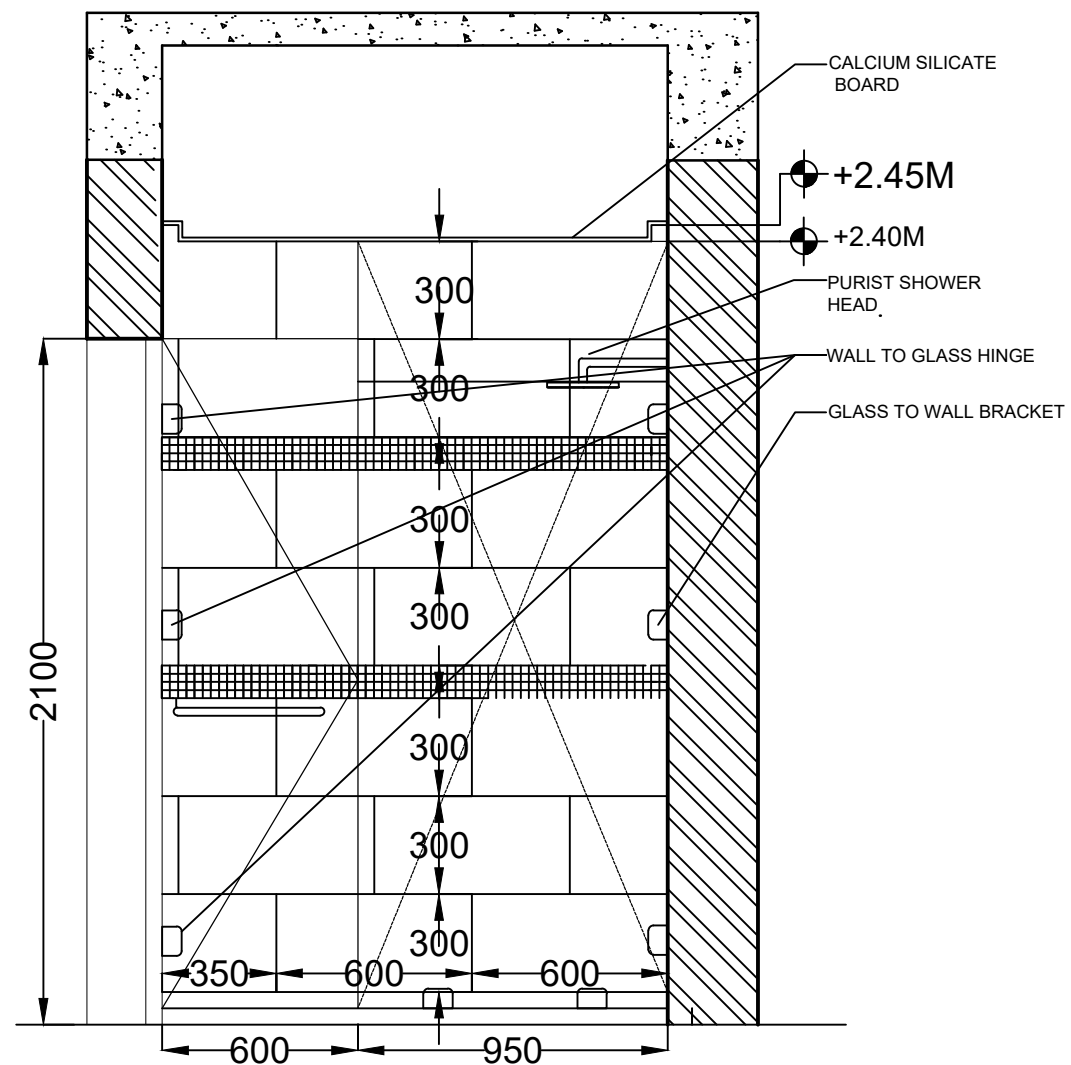


SECTION BB'
SCALE=1:25


SECTION CC'
SCALE=1:25

NOTES:


1. DRAWINGS SHALL NOT BE SCALED.
2. ALL DIMENSIONS ARE IN MM.
3. ANY DISCREPANCY IN DRAWINGS AND EXISTING CONDITIONS SHOULD BE BROUGHT TO THE NOTICE OF THE ARCHITECT PRIOR TO PROCEEDING WITH THE ITEM
4. FOR SIZE OF STRUCTURAL MEMBERS REFER STRUCTURAL ENGINEER'S DRAWINGS.
5. ALL DOOR & WINDOW DIMENSIONS LISTED IN SCHEDULES MUST BE VERIFIED WITH SITE CONDITIONS BEFORE FABRICATION.
6. ALL DOOR AND WINDOW DIMENSIONS ARE MASONARY DIMENSIONS
7. CORRELATE STRUCTURAL & ARCHITECT'S DWGS. AND GET BACK TO ARCHITECT WITH DISCREPANCIES IF ANY.

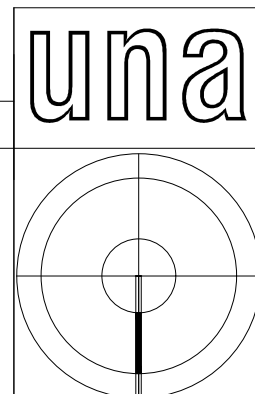


1	12.08.2022	ISSUE FOR TENDER PURPOSE
No.	DATE	ISSUE/ REVISION
<u>I I T BOMBAY: VANVIHAR GUEST HOUSE</u> POWAI, MUMBAI - 400 076, INDIA		
UPENDRA NAYAK & ASSOCIATES ARCHITECTS. INTERIOR DESIGNERS 1, SULBHA NIWAS. DILIP GUPTA MARG. MAHIM. MUMBAI 400016 TEL: 24458473 FAX:24446223		A5b
DATE: 21.02.2022	SCALE: AS NOTED	
DRAWN BY: HR		CHECKED BY: AB

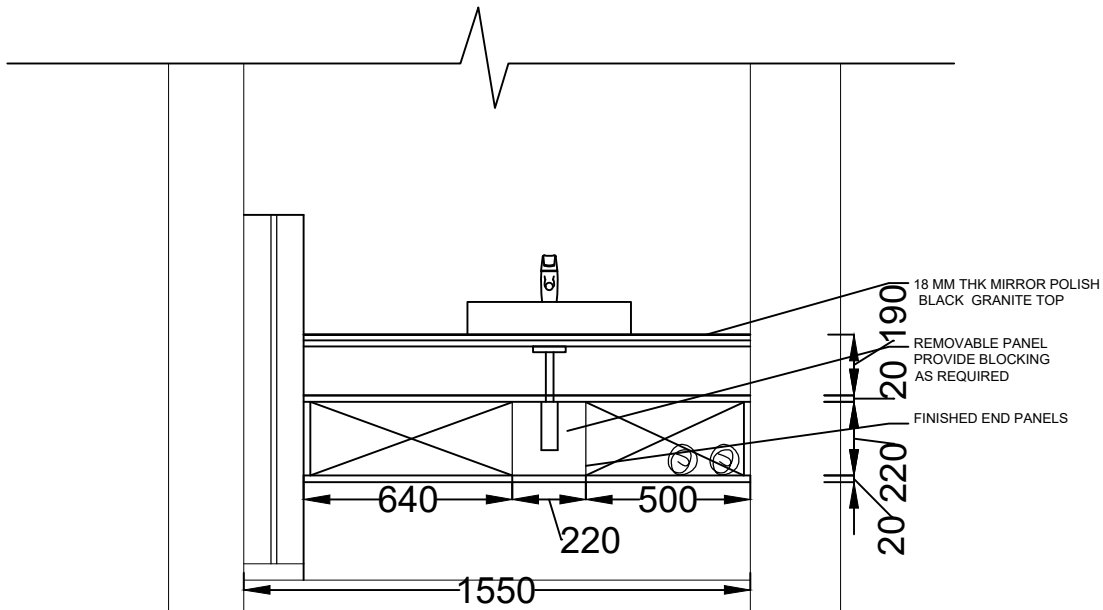


FRONT ELEVATION
SCALE=1:25

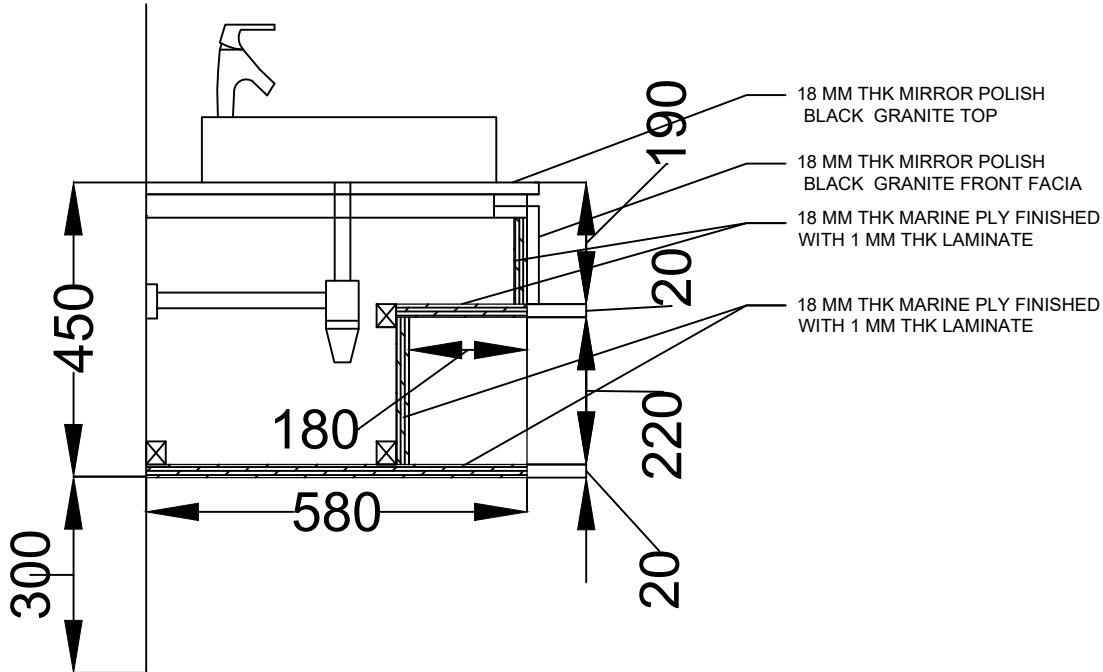

SECTION BB'
SCALE=1:15

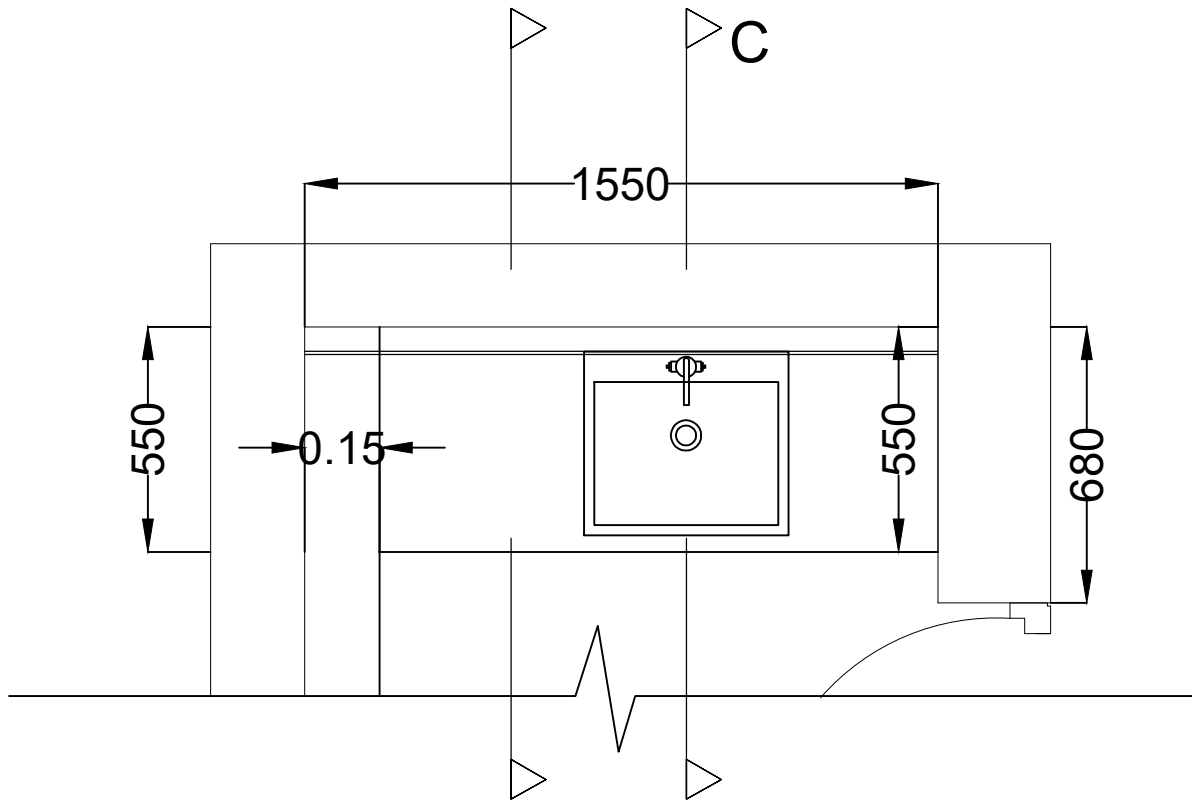

PLAN OF WASH BASIN COUNTER
SCALE=1:20

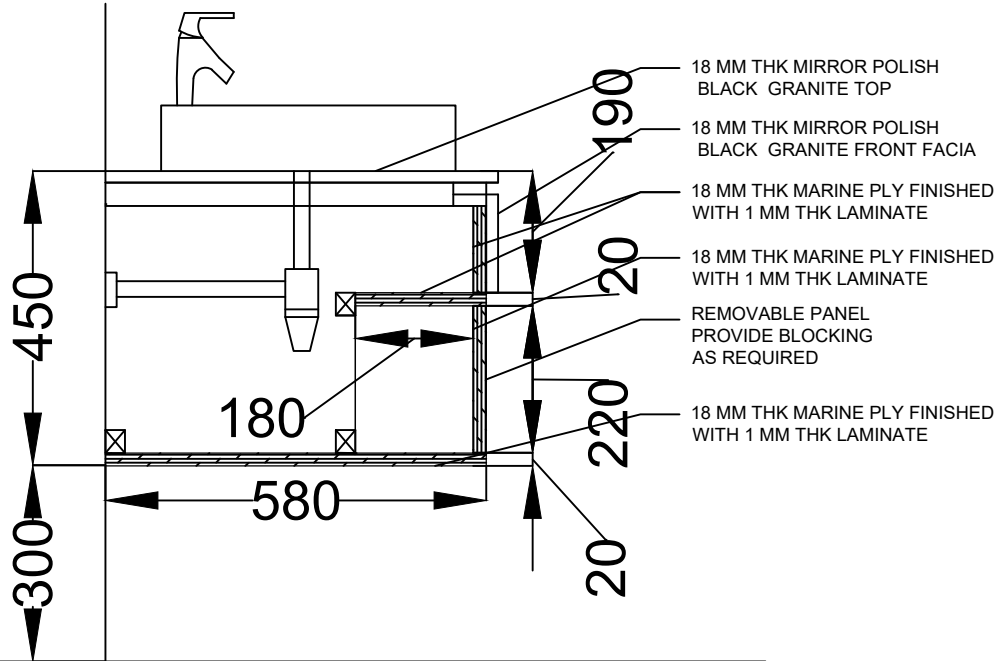


SECTION CC'
SCALE=1:15

NOTES:

1. DRAWINGS SHALL NOT BE SCALED.
2. ALL DIMENSIONS ARE IN MM.
3. ANY DISCREPANCY IN DRAWINGS AND EXISTING CONDITIONS SHOULD BE BROUGHT TO THE NOTICE OF THE ARCHITECT PRIOR TO PROCEEDING WITH THE ITEM
4. FOR SIZE OF STRUCTURAL MEMBERS REFER STRUCTURAL ENGINEER'S DRAWINGS.
5. ALL DOOR & WINDOW DIMENSIONS LISTED IN SCHEDULES MUST BE VERIFIED WITH SITE CONDITIONS BEFORE FABRICATION.
6. ALL DOOR AND WINDOW DIMENSIONS ARE MASONARY DIMENSIONS
7. CORELATE STRUCTURAL & ARCHITECT'S DWGS. AND GET BACK TO ARCHITECT WITH DISCREPANCIES IF ANY.

una

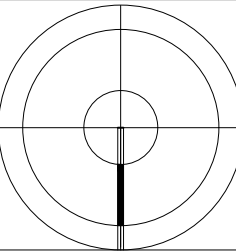

1 12.08.2022 ISSUE FOR TENDER PURPOSE





No. DATE ISSUE/ REVISION

I I T BOMBAY: VANVIHAR GUEST HOUSE
POWAI, MUMBAI - 400 076, INDIA

UPENDRA NAYAK & ASSOCIATES
ARCHITECTS. INTERIOR DESIGNERS
1, SULBHA NIWAS. DILIP GUPTA MARG. MAHIM. MUMBAI 400016
TEL: 24458473 FAX:24446223


DATE: 21.02.2022 SCALE: AS NOTED DRAWN BY: HR CHECKED BY: AB


A5c

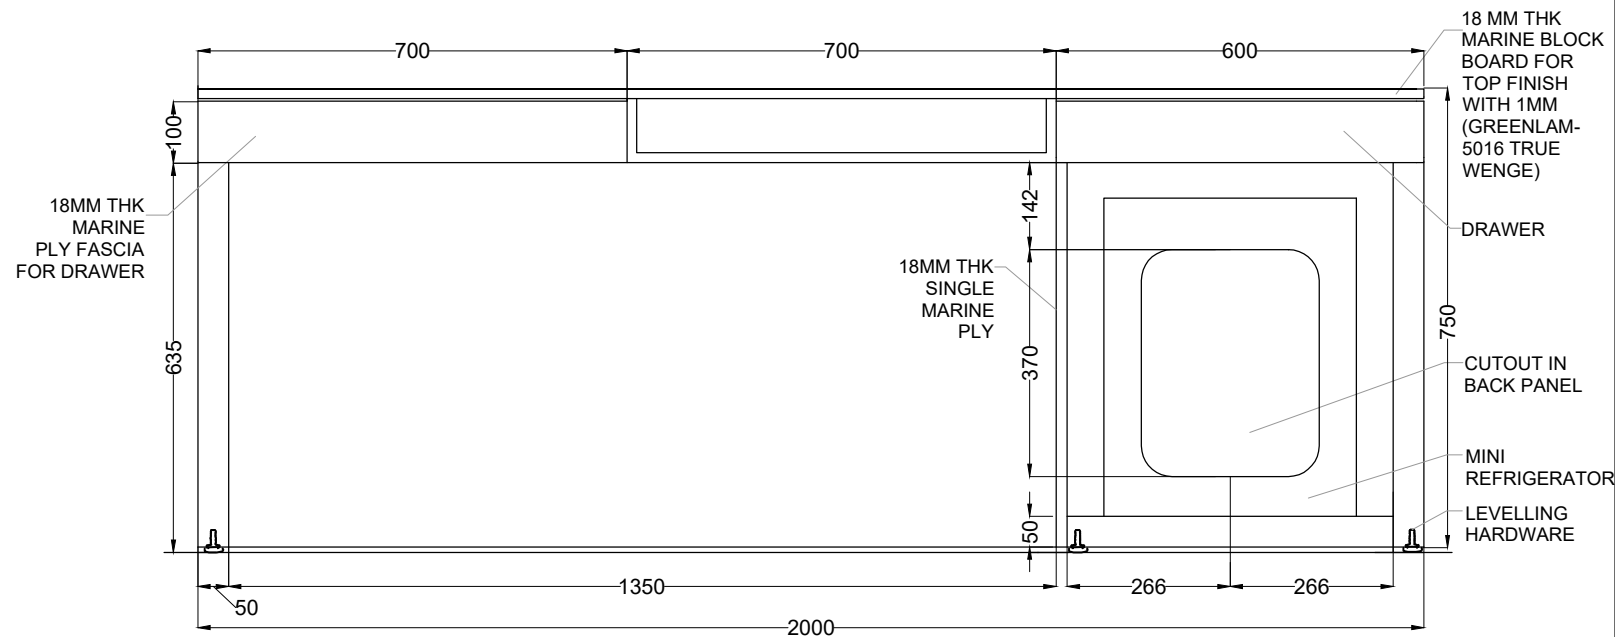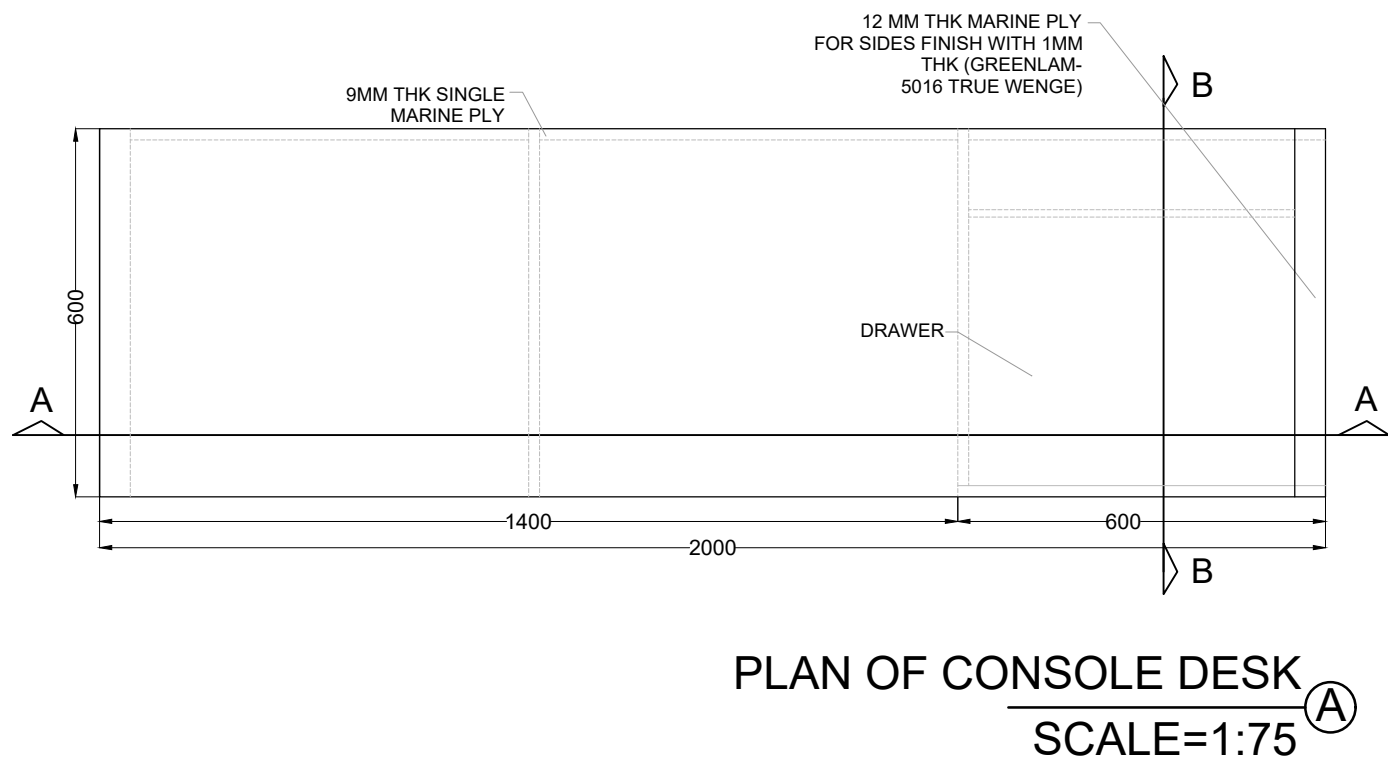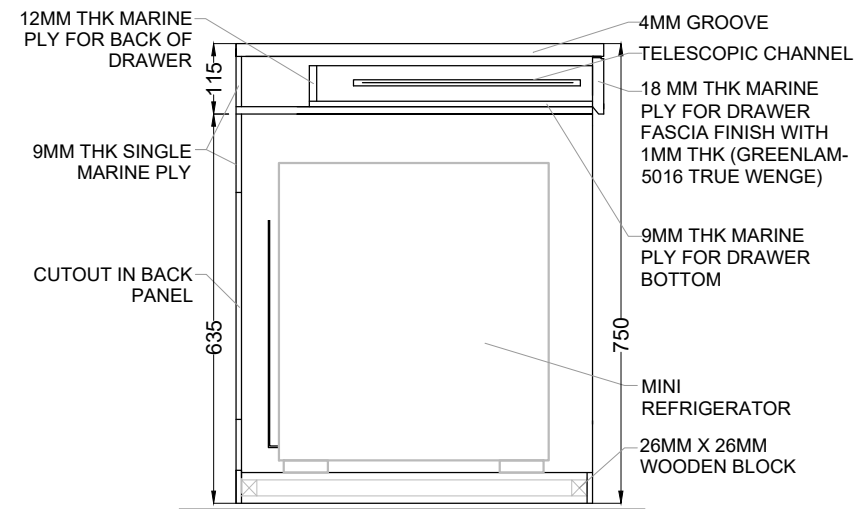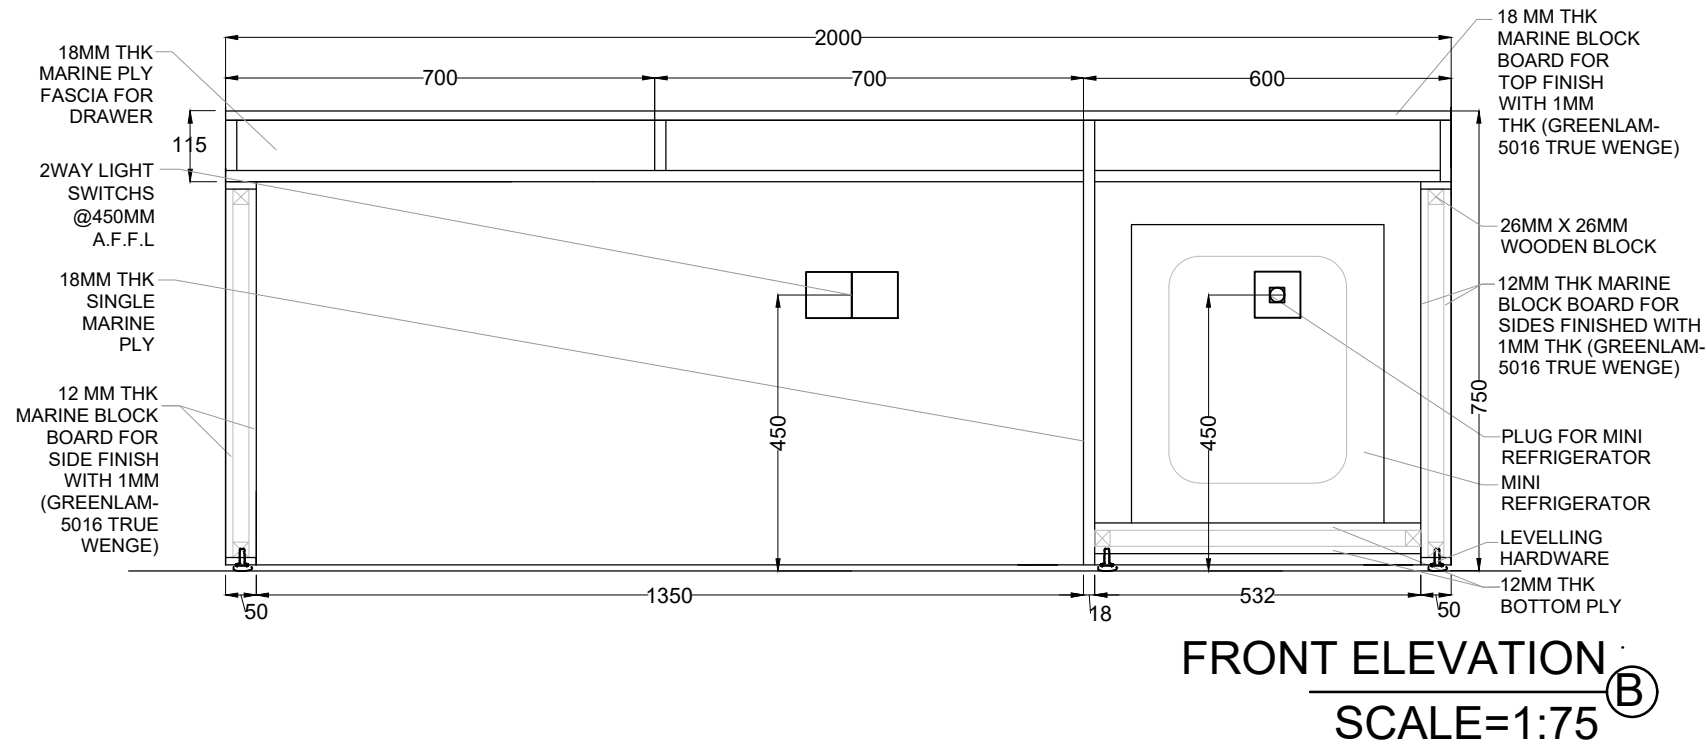


NOTES:

1. DRAWINGS SHALL NOT BE SCALED.
2. ALL DIMENSIONS ARE IN MM.
3. ANY DISCREPANCY IN DRAWINGS AND EXISTING CONDITIONS SHOULD BE BROUGHT TO THE NOTICE OF THE ARCHITECT PRIOR TO PROCEEDING WITH THE ITEM
4. FOR SIZE OF STRUCTURAL MEMBERS REFER STRUCTURAL ENGINEER'S DRAWINGS.
5. ALL DOOR & WINDOW DIMENSIONS LISTED IN SCHEDULES MUST BE VERIFIED WITH SITE CONDITIONS BEFORE FABRICATION.
6. ALL DOOR AND WINDOW DIMENSIONS ARE MASONARY DIMENSIONS
7. CORELATE STRUCTURAL & ARCHITECT'S DWGS. AND GET BACK TO ARCHITECT WITH DISCREPANCIES IF ANY.

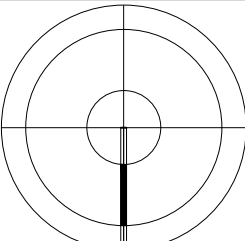
una	1	12.08.2022	ISSUE FOR TENDER PURPOSE	
	No.	DATE	ISSUE/ REVISION	
	<u>I I T BOMBAY: VANVIHAR GUEST HOUSE</u>			
	POWAI, MUMBAI - 400 076, INDIA			
	UPENDRA NAYAK & ASSOCIATES			
	ARCHITECTS. INTERIOR DESIGNERS			
	1, SULBHA NIWAS. DILIP GUPTA MARG. MAHIM. MUMBAI 400016 TEL: 24458473 FAX:24446223			
DATE: 21.02.2022		SCALE:AS NOTED	DRAWN BY:HR	CHECKED BY:AB
A6				

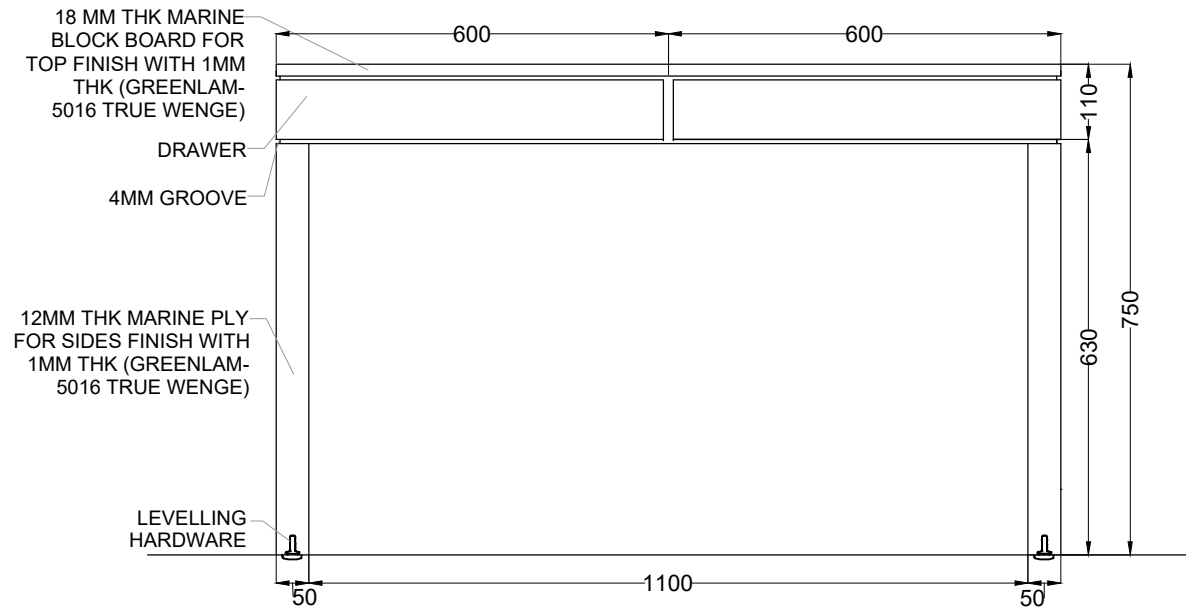


FRONT ELEVATION
SCALE=1:10 [ⓑ]

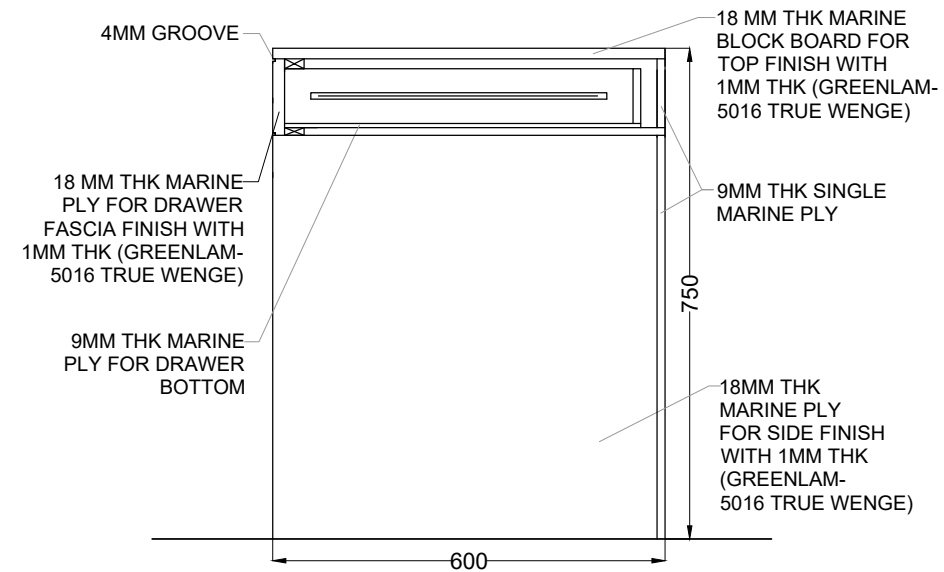

SECTION BB'
SCALE=1:10 [ⓒ]

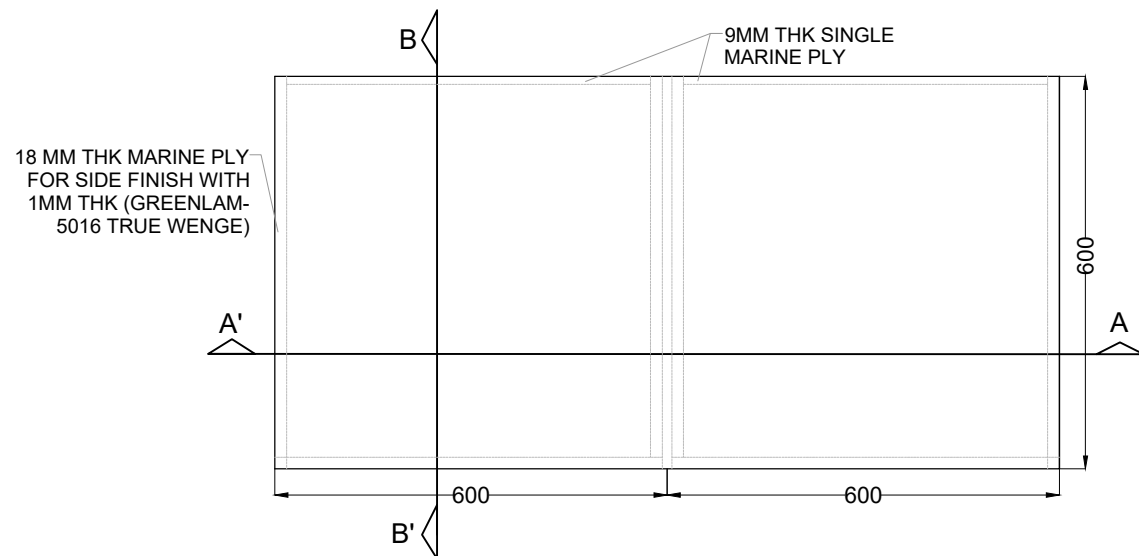

PLAN OF SIDE TABLE
SCALE=1:10 [Ⓐ]

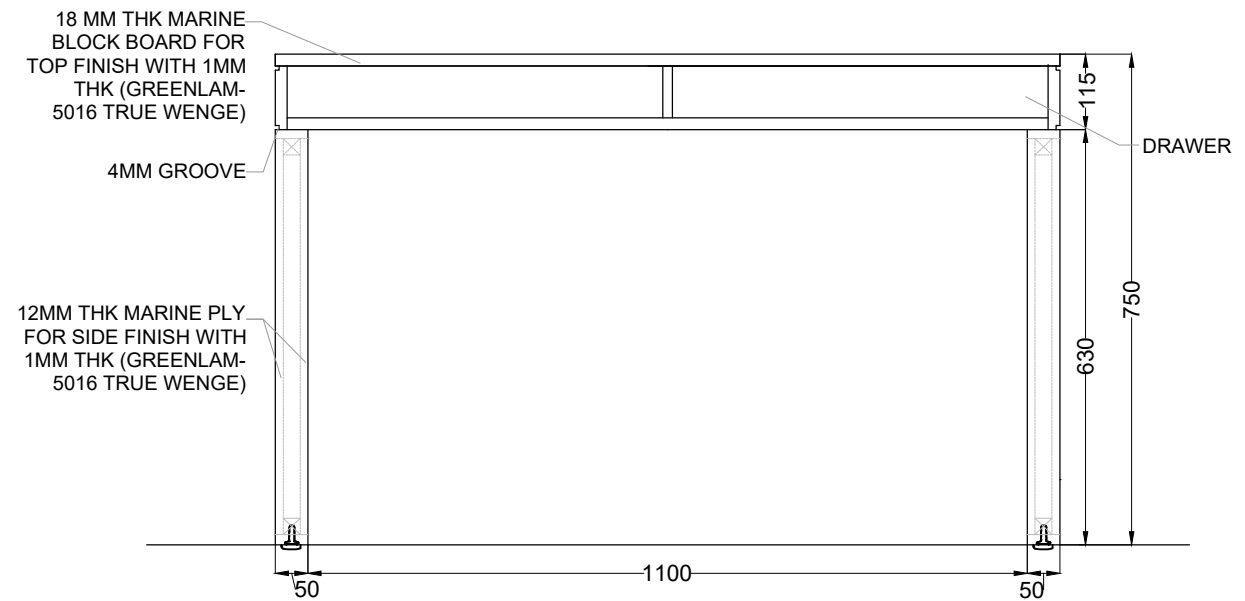


SECTION AA'
SCALE=1:10 [Ⓓ]

NOTES:

- DRAWINGS SHALL NOT BE SCALED.
- ALL DIMENSIONS ARE IN MM.
- ANY DISCREPANCY IN DRAWINGS AND EXISTING CONDITIONS SHOULD BE BROUGHT TO THE NOTICE OF THE ARCHITECT PRIOR TO PROCEEDING WITH THE ITEM
- FOR SIZE OF STRUCTURAL MEMBERS REFER STRUCTURAL ENGINEER'S DRAWINGS.
- ALL DOOR & WINDOW DIMENSIONS LISTED IN SCHEDULES MUST BE VERIFIED WITH SITE CONDITIONS BEFORE FABRICATION.
- ALL DOOR AND WINDOW DIMENSIONS ARE MASONARY DIMENSIONS
- CORELATE STRUCTURAL & ARCHITECT'S DWGS. AND GET BACK TO ARCHITECT WITH DISCREPANCIES IF ANY.


una			
	1	12.08.2022	ISSUE FOR TENDER PURPOSE
	No.	DATE	ISSUE/ REVISION
	I I T BOMBAY: VANVIHAR GUEST HOUSE		
	POWAI, MUMBAI - 400 076, INDIA		
	UPENDRA NAYAK & ASSOCIATES		
	ARCHITECTS. INTERIOR DESIGNERS		
	1, SULBHA NIWAS. DILIP GUPTA MARG. MAHIM. MUMBAI 400016		
	TEL: 24458473 FAX:24446223		
	DATE: 21.02.2022	SCALE: AS NOTED	DRAWN BY: HR
		CHECKED BY: AB	

A7

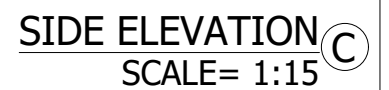

1. DRAWINGS SHALL NOT BE SCALED.
2. ALL DIMENSIONS ARE IN MM.
3. ANY DISCREPANCY IN DRAWINGS AND EXISTING CONDITIONS SHOULD BE BROUGHT TO THE NOTICE OF THE ARCHITECT PRIOR TO PROCEEDING WITH THE ITEM
4. FOR SIZE OF STRUCTURAL MEMBERS REFER STRUCTURAL ENGINEER'S DRAWINGS.
5. ALL DOOR & WINDOW DIMENSIONS LISTED IN SCHEDULES MUST BE VERIFIED WITH SITE CONDITIONS BEFORE FABRICATION.
6. ALL DOOR AND WINDOW DIMENSIONS ARE MASONRY DIMENSIONS
7. CORRELATE STRUCTURAL & ARCHITECT'S DWGS. AND GET BACK TO ARCHITECT WITH DISCREPANCIES IF ANY.


una

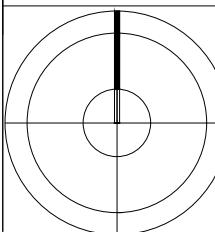



1	12.08.22	ISSUE FOR TENDER PURPOSE	
No.	DATE	ISSUE/ REVISION	
<u>I I T BOMBAY: VANVIHAR GUEST HOUSE</u> POWAI, MUMBAI - 400 076, INDIA			
UPENDRA NAYAK & ASSOCIATES ARCHITECTS. INTERIOR DESIGNERS 1, SULBHA NIWAS. DILIP GUPTA MARG. MAHIM. MUMBAI 400016 TEL: 24458473 FAX:24446223		A8	
DATE: 2012.02.2022	SCALE: AS NOTED		DRAWN BY: HR



WARDROBE DETAIL WITH SAFE

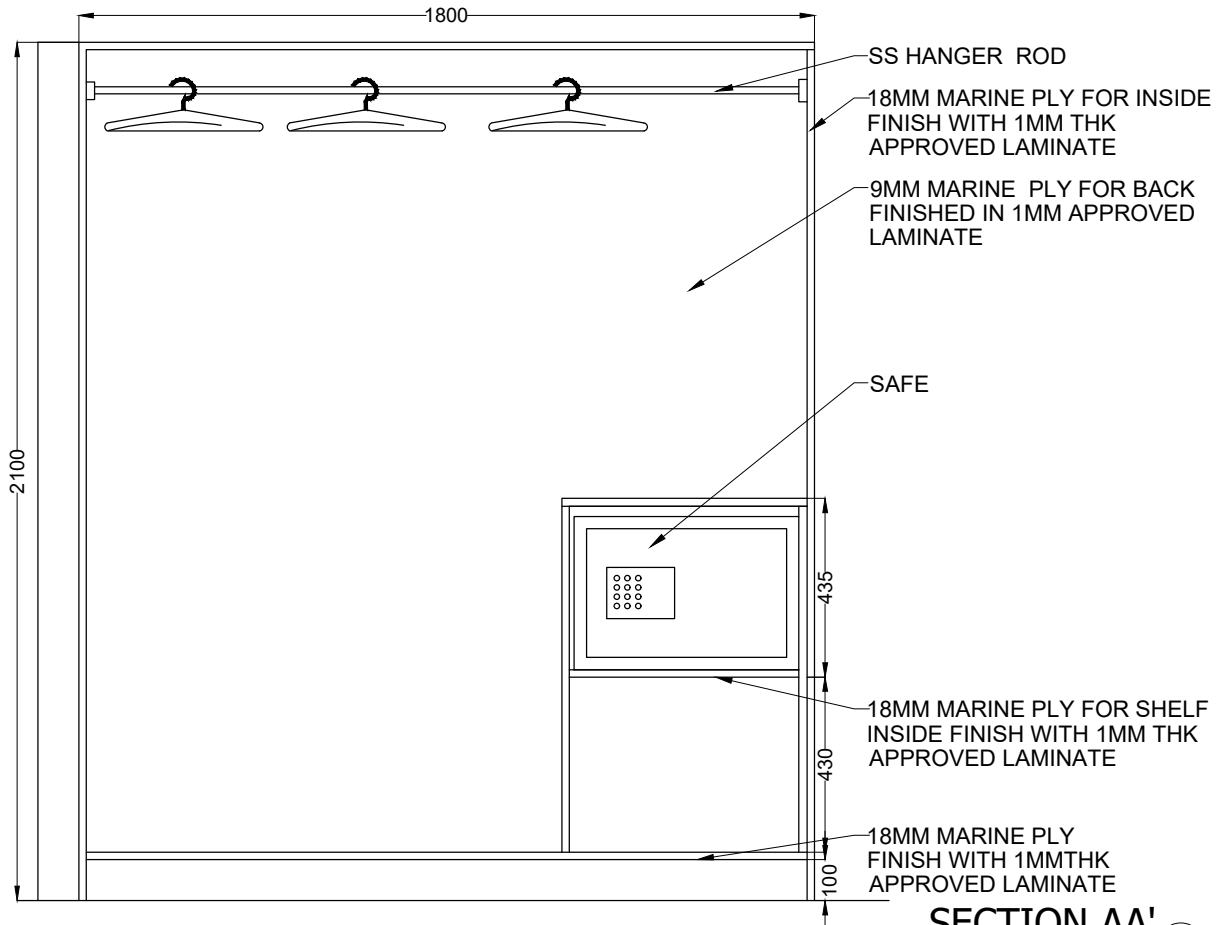

SECTION AA' ^D
SCALE= 1:20

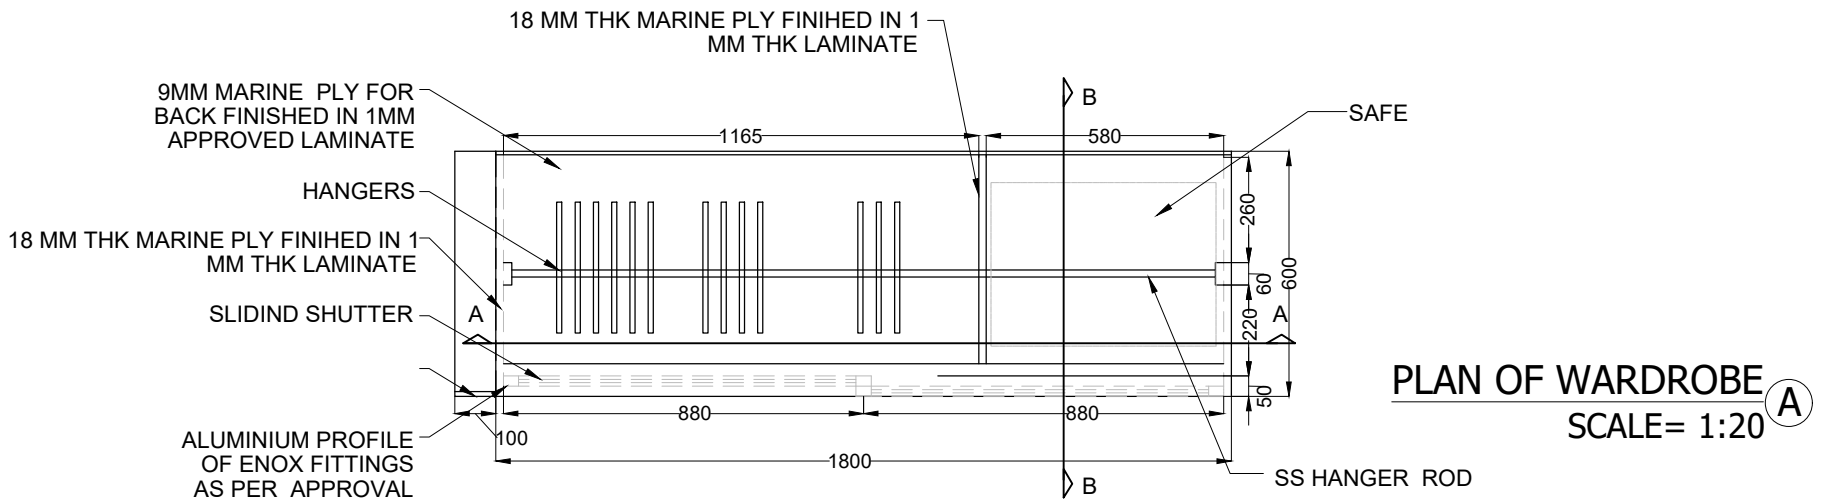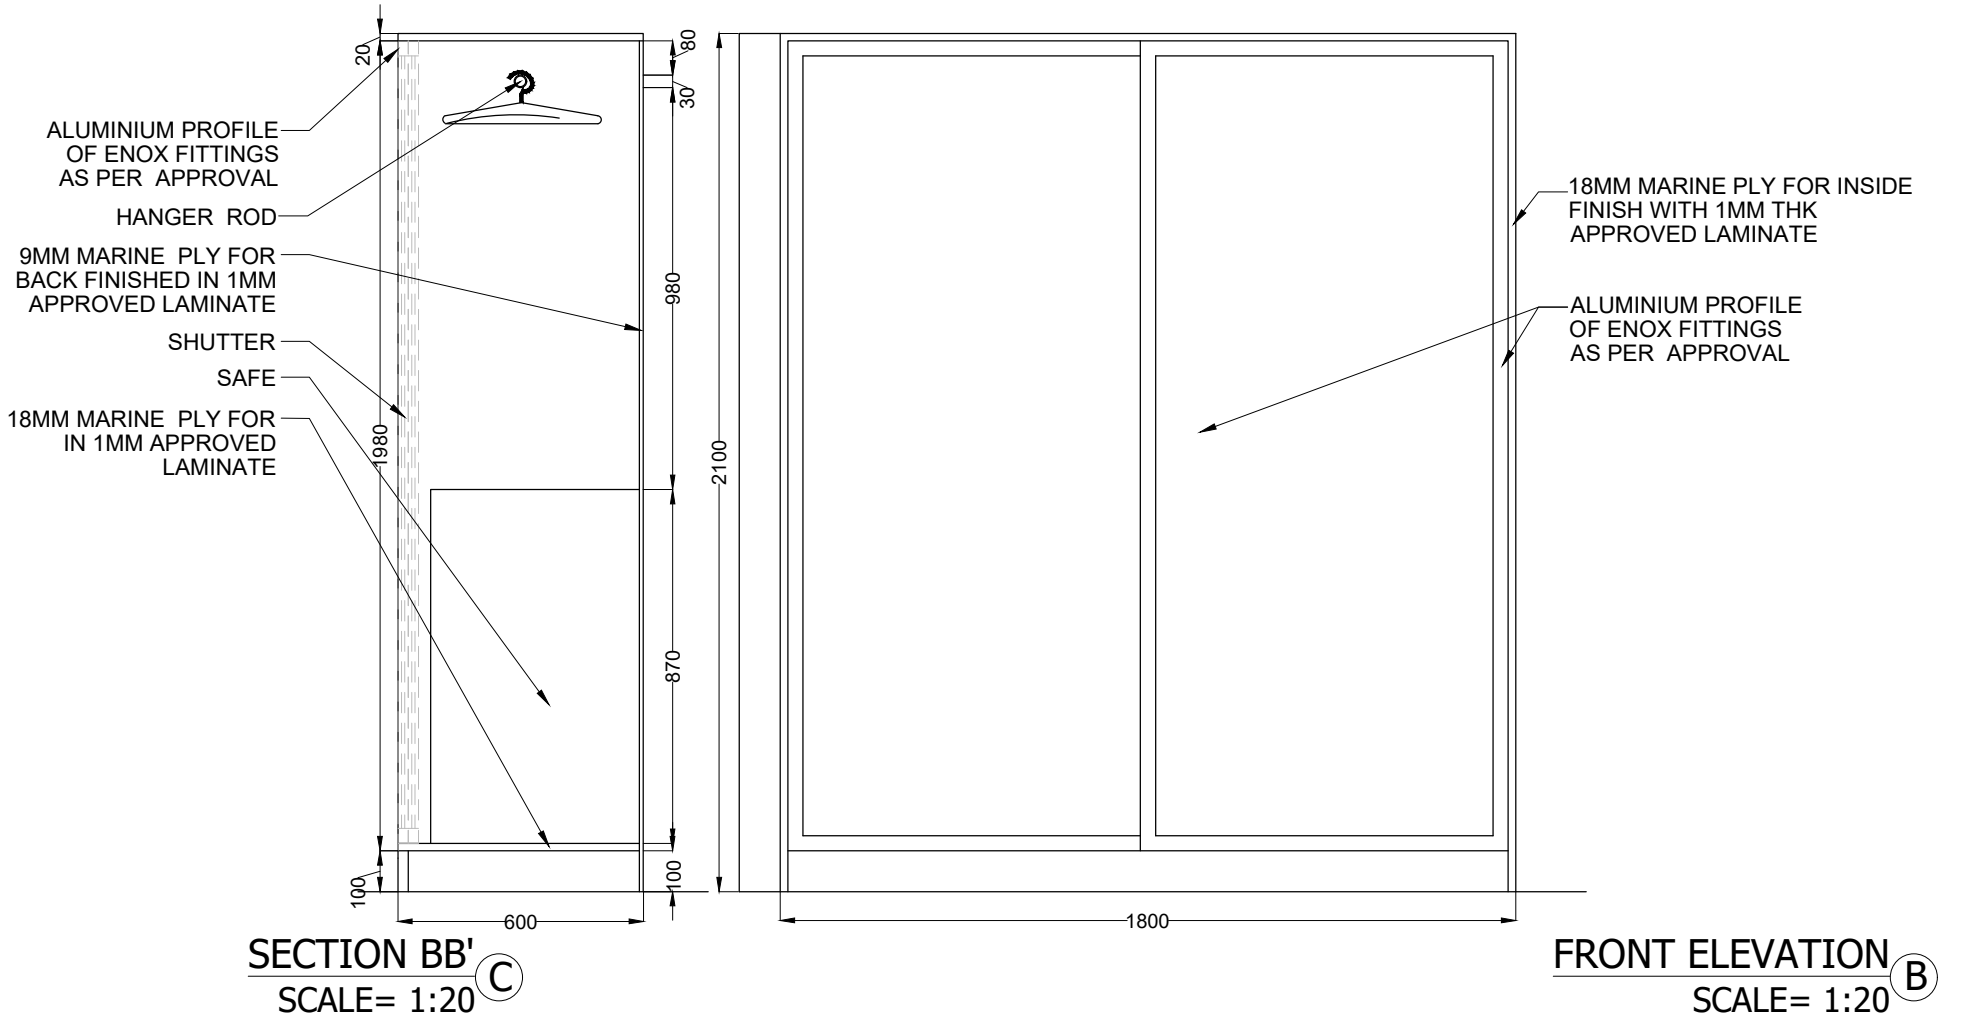

NOTES:

1. DRAWINGS SHALL NOT BE SCALED.

2. ALL DIMENSIONS ARE IN MM.

3. ANY DISCREPANCY IN DRAWINGS AND EXISTING CONDITIONS SHOULD BE BROUGHT TO THE NOTICE OF THE ARCHITECT PRIOR TO PROCEEDING WITH THE ITEM


4. FOR SIZE OF STRUCTURAL MEMBERS REFER STRUCTURAL ENGINEER'S DRAWINGS.

5. ALL DOOR & WINDOW DIMENSIONS LISTED IN SCHEDULES MUST BE VERIFIED WITH SITE CONDITIONS BEFORE FABRICATION.

6. ALL DOOR AND WINDOW DIMENSIONS ARE MASONARY DIMENSIONS

7.CORELATE STRUCTURAL & ARCHITECT'S DWGS. AND GET BACK TO ARCHITECT WITH DISCREPANCIES IF ANY.

una

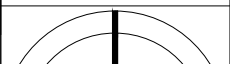

I I T BOMBAY: VANVIHAR GUEST HOUSE

POWAI, MUMBAI - 400 076, INDIA

UPENDRA NAYAK & ASSOCIATES

ARCHITECTS. INTERIOR DESIGNERS

1, SULBHA NIWAS, DILIP GUPTA MARG. MAHIM. MUMBAI 400016

TEL: 24458473 FAX:24446223


DATE: 1.02.2022

SCALE: AS NOTED


DRAWN BY: HR

CHECKED BY: AB


A9

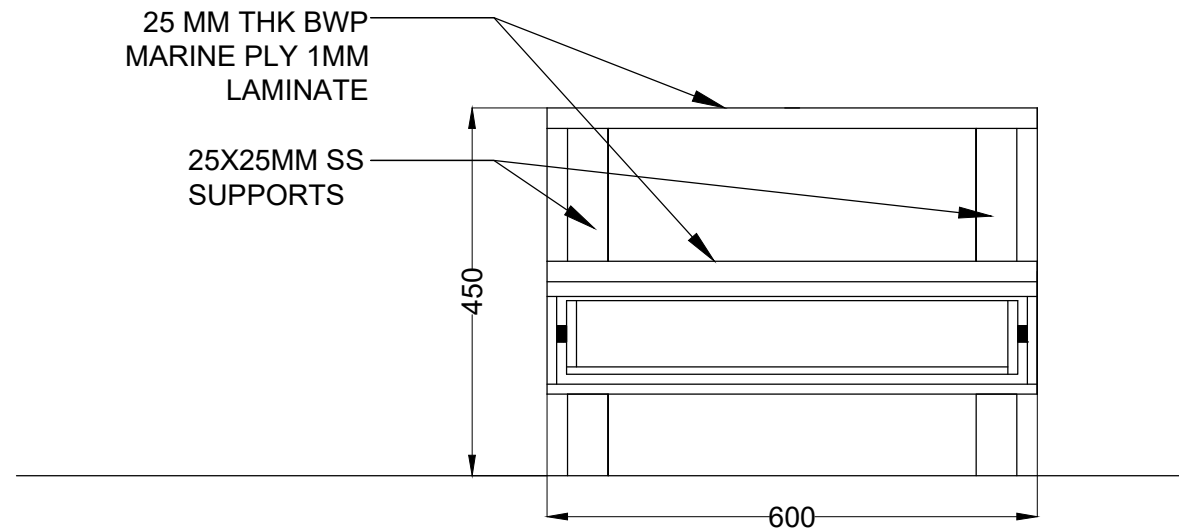


SECTION A-A'
SCALE= 1:10 (B)

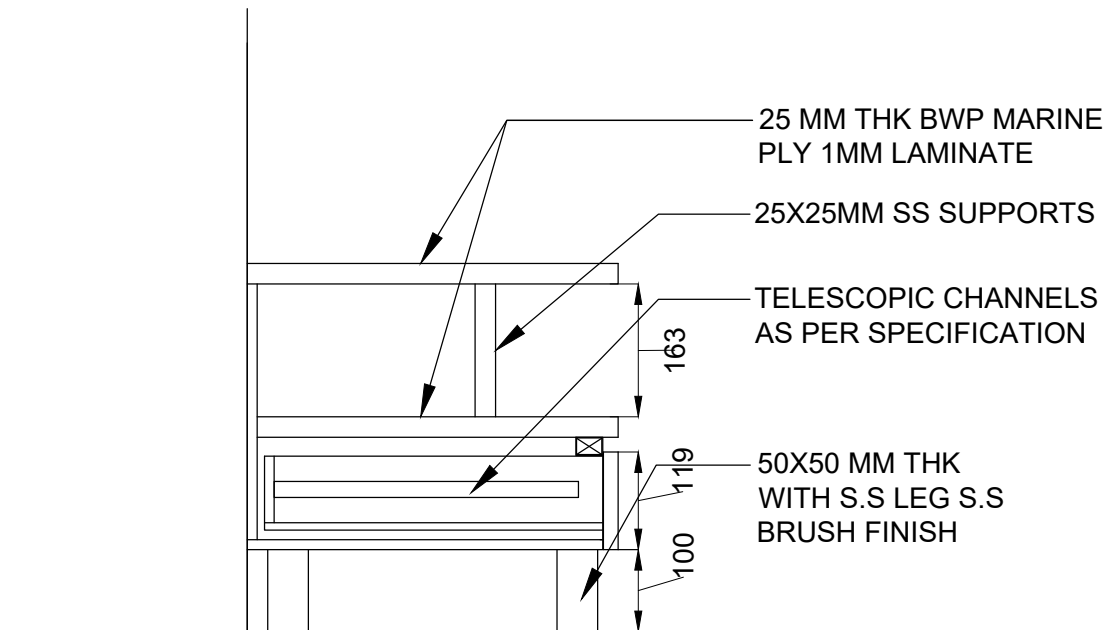

SECTION B-B'
SCALE= 1:10 (C)

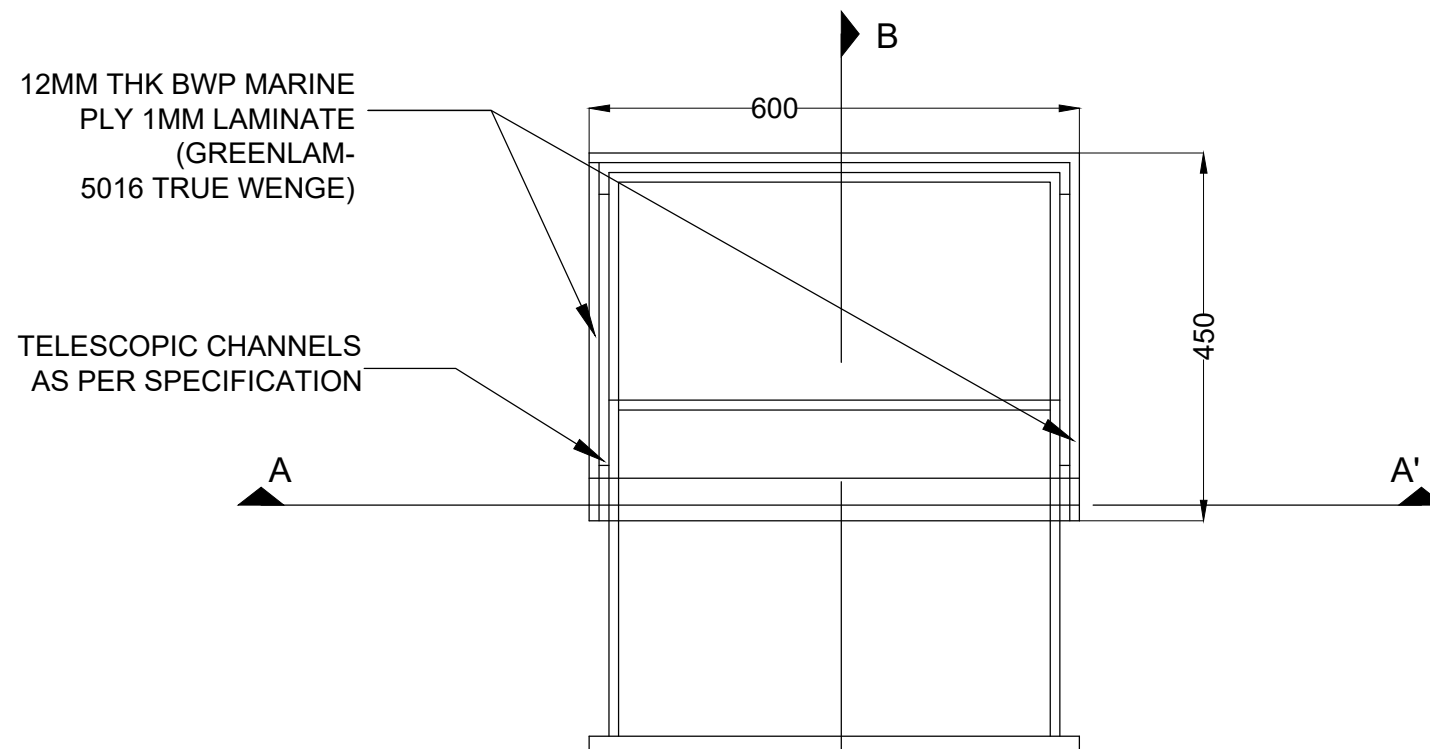


PLAN OF SIDE TABLE
SCALE=1:10 (A)

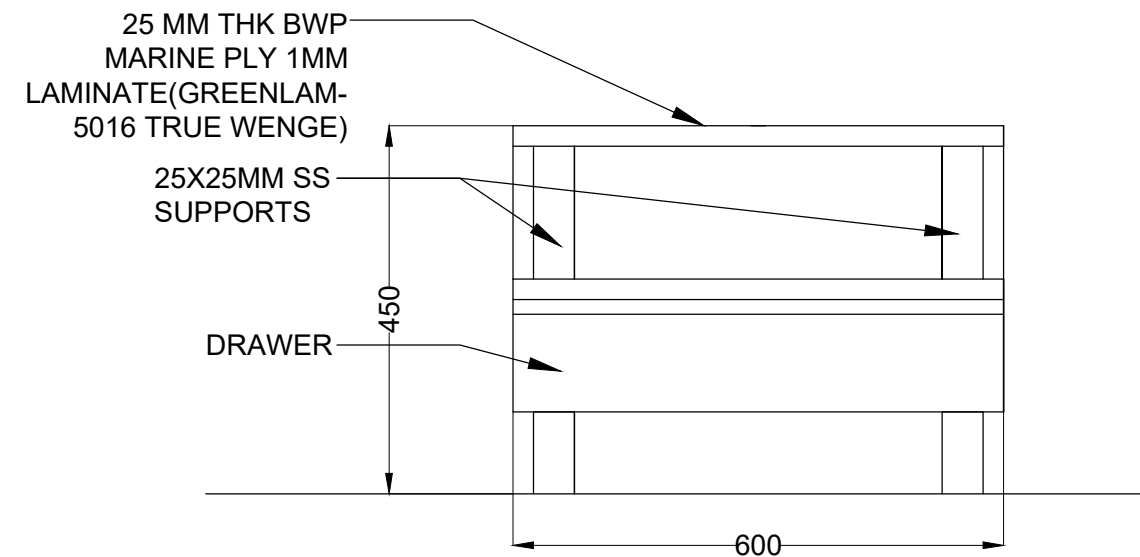


FRONT ELEVATION
SCALE= 1:10 (D)

NOTES:


1. DRAWINGS SHALL NOT BE SCALED.
2. ALL DIMENSIONS ARE IN MM.
3. ANY DISCREPANCY IN DRAWINGS AND EXISTING CONDITIONS SHOULD BE BROUGHT TO THE NOTICE OF THE ARCHITECT PRIOR TO PROCEEDING WITH THE ITEM
4. FOR SIZE OF STRUCTURAL MEMBERS REFER STRUCTURAL ENGINEER'S DRAWINGS.
5. ALL DOOR & WINDOW DIMENSIONS LISTED IN SCHEDULES MUST BE VERIFIED WITH SITE CONDITIONS BEFORE FABRICATION.
6. ALL DOOR AND WINDOW DIMENSIONS ARE MASONARY DIMENSIONS
7. CORELATE STRUCTURAL & ARCHITECT'S DWGS. AND GET BACK TO ARCHITECT WITH DISCREPANCIES IF ANY.

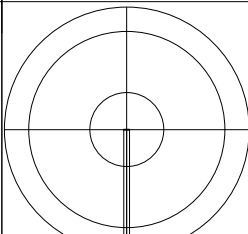
una			
	1	12.08.2022	ISSUE FOR TENDER PURPOSE
	No.	DATE	ISSUE/ REVISION
	I I T BOMBAY: VANVIHAR GUEST HOUSE		
	POWAI, MUMBAI - 400 076, INDIA		
	UPENDRA NAYAK & ASSOCIATES		
	ARCHITECTS. INTERIOR DESIGNERS		
	1, SULBHA NIWAS. DILIP GUPTA MARG. MAHIM. MUMBAI 400016 TEL: 24458473 FAX:24446223		
	DATE: 21.02.2022	SCALE: AS NOTED	DRAWN BY:HR
			CHECKED BY:AN
			A10

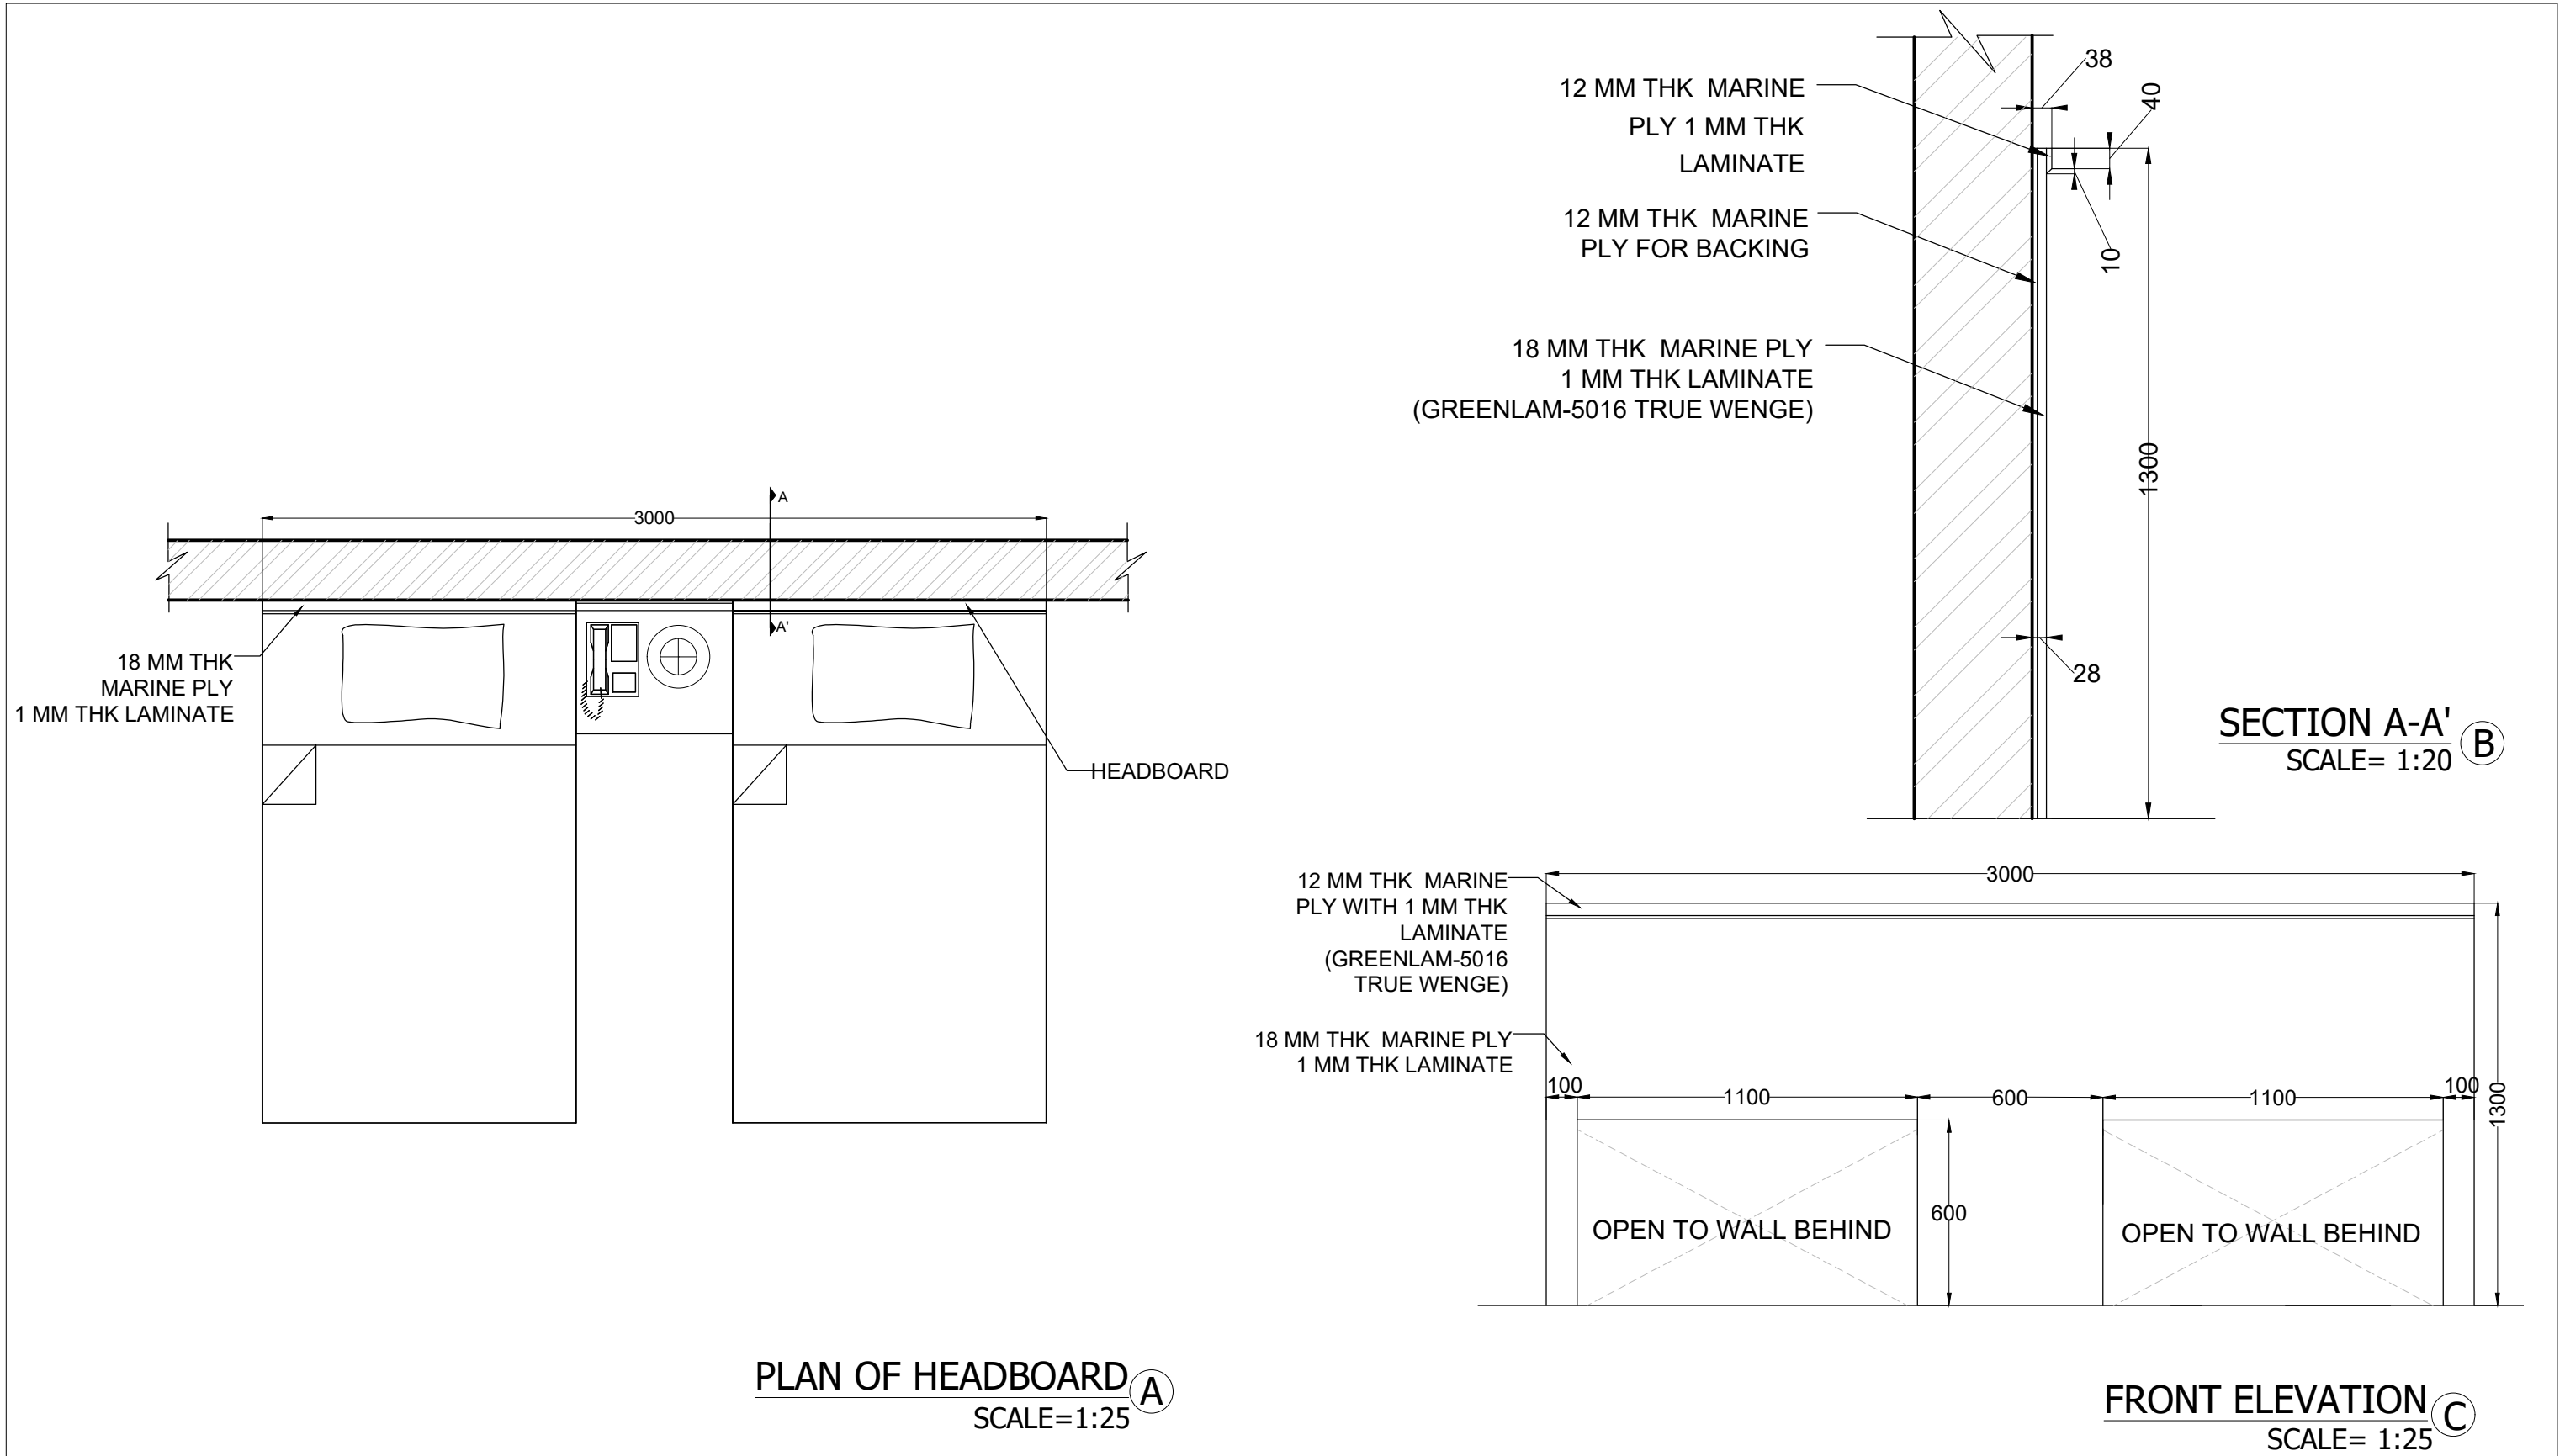

NOTES:

- DRAWINGS SHALL NOT BE SCALED.
- ALL DIMENSIONS ARE IN MM.
- ANY DISCREPANCY IN DRAWINGS AND EXISTING CONDITIONS SHOULD BE BROUGHT TO THE NOTICE OF THE ARCHITECT PRIOR TO PROCEEDING WITH THE ITEM
- FOR SIZE OF STRUCTURAL MEMBERS REFER STRUCTURAL ENGINEER'S DRAWINGS.
- ALL DOOR & WINDOW DIMENSIONS LISTED IN SCHEDULES MUST BE VERIFIED WITH SITE CONDITIONS BEFORE FABRICATION.
- ALL DOOR AND WINDOW DIMENSIONS ARE MASONARY DIMENSIONS
- CORELATE STRUCTURAL & ARCHITECT'S DWGS. AND GET BACK TO ARCHITECT WITH DISCREPANCIES IF ANY.

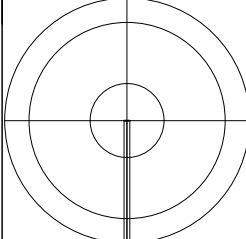					
	1	12.08.22	ISSUE FOR TENDER PURPOSE		
	No.	DATE	ISSUE/ REVISION		
	<u>I I T BOMBAY: VANVIHAR GUEST HOUSE</u>				
	POWAI, MUMBAI - 400 076, INDIA				
	UPENDRA NAYAK & ASSOCIATES			A11	
	ARCHITECTS. INTERIOR DESIGNERS				
1, SULBHA NIWAS. DILIP GUPTA MARG. MAHIM. MUMBAI 400016					
TEL: 24458473 FAX:24446223					
DATE: 21.02.2022		SCALE: AS NOTED	DRAWN BY:HR	CHECKED BY:AN	

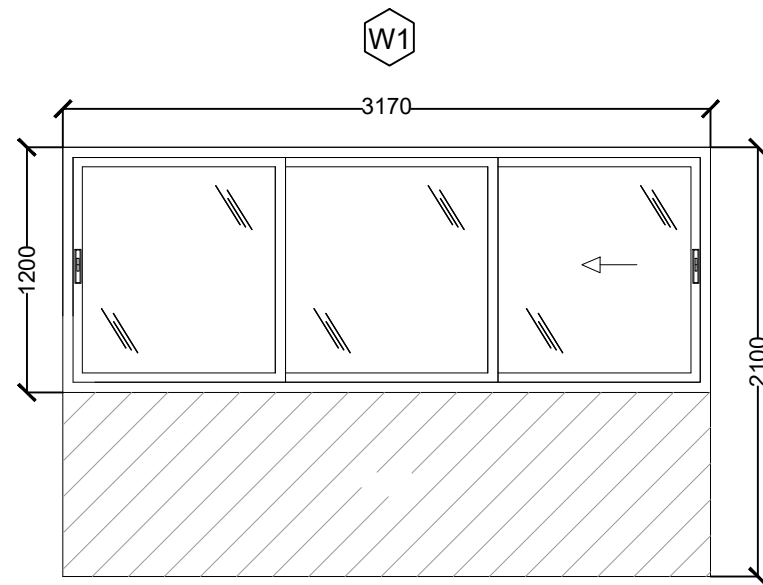

SLIDING WINDOW

WINDOW SCHEDULE OF VANVIHAR GUEST HOUSE						
SR. NO.	TYPE	NOS.	SIZE	SILL LVL.	LINTEL LVL.	DESCRIPTION
1	GUEST HOUSE TYPICAL ROOM					
1	W1	1	(3.17 x 1.2)	0.90	2.1	CASEMENT WINDOW IN UPVC SECTION WITH SLIDING WINDOW AND 6MM THICK SAINT GOBAIN CLEAR GLASS

NOTES:


1. DRAWINGS SHALL NOT BE SCALED.
2. ALL DIMENSIONS ARE IN MM.
3. ANY DISCREPANCY IN DRAWINGS AND EXISTING CONDITIONS SHOULD BE BROUGHT TO THE NOTICE OF THE ARCHITECT PRIOR TO PROCEEDING WITH THE ITEM
4. FOR SIZE OF STRUCTURAL MEMBERS REFER STRUCTURAL ENGINEER'S DRAWINGS.
5. ALL DOOR & WINDOW DIMENSIONS LISTED IN SCHEDULES MUST BE VERIFIED WITH SITE CONDITIONS BEFORE FABRICATION.
6. ALL DOOR AND WINDOW DIMENSIONS ARE MASONARY DIMENSIONS
- 7.CORELATE STRUCTURAL & ARCHITECT'S DWGS. AND GET BACK TO ARCHITECT WITH DISCREPANCIES IF ANY.

una

1	12.08.2022	ISSUE FOR TENDER PURPOSE
No.	DATE	ISSUE/ REVISION
I I T BOMBAY: VANVIHAR GUEST HOUSE POWAI, MUMBAI - 400 076, INDIA		
UPENDRA NAYAK & ASSOCIATES ARCHITECTS. INTERIOR DESIGNERS 1, SULBHA NIWAS. DILIP GUPTA MARG. MAHIM. MUMBAI 400016 TEL: 24458473 FAX:24446223		A12
DATE: 21.02.2022	SCALE:AS NOTED	DRAWN BY:HR
CHECKED BY:AB		




1. DRAWINGS SHALL NOT BE SCALED.
2. ALL DIMENSIONS ARE IN MM.
3. ANY DISCREPANCY IN DRAWINGS AND EXISTING CONDITIONS SHOULD BE BROUGHT TO THE NOTICE OF THE ARCHITECT PRIOR TO PROCEEDING WITH THE ITEM
4. FOR SIZE OF STRUCTURAL MEMBERS REFER STRUCTURAL ENGINEER'S DRAWINGS.
5. ALL DOOR & WINDOW DIMENSIONS LISTED IN SCHEDULES MUST BE VERIFIED WITH SITE CONDITIONS BEFORE FABRICATION.
6. ALL DOOR AND WINDOW DIMENSIONS ARE MASONRY DIMENSIONS
7. CORRELATE STRUCTURAL & ARCHITECT'S DWGS. AND GET BACK TO ARCHITECT WITH DISCREPANCIES IF ANY.

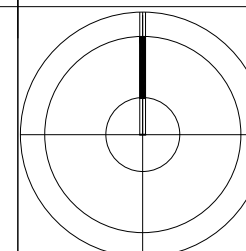

1	12.08.2022	ISSUE FOR TENDER PURPOSE	
No.	DATE	ISSUE/ REVISION	
<u>I I T BOMBAY: VANVIHAR GUEST HOUSE</u> POWAI, MUMBAI - 400 076, INDIA			
UPENDRA NAYAK & ASSOCIATES ARCHITECTS. INTERIOR DESIGNERS 1, SULBHA NIWAS. DILIP GUPTA MARG. MAHIM. MUMBAI 400016 TEL: 24458473 FAX:24446223		A13	
DATE: 21.02.2022	SCALE: AS NOTED		DRAWN BY:HR

A13

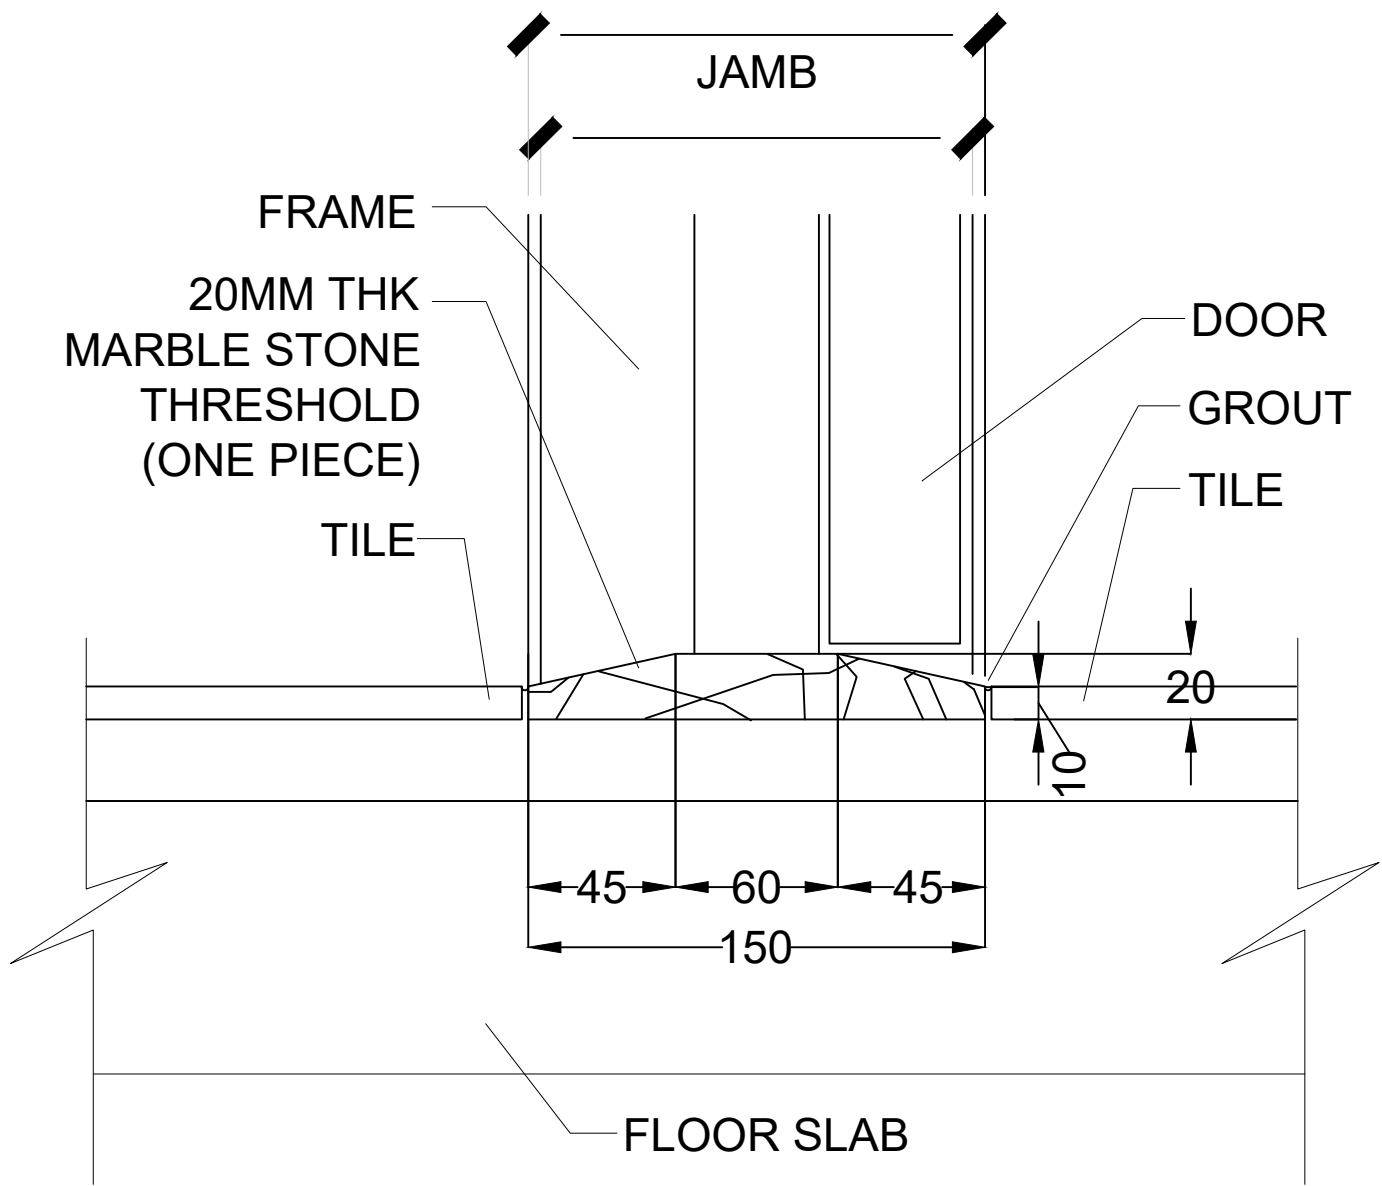

MAIN DOOR THRESHOLD DETAIL

MAIN DOOR THRESHOLD DETAIL DRAWING ^A
SCALE= 1:25

NOTES:


- 1. DRAWINGS SHALL NOT BE SCALED.
- 2. ALL DIMENSIONS ARE IN MM.
- 3. ANY DISCREPANCY IN DRAWINGS AND EXISTING CONDITIONS SHOULD BE BROUGHT TO THE NOTICE OF THE ARCHITECT PRIOR TO PROCEEDING WITH THE ITEM
- 4. FOR SIZE OF STRUCTURAL MEMBERS REFER STRUCTURAL ENGINEER'S DRAWINGS.
- 5. ALL DOOR & WINDOW DIMENSIONS LISTED IN SCHEDULES MUST BE VERIFIED WITH SITE CONDITIONS BEFORE FABRICATION.
- 6. ALL DOOR AND WINDOW DIMENSIONS ARE MASONARY DIMENSIONS
- 7.CORELATE STRUCTURAL & ARCHITECT'S DWGS. AND GET BACK TO ARCHITECT WITH DISCREPANCIES IF ANY.

una


1	12.08.22	ISSUE FOR TENDER PURPOSE	
No.	DATE	ISSUE/ REVISION	
I I T BOMBAY: VANVIHAR GUEST HOUSE			
POWAI, MUMBAI - 400 076, INDIA			
UPENDRA NAYAK & ASSOCIATES		A14	
ARCHITECTS. INTERIOR DESIGNERS			
1, SULBHA NIWAS, DILIP GUPTA MARG, MAHIM, MUMBAI 400016			
TEL: 24458473 FAX:24446223			
DATE: 04.08.2022	SCALE: AS NOTED	DRAWN BY: HR	CHECKED BY: AN

ARCHITECTURAL DETAIL DRAWINGS- SECOND FLOOR

TENDER DRAWINGS

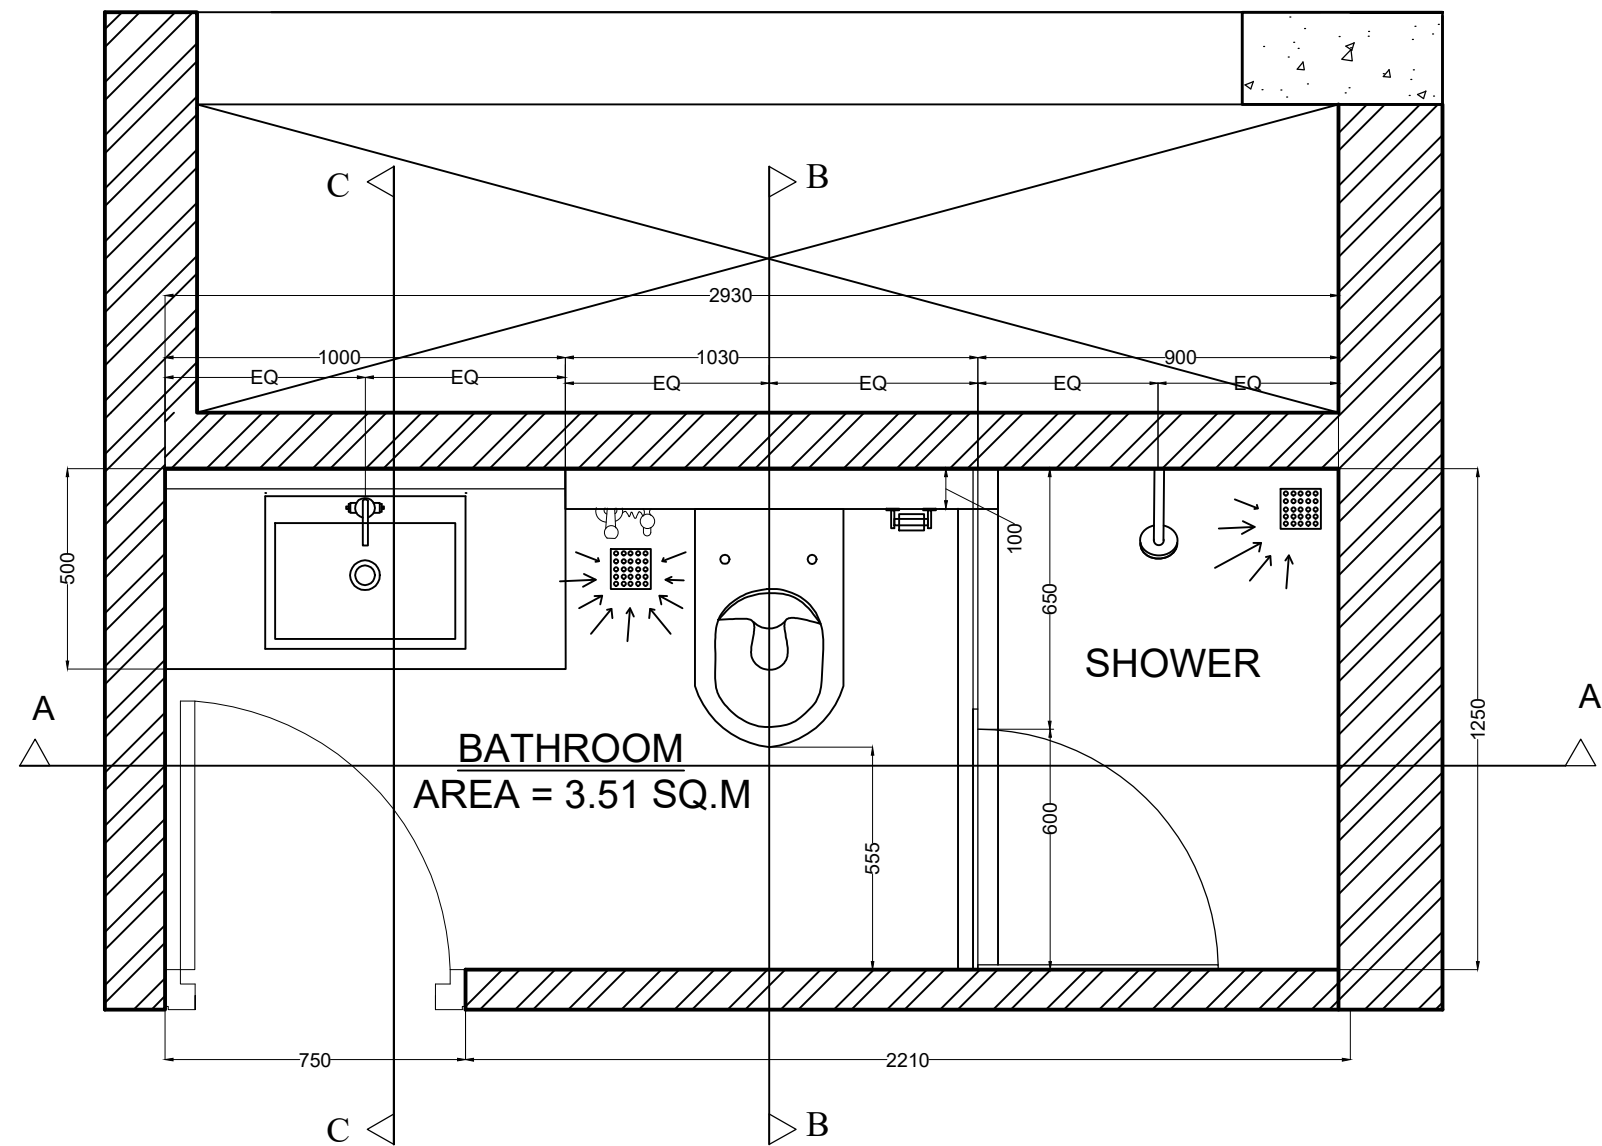



BATHROOM PLAN (A)
SCALE= 1:50

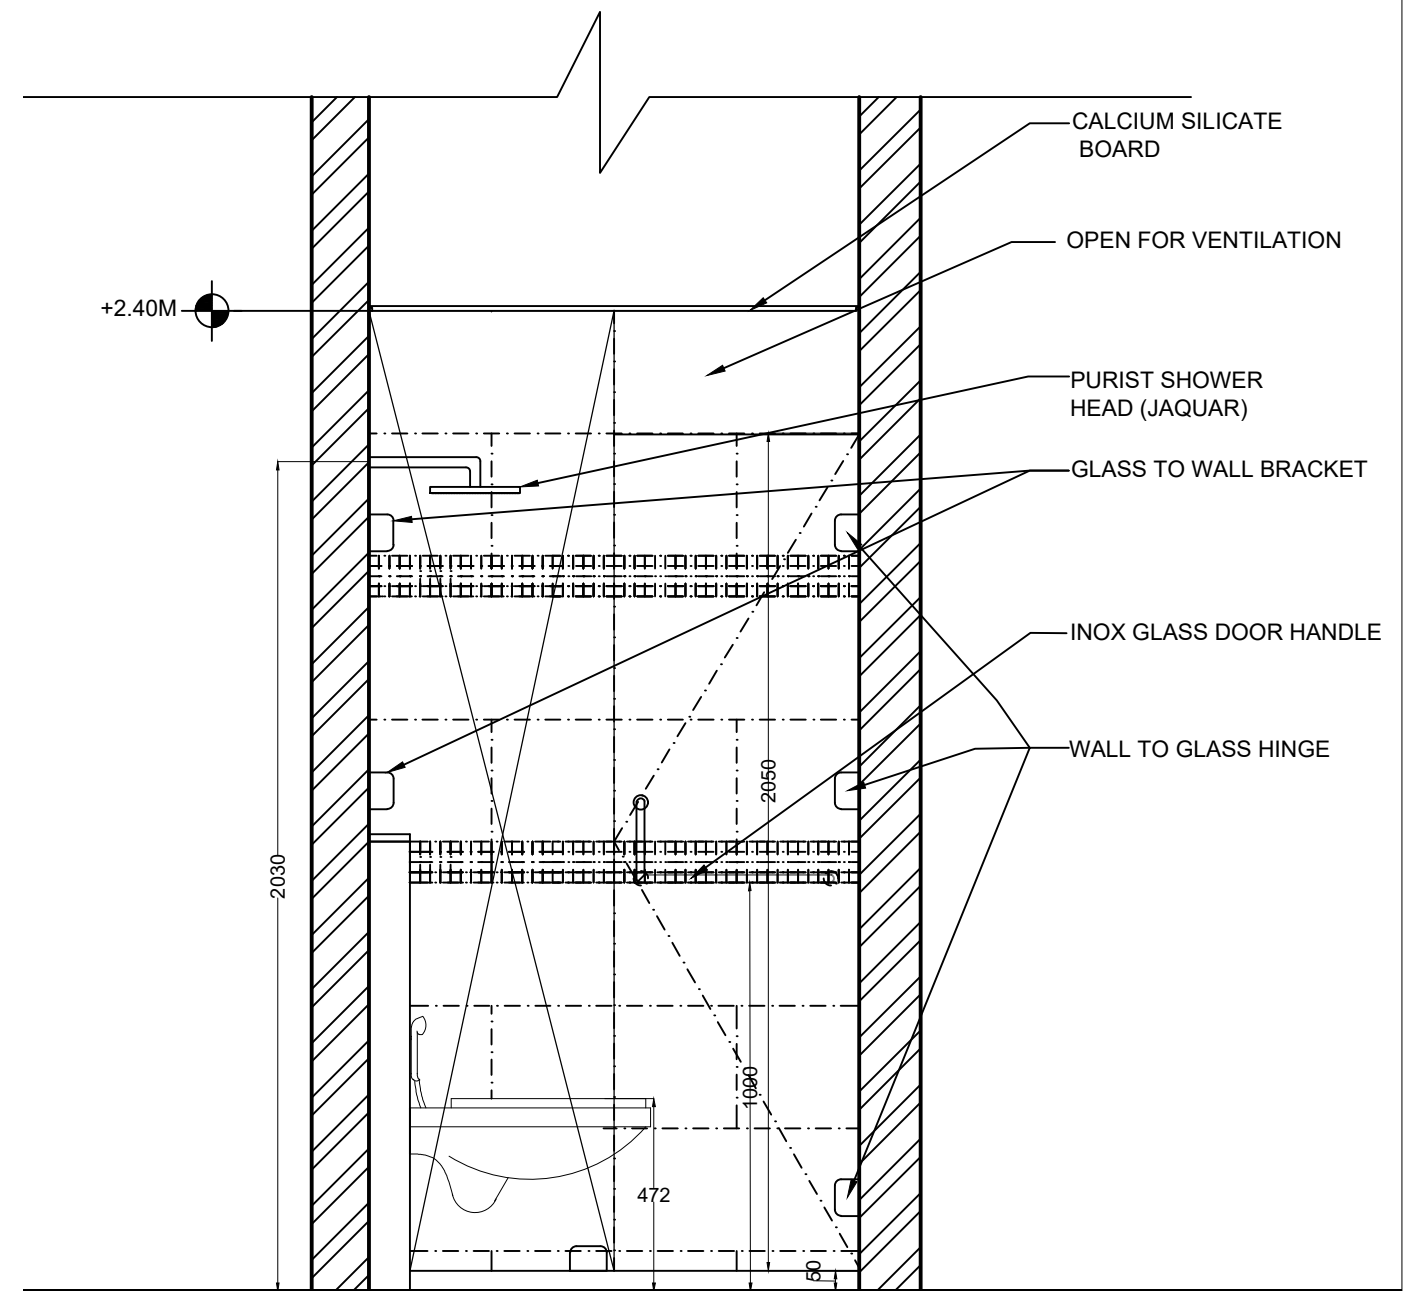

NOTES:

1. DRAWINGS SHALL NOT BE SCALED.
2. ALL DIMENSIONS ARE IN MM.
3. ANY DISCREPANCY IN DRAWINGS AND EXISTING CONDITIONS SHOULD BE BROUGHT TO THE NOTICE OF THE ARCHITECT PRIOR TO PROCEEDING WITH THE ITEM
4. FOR SIZE OF STRUCTURAL MEMBERS REFER STRUCTURAL ENGINEER'S DRAWINGS.
5. ALL DOOR & WINDOW DIMENSIONS LISTED IN SCHEDULES MUST BE VERIFIED WITH SITE CONDITIONS BEFORE FABRICATION.
6. ALL DOOR AND WINDOW DIMENSIONS ARE MASONARY DIMENSIONS
7. CORELATE STRUCTURAL & ARCHITECT'S DWGS. AND GET BACK TO ARCHITECT WITH DISCREPANCIES IF ANY.

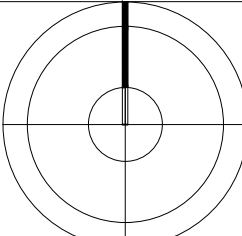			
	1	12.08.22	ISSUE FOR TENDER PURPOSE
	No.	DATE	ISSUE/ REVISION
	I I T BOMBAY: VANVIHAR GUEST HOUSE		
	POWAI, MUMBAI - 400 076, INDIA		
	UPENDRA NAYAK & ASSOCIATES		A6a
ARCHITECTS. INTERIOR DESIGNERS 1, SULBHA NIWAS. DILIP GUPTA MARG. MAHIM. MUMBAI 400016 TEL: 24458473 FAX:24446223			
DATE: 21.02.2022		SCALE: AS NOTED	DRAWN BY:HR

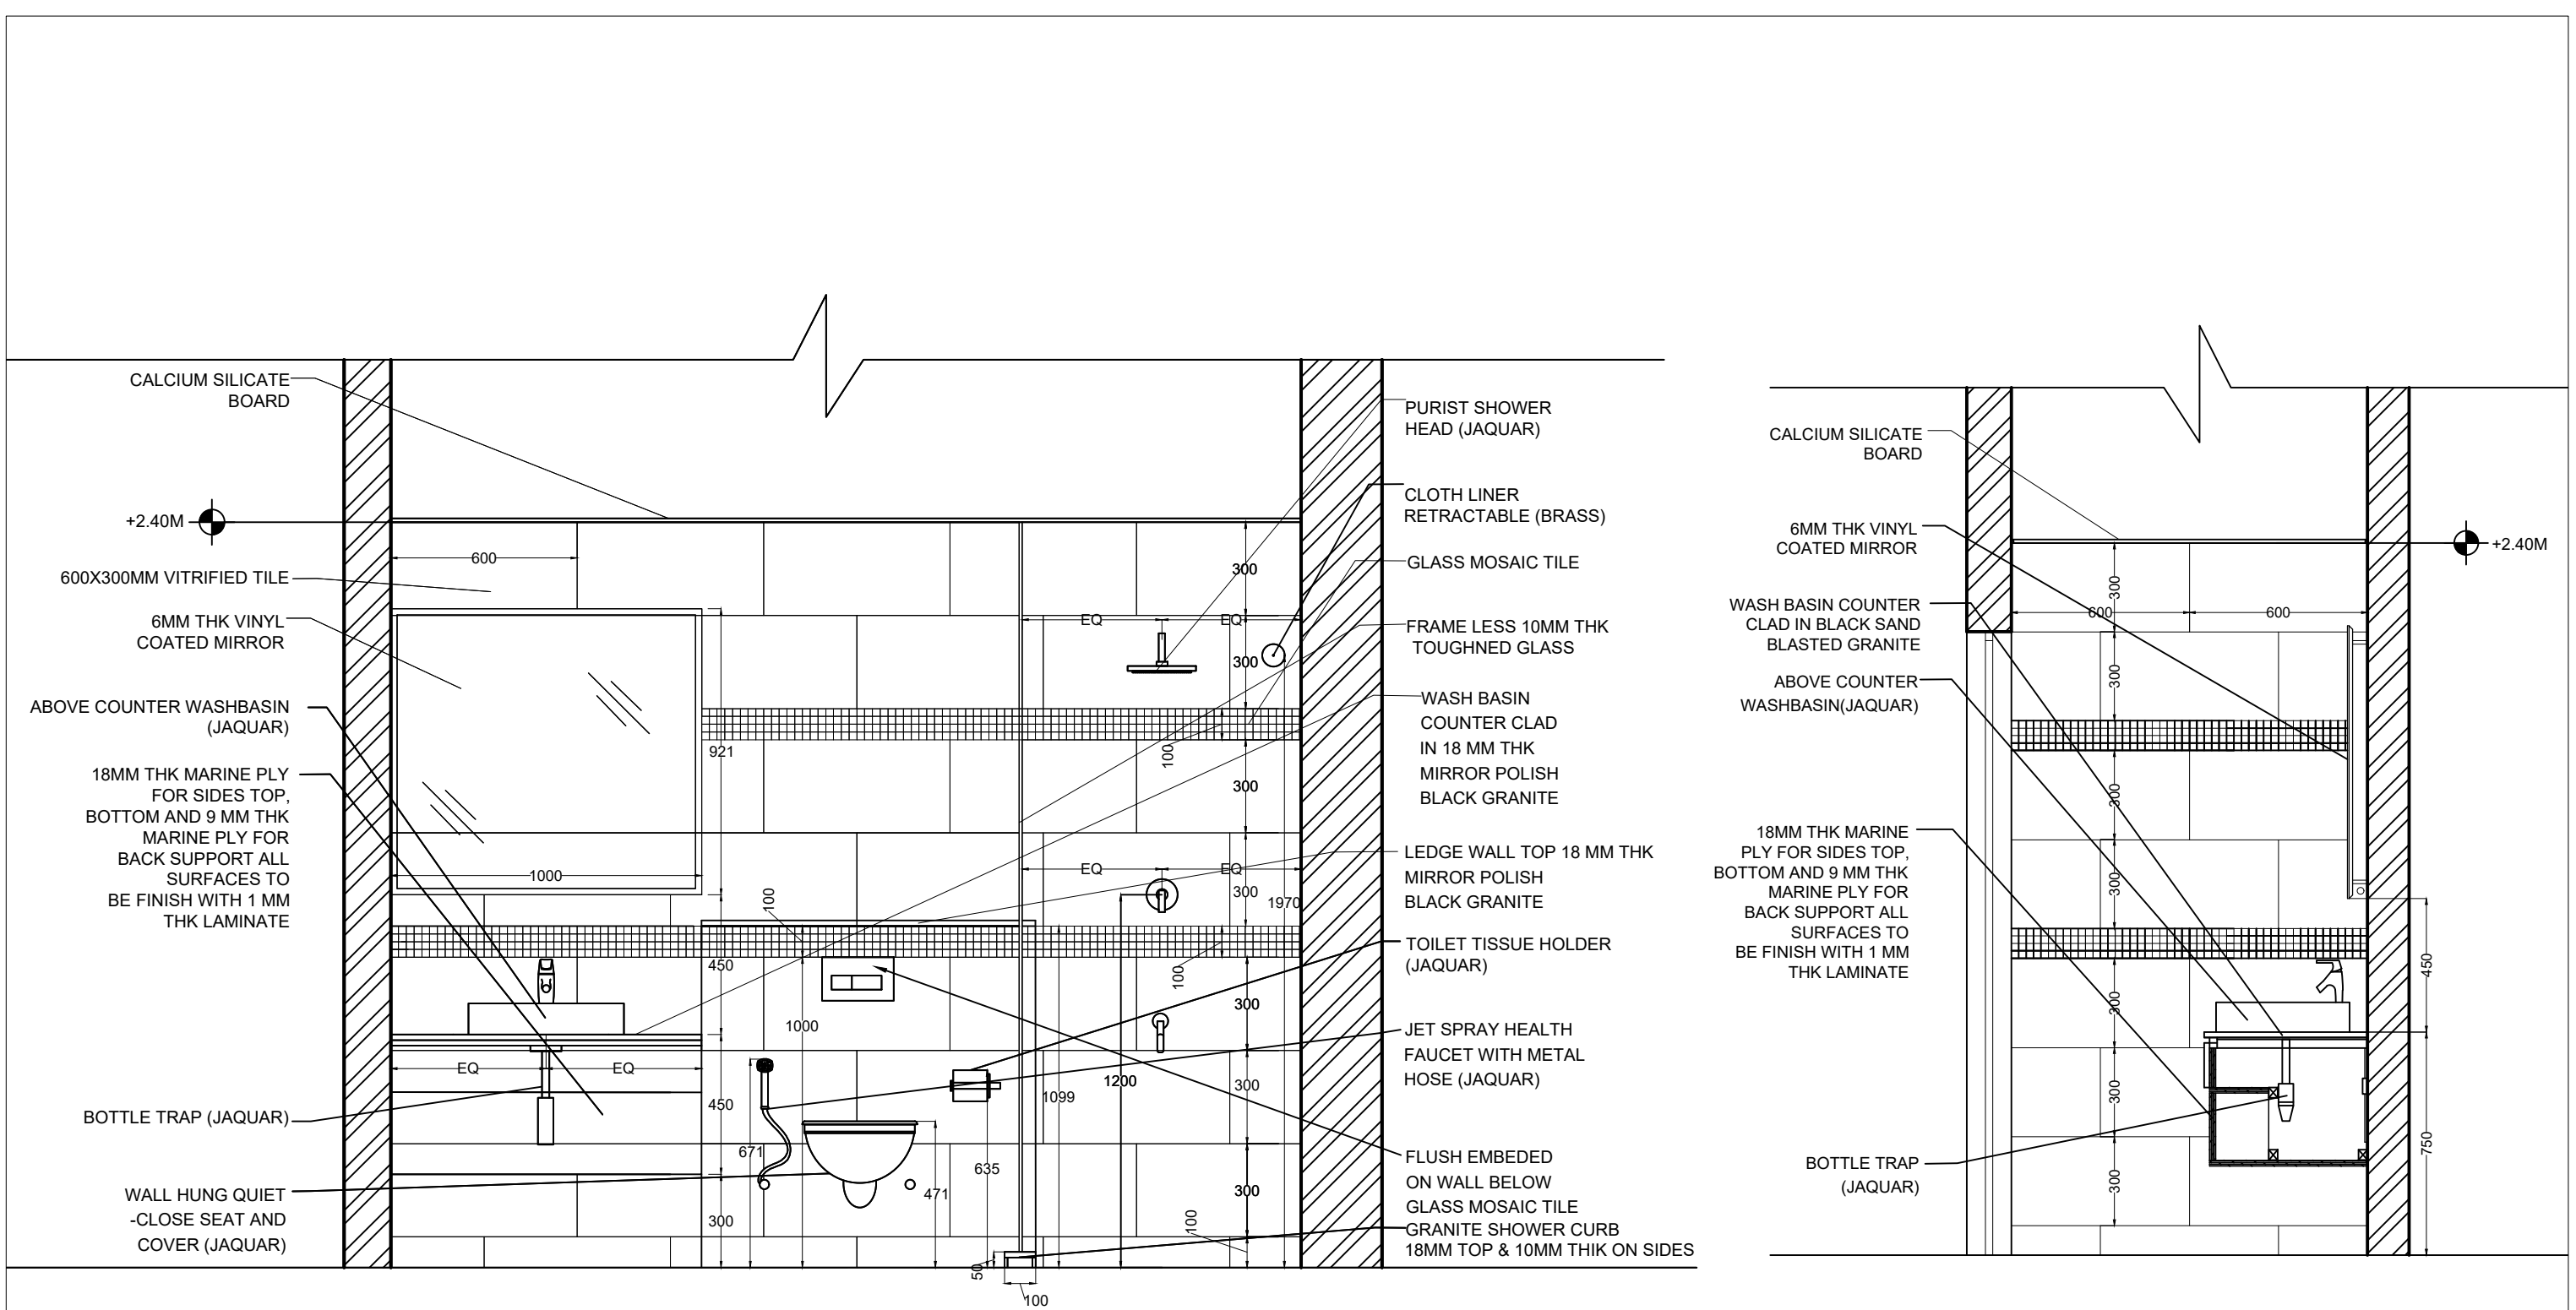


NOTES:


- DRAWINGS SHALL NOT BE SCALED.
- ALL DIMENSIONS ARE IN MM.
- ANY DISCREPANCY IN DRAWINGS AND EXISTING CONDITIONS SHOULD BE BROUGHT TO THE NOTICE OF THE ARCHITECT PRIOR TO PROCEEDING WITH THE ITEM
- FOR SIZE OF STRUCTURAL MEMBERS REFER STRUCTURAL ENGINEER'S DRAWINGS.
- ALL DOOR & WINDOW DIMENSIONS LISTED IN SCHEDULES MUST BE VERIFIED WITH SITE CONDITIONS BEFORE FABRICATION.
- ALL DOOR AND WINDOW DIMENSIONS ARE MASONARY DIMENSIONS
- CORELATE STRUCTURAL & ARCHITECT'S DWGS. AND GET BACK TO ARCHITECT WITH DISCREPANCIES IF ANY.

una

1	12.08.2022	ISSUE FOR TENDER PURPOSE
No.	DATE	ISSUE/ REVISION
I I T BOMBAY: VANVIHAR GUEST HOUSE POWAI, MUMBAI - 400 076, INDIA		
UPENDRA NAYAK & ASSOCIATES ARCHITECTS. INTERIOR DESIGNERS 1, SULBHA NIWAS. DILIP GUPTA MARG. MAHIM. MUMBAI 400016 TEL: 24458473 FAX:24446223		A6b
DATE: 21.02.2022	SCALE: AS NOTED	

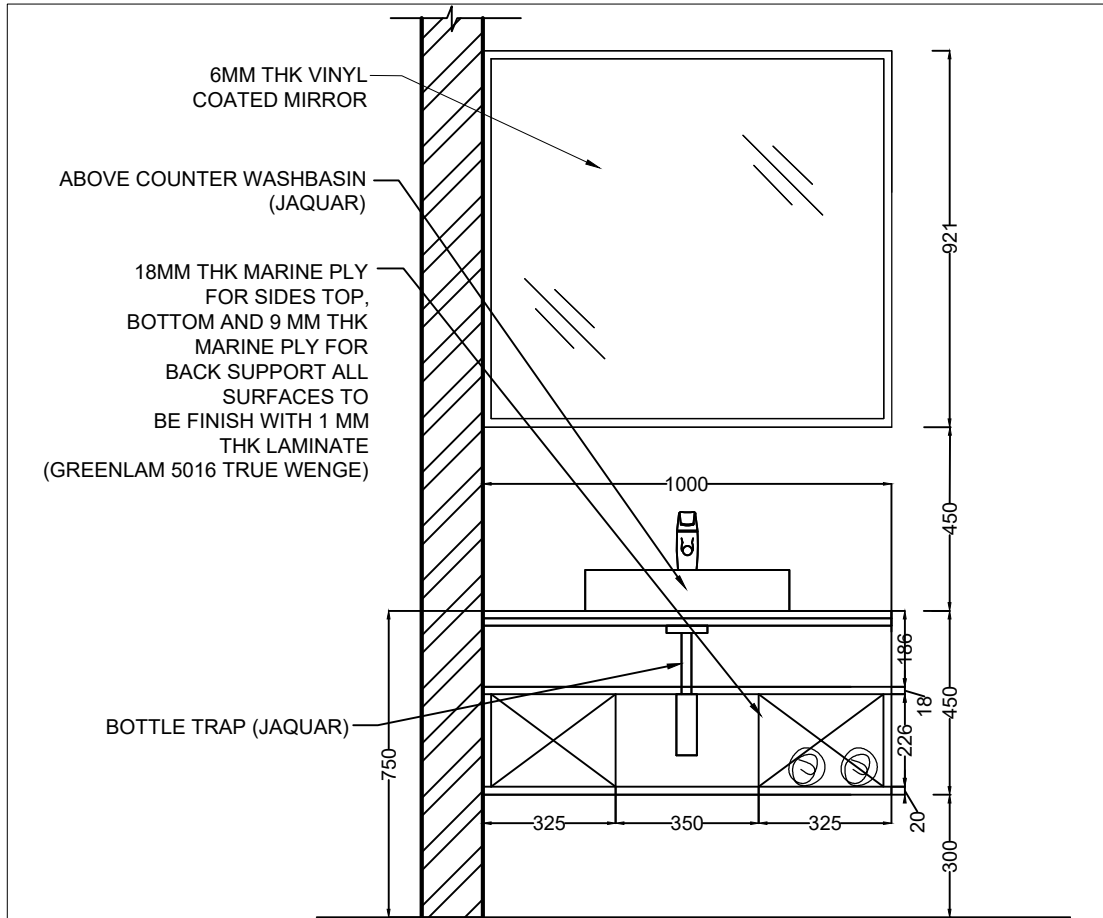


FRONT ELEVATION ^(A)
SCALE= 1:20

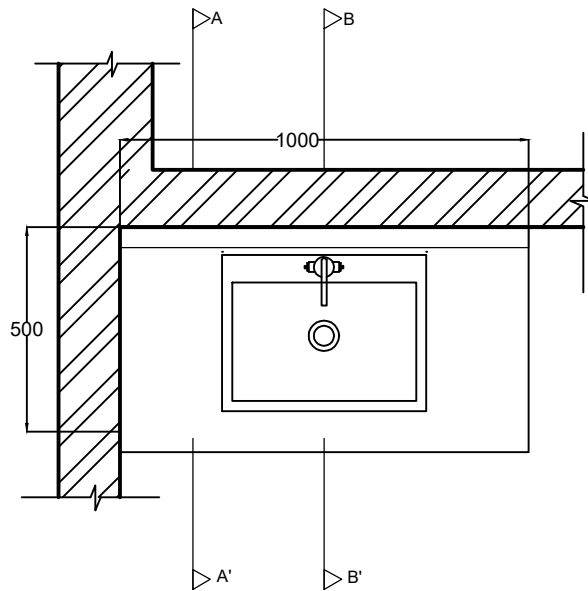


PLAN OF WASHBASIN COUNTER ^(C)
SCALE= 1:20

NOTES:

- DRAWINGS SHALL NOT BE SCALED.
- ALL DIMENSIONS ARE IN MM.
- ANY DISCREPANCY IN DRAWINGS AND EXISTING CONDITIONS SHOULD BE BROUGHT TO THE NOTICE OF THE ARCHITECT PRIOR TO PROCEEDING WITH THE ITEM
- FOR SIZE OF STRUCTURAL MEMBERS REFER STRUCTURAL ENGINEER'S DRAWINGS.
- ALL DOOR & WINDOW DIMENSIONS LISTED IN SCHEDULES MUST BE VERIFIED WITH SITE CONDITIONS BEFORE FABRICATION.
- ALL DOOR AND WINDOW DIMENSIONS ARE MASONARY DIMENSIONS
- CORELATE STRUCTURAL & ARCHITECT'S DWGS. AND GET BACK TO ARCHITECT WITH DISCREPANCIES IF ANY.

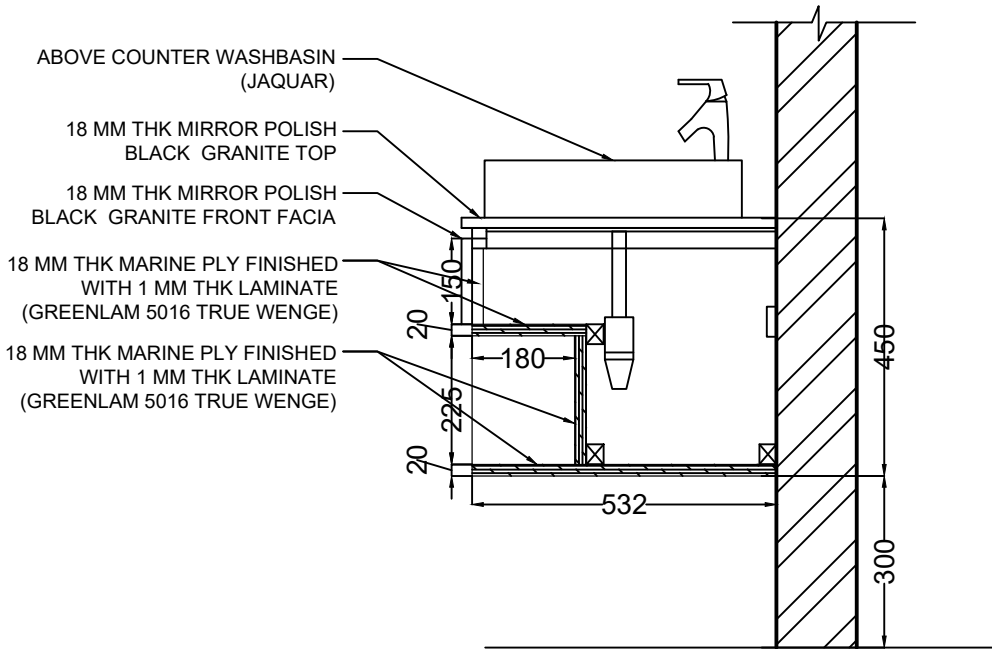


SECTION A-A' ^(B)
SCALE= 1:15

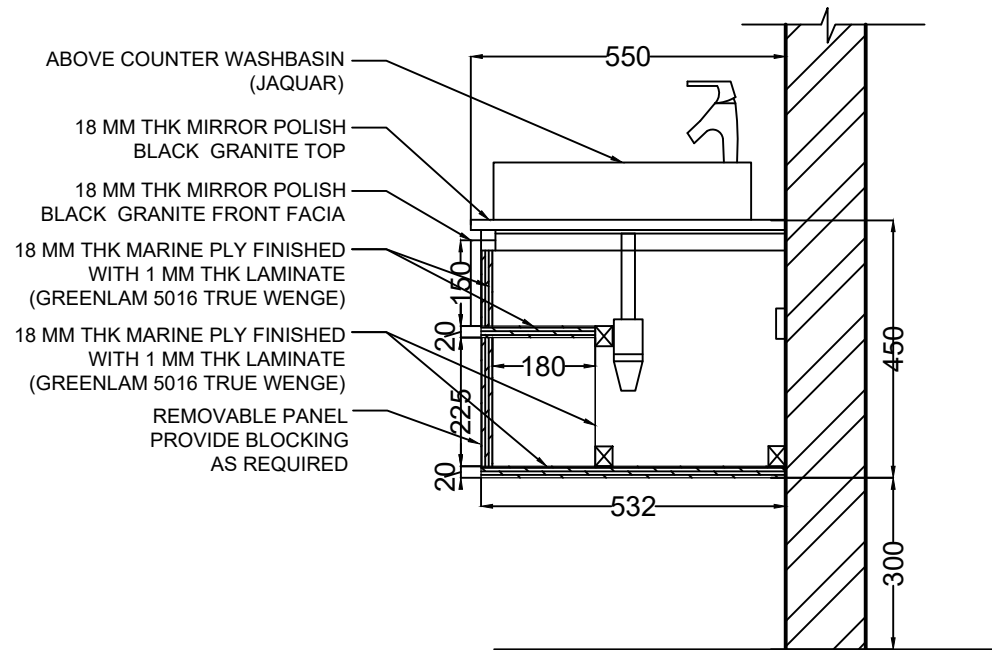


SECTION B-B' ^(D)
SCALE= 1:15


una

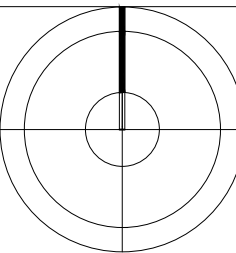

1	12.08.2022	ISSUE FOR TENDER PURPOSE
No.	DATE	ISSUE/ REVISION
<u>I I T BOMBAY: VANVIHAR GUEST HOUSE</u>		
POWAI, MUMBAI - 400 076, INDIA		
UPENDRA NAYAK & ASSOCIATES ARCHITECTS. INTERIOR DESIGNERS 1, SULBHA NIWAS. DILIP GUPTA MARG. MAHIM. MUMBAI 400016 TEL: 24458473 FAX:24446223		A6c
DATE: 21.02.2022	SCALE: AS NOTED	
		DRAWN BY:HR

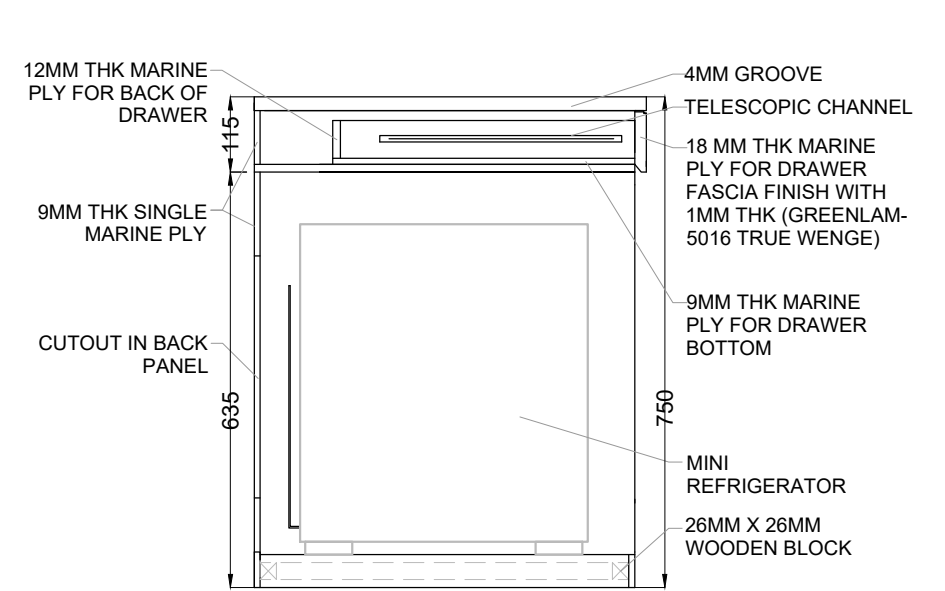


SECTION B-B' (C)
SCALE= 1:75

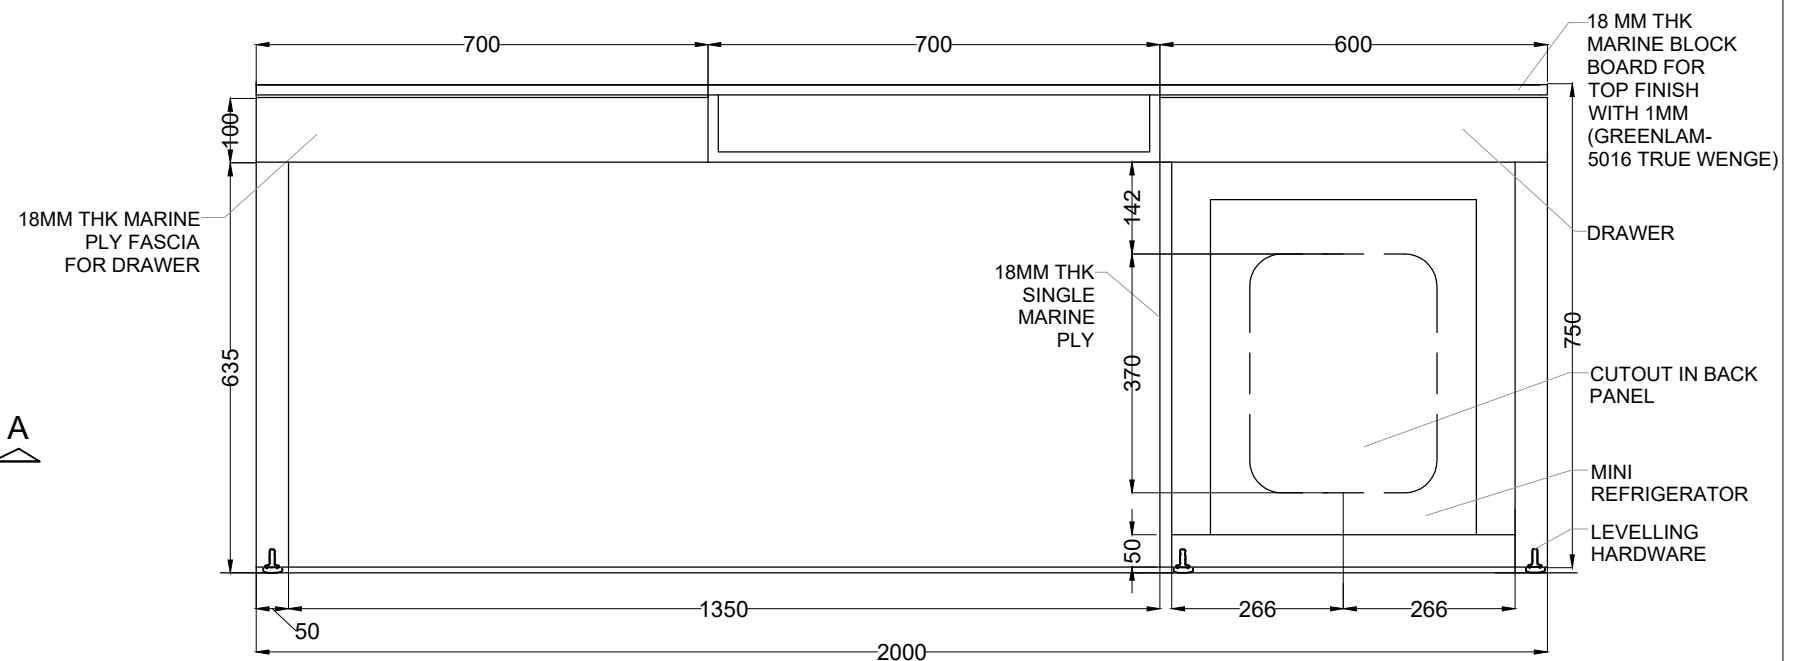


FRONT ELEVATION
SCALE= 1:75 (D)


1. DRAWINGS SHALL NOT BE SCALED.
2. ALL DIMENSIONS ARE IN MM.
3. ANY DISCREPANCY IN DRAWINGS AND EXISTING CONDITIONS SHOULD BE BROUGHT TO THE NOTICE OF THE ARCHITECT PRIOR TO PROCEEDING WITH THE ITEM
4. FOR SIZE OF STRUCTURAL MEMBERS REFER STRUCTURAL ENGINEER'S DRAWINGS.
5. ALL DOOR & WINDOW DIMENSIONS LISTED IN SCHEDULES MUST BE VERIFIED WITH SITE CONDITIONS BEFORE FABRICATION.
6. ALL DOOR AND WINDOW DIMENSIONS ARE MASONARY DIMENSIONS
7. CORRELATE STRUCTURAL & ARCHITECT'S DWGS. AND GET BACK TO ARCHITECT WITH DISCREPANCIES IF ANY.

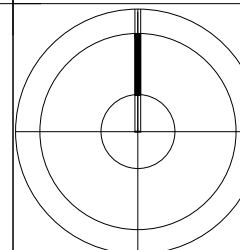


1	12.08.22	ISSUE FOR TENDER PURPOSE	
No.	DATE	ISSUE/ REVISION	
<u>I I T BOMBAY: VANVIHAR GUEST HOUSE</u> POWAI, MUMBAI - 400 076, INDIA			
UPENDRA NAYAK & ASSOCIATES ARCHITECTS. INTERIOR DESIGNERS 1, SULBHA NIWAS. DILIP GUPTA MARG. MAHIM, MUMBAI 400016 TEL: 24458473 FAX:24446223		A7	
DATE:21.02.2022	SCALE:AS NOTED		DRAWN BY:HR

A7

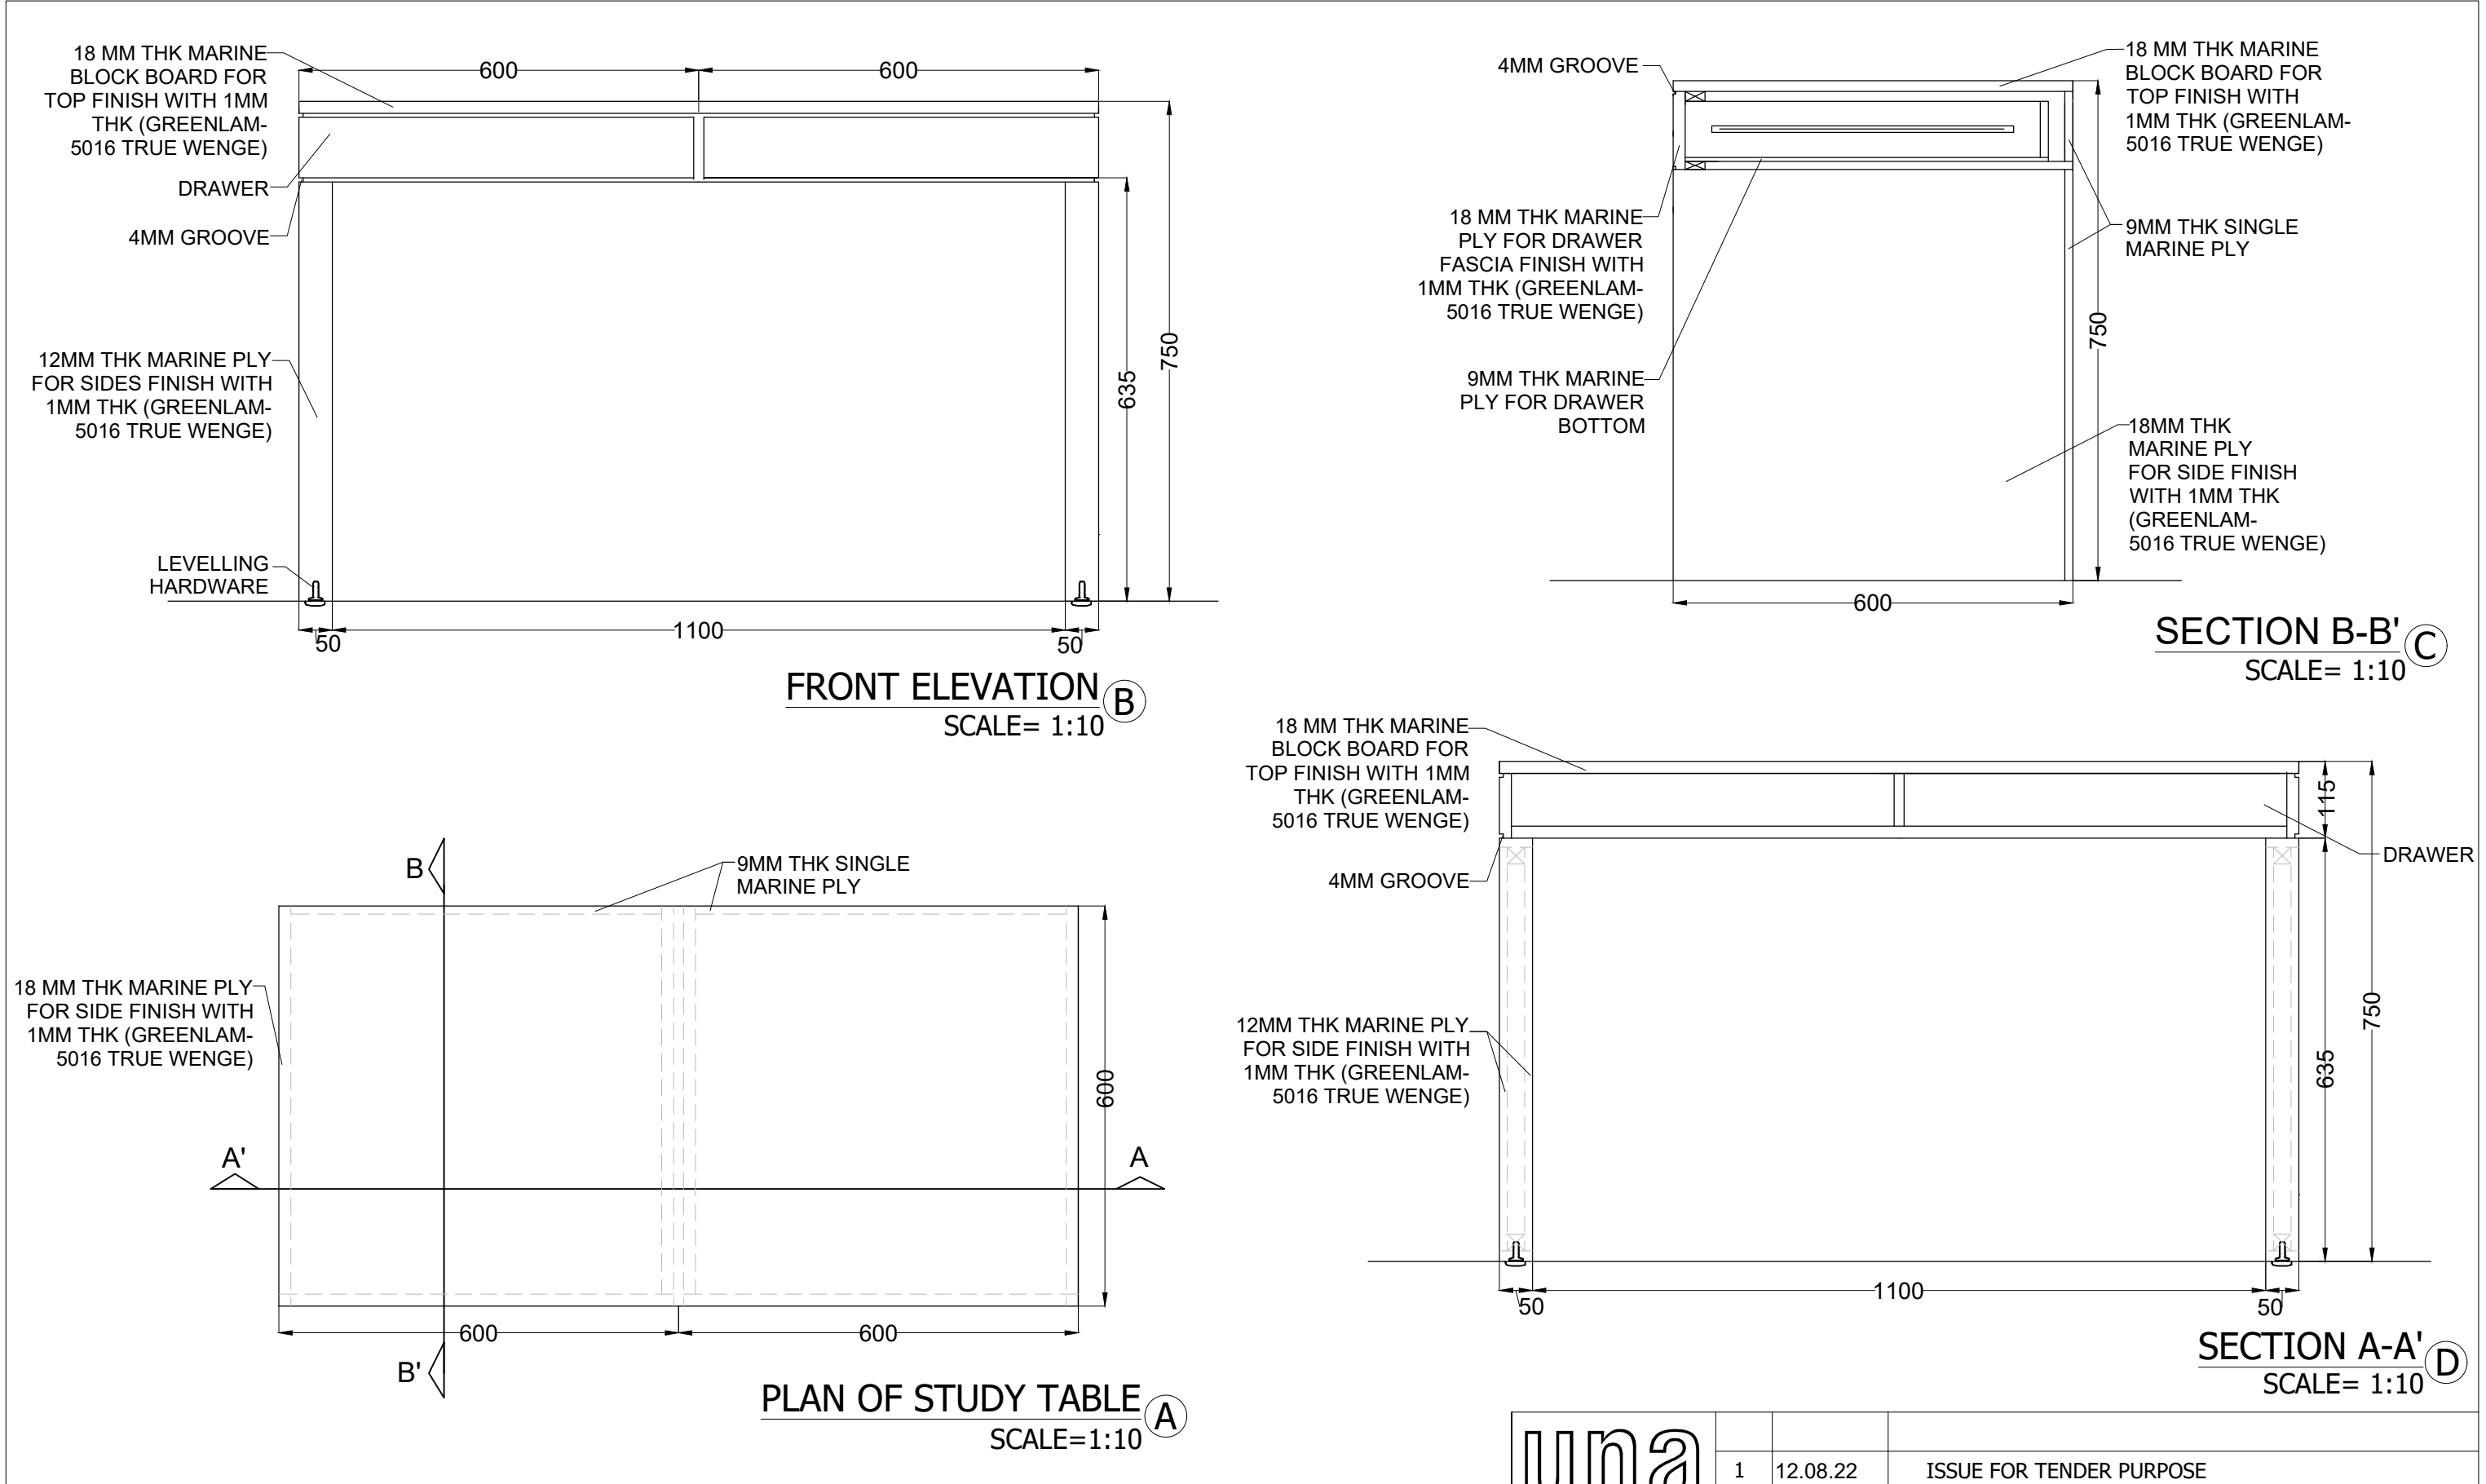

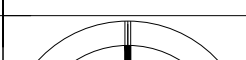NOTES:		una		No.		DATE		ISSUE/ REVISION			
1. DRAWINGS SHALL NOT BE SCALED. 2. ALL DIMENSIONS ARE IN MM. 3. ANY DISCREPANCY IN DRAWINGS AND EXISTING CONDITIONS SHOULD BE BROUGHT TO THE NOTICE OF THE ARCHITECT PRIOR TO PROCEEDING WITH THE ITEM 4. FOR SIZE OF STRUCTURAL MEMBERS REFER STRUCTURAL ENGINEER'S DRAWINGS. 5. ALL DOOR & WINDOW DIMENSIONS LISTED IN SCHEDULES MUST BE VERIFIED WITH SITE CONDITIONS BEFORE FABRICATION. 6. ALL DOOR AND WINDOW DIMENSIONS ARE MASONARY DIMENSIONS 7.CORELATE STRUCTURAL & ARCHITECT'S DWGS. AND GET BACK TO ARCHITECT WITH DISCREPANCIES IF ANY.				I I T BOMBAY: VANVIHAR GUEST HOUSE POWAI, MUMBAI - 400 076, INDIA							
				UPENDRA NAYAK & ASSOCIATES ARCHITECTS. INTERIOR DESIGNERS 1, SULBHA NIWAS. DILIP GUPTA MARG. MAHIM. MUMBAI 400016 TEL: 24458473 FAX:24446223							
				A8							
				DATE: 21.02.2022		SCALE:AS NOTED		DRAWN BY:HR		CHECKED BY: AN	

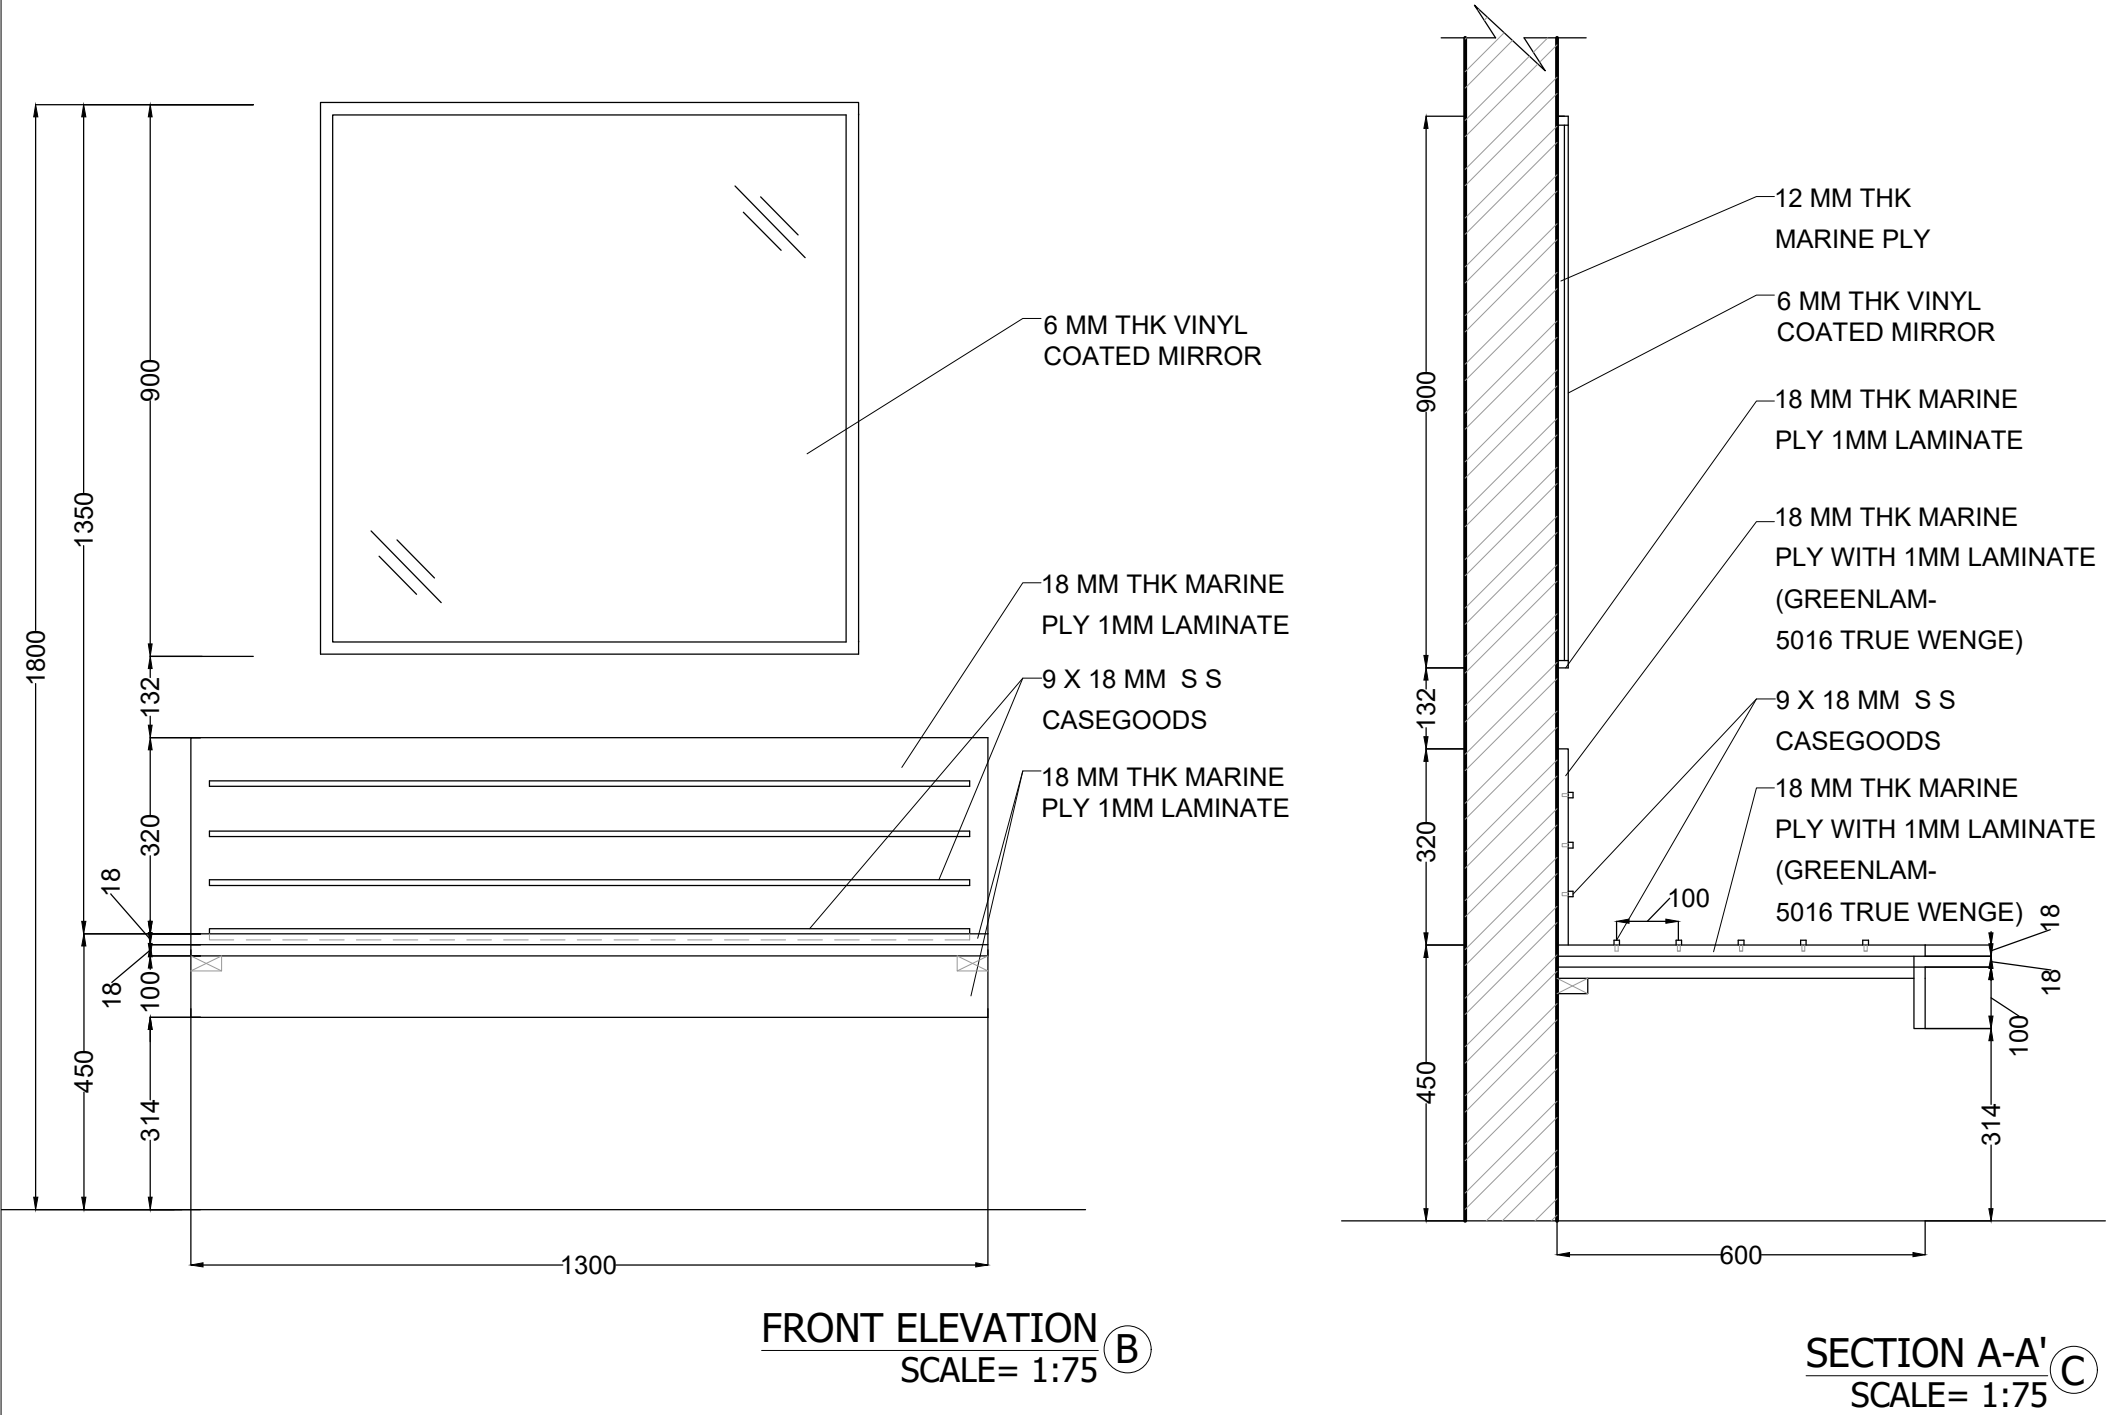


NOTES:

1. DRAWINGS SHALL NOT BE SCALED.
2. ALL DIMENSIONS ARE IN MM.
3. ANY DISCREPANCY IN DRAWINGS AND EXISTING CONDITIONS SHOULD BE BROUGHT TO THE NOTICE OF THE ARCHITECT PRIOR TO PROCEEDING WITH THE ITEM
4. FOR SIZE OF STRUCTURAL MEMBERS REFER STRUCTURAL ENGINEER'S DRAWINGS.
5. ALL DOOR & WINDOW DIMENSIONS LISTED IN SCHEDULES MUST BE VERIFIED WITH SITE CONDITIONS BEFORE FABRICATION.
6. ALL DOOR AND WINDOW DIMENSIONS ARE MASONARY DIMENSIONS
7. CORELATE STRUCTURAL & ARCHITECT'S DWGS. AND GET BACK TO ARCHITECT WITH DISCREPANCIES IF ANY.


una				
1	12.08.22	ISSUE FOR TENDER PURPOSE		
No.	DATE	ISSUE/ REVISION		
I I T BOMBAY: VANVIHAR GUEST HOUSE				
POWAI, MUMBAI - 400 076, INDIA				
UPENDRA NAYAK & ASSOCIATES			A9	
ARCHITECTS. INTERIOR DESIGNERS				
1, SULBHA NIWAS. DILIP GUPTA MARG. MAHIM. MUMBAI 400016				
TEL: 24458473 FAX:24446223				
DATE: 21.02.2022		SCALE: AS NOTED	DRAWN BY: HR	CHECKED BY: AN




WARDROBE DETAIL WITH SAFE

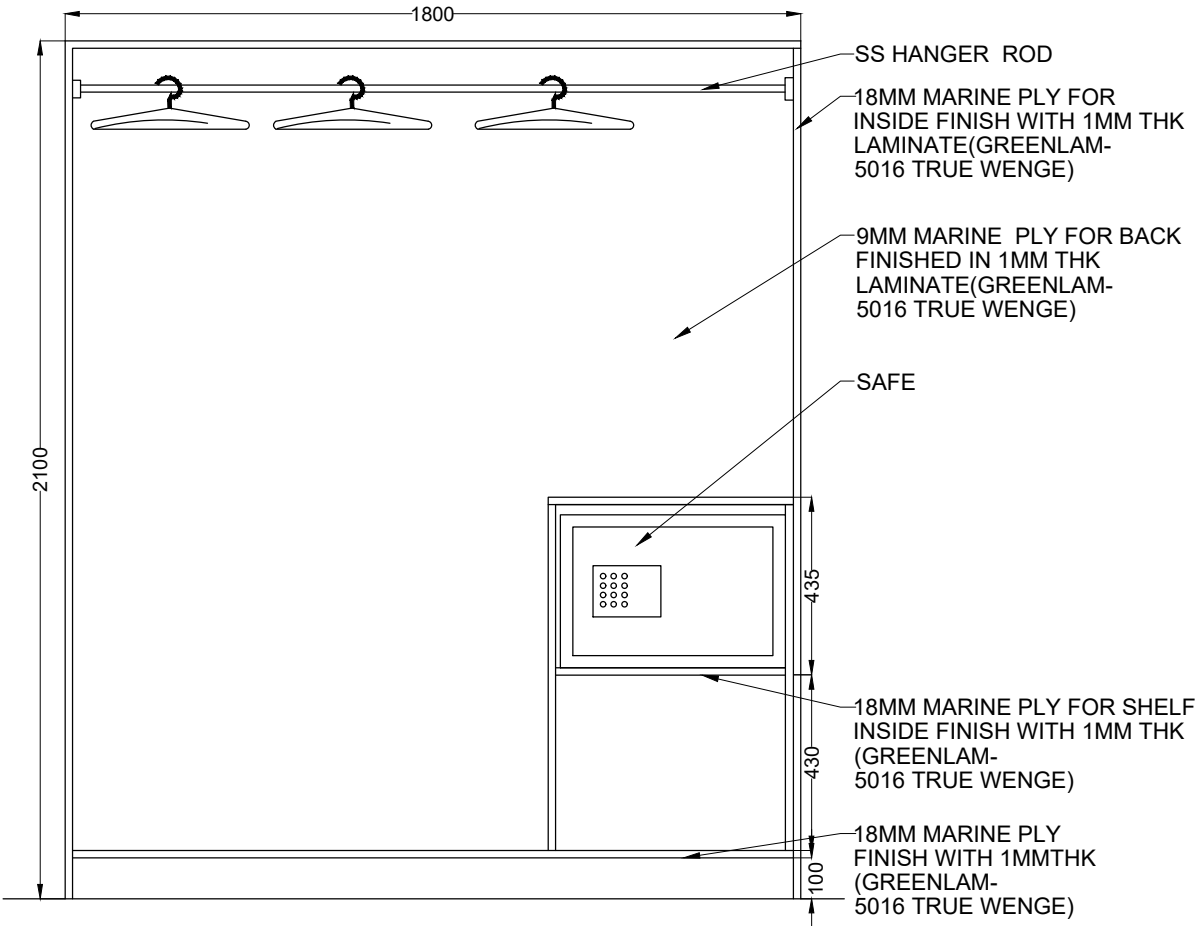


SECTION A-A' ^D
SCALE=1:20

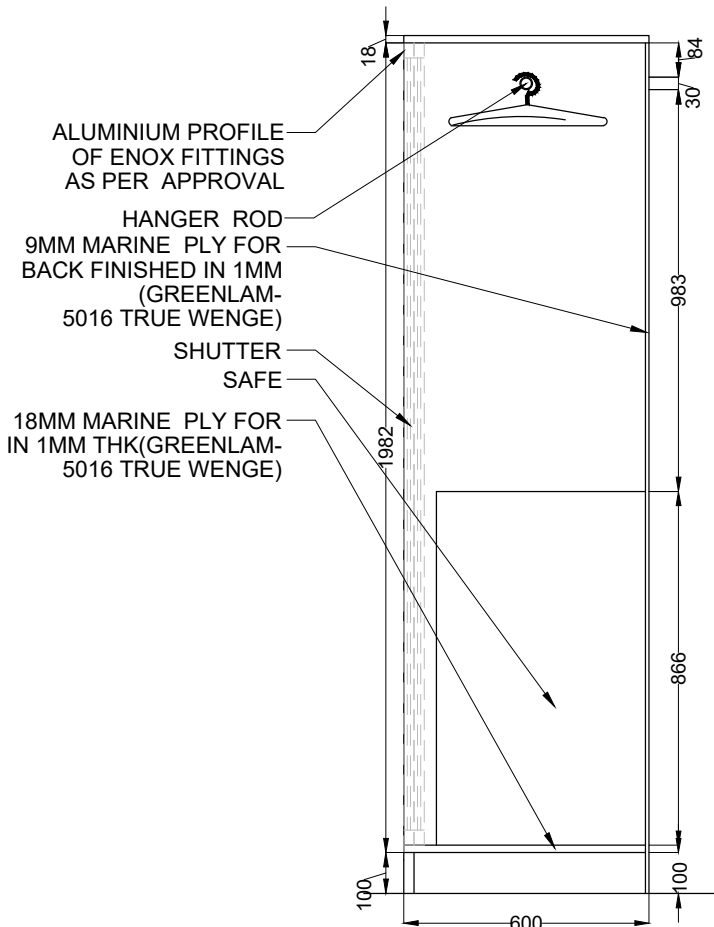

SECTION B-B' ^C
SCALE=1:20

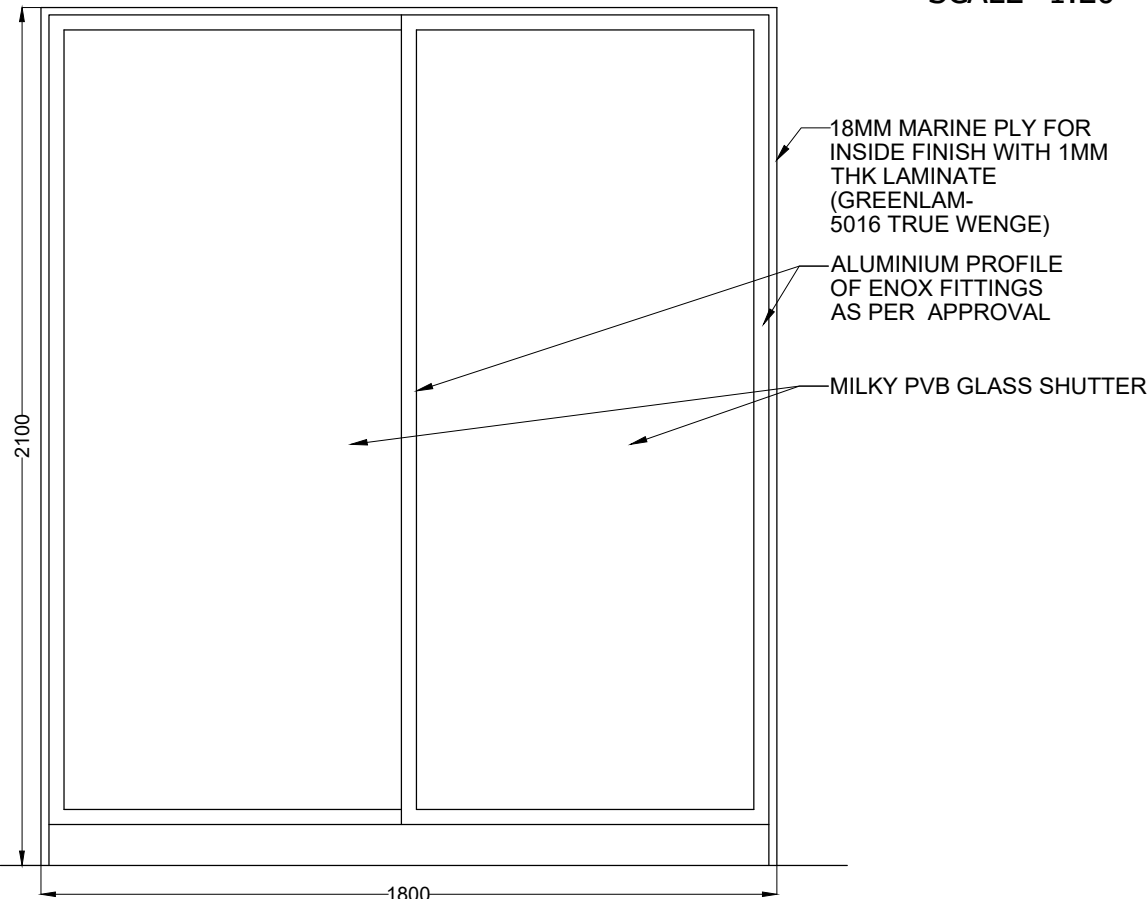

FRONT ELEVATION ^B
SCALE=1:20

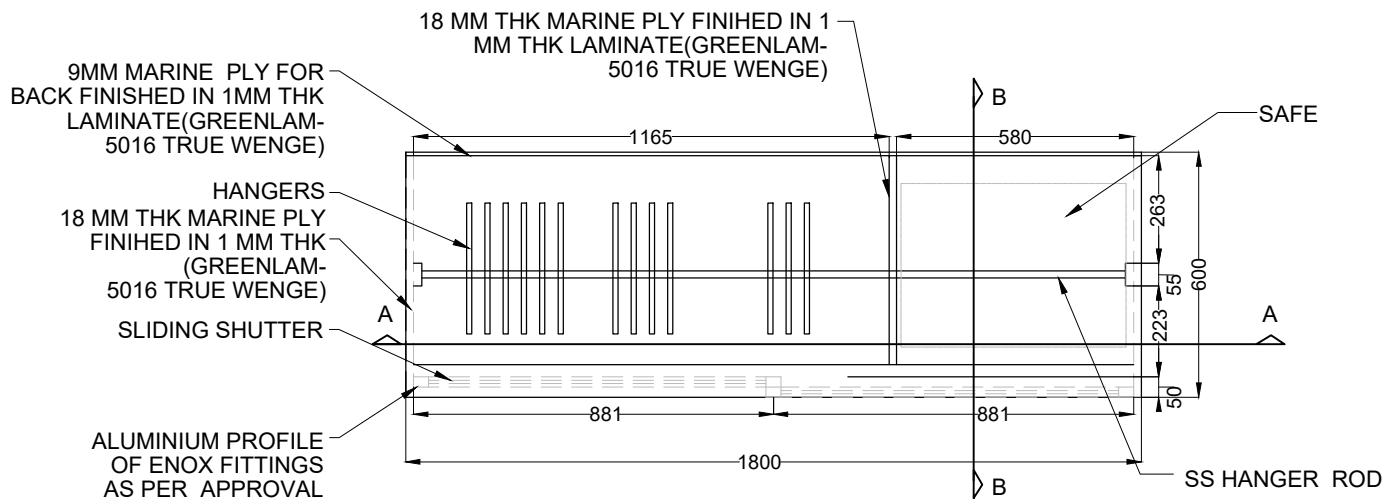


PLAN OF WARDROBE ^A
SCALE=1:20

NOTES:


1. DRAWINGS SHALL NOT BE SCALED.
2. ALL DIMENSIONS ARE IN MM.
3. ANY DISCREPANCY IN DRAWINGS AND EXISTING CONDITIONS SHOULD BE BROUGHT TO THE NOTICE OF THE ARCHITECT PRIOR TO PROCEEDING WITH THE ITEM
4. FOR SIZE OF STRUCTURAL MEMBERS REFER STRUCTURAL ENGINEER'S DRAWINGS.
5. ALL DOOR & WINDOW DIMENSIONS LISTED IN SCHEDULES MUST BE VERIFIED WITH SITE CONDITIONS BEFORE FABRICATION.
6. ALL DOOR AND WINDOW DIMENSIONS ARE MASONARY DIMENSIONS
- 7.CORELATE STRUCTURAL & ARCHITECT'S DWGS. AND GET BACK TO ARCHITECT WITH DISCREPANCIES IF ANY.

una

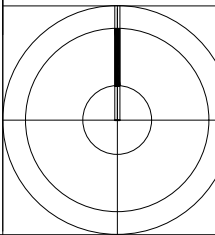


1	12.08.2022	ISSUE FOR TENDER PRUPOSE
No.	DATE	ISSUE/ REVISION
I I T BOMBAY: VANVIHAR GUEST HOUSE		
POWAI, MUMBAI - 400 076, INDIA		
UPENDRA NAYAK & ASSOCIATES		
ARCHITECTS. INTERIOR DESIGNERS		
1, SULBHA NIWAS. DILIP GUPTA MARG. MAHIM. MUMBAI 400016		
TEL: 24458473 FAX:24446223		
DATE: 21.02.22	SCALE: AS NOTED	DRAWN BY: HR
CHECKED BY: AN		


A10

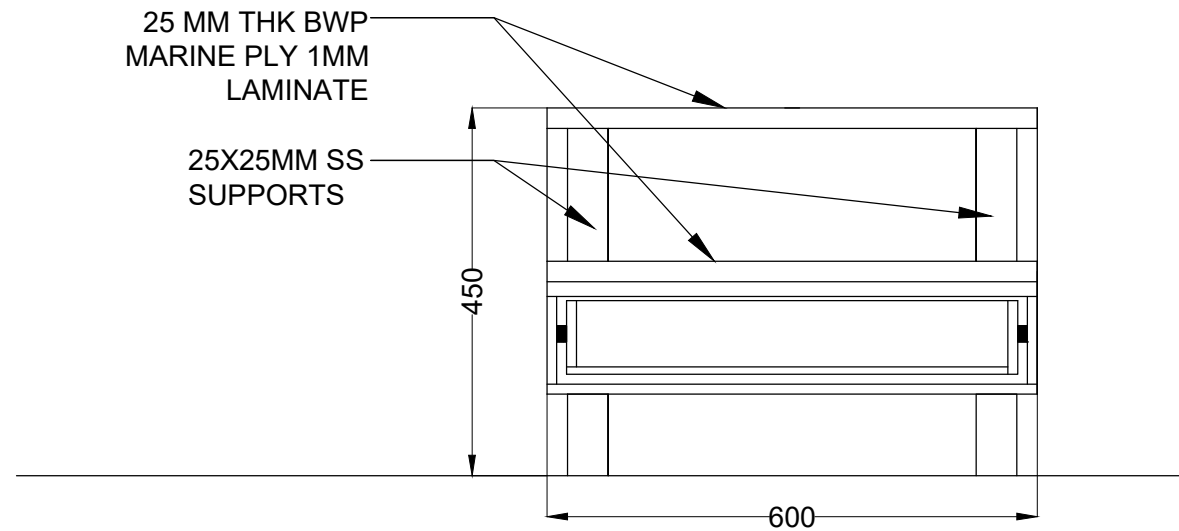


SECTION A-A'
SCALE= 1:10 (B)

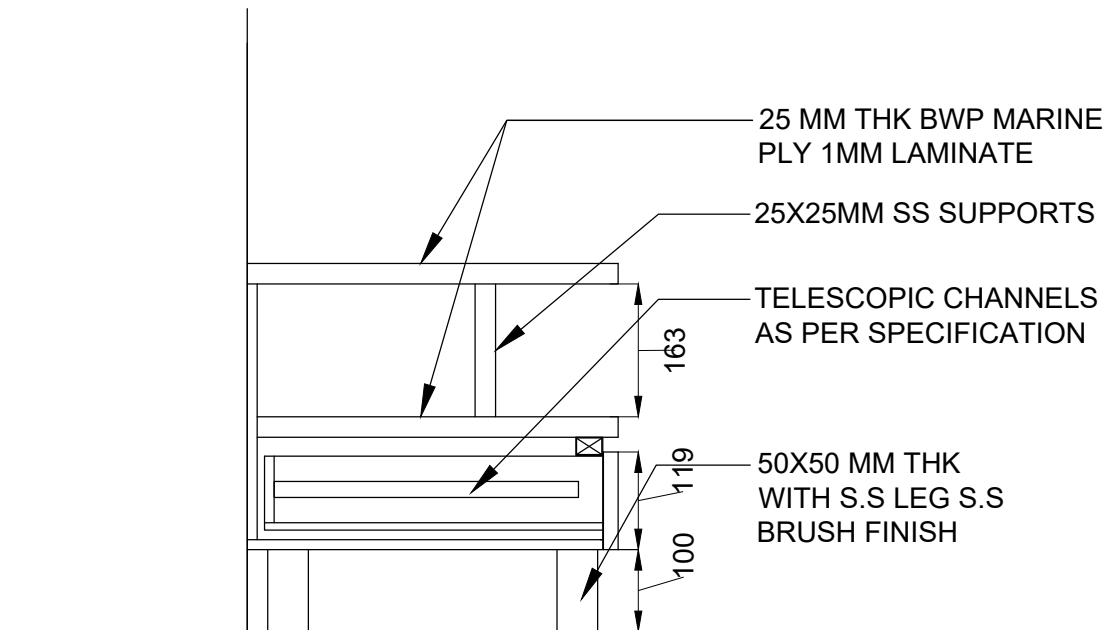

SECTION B-B'
SCALE= 1:10 (C)

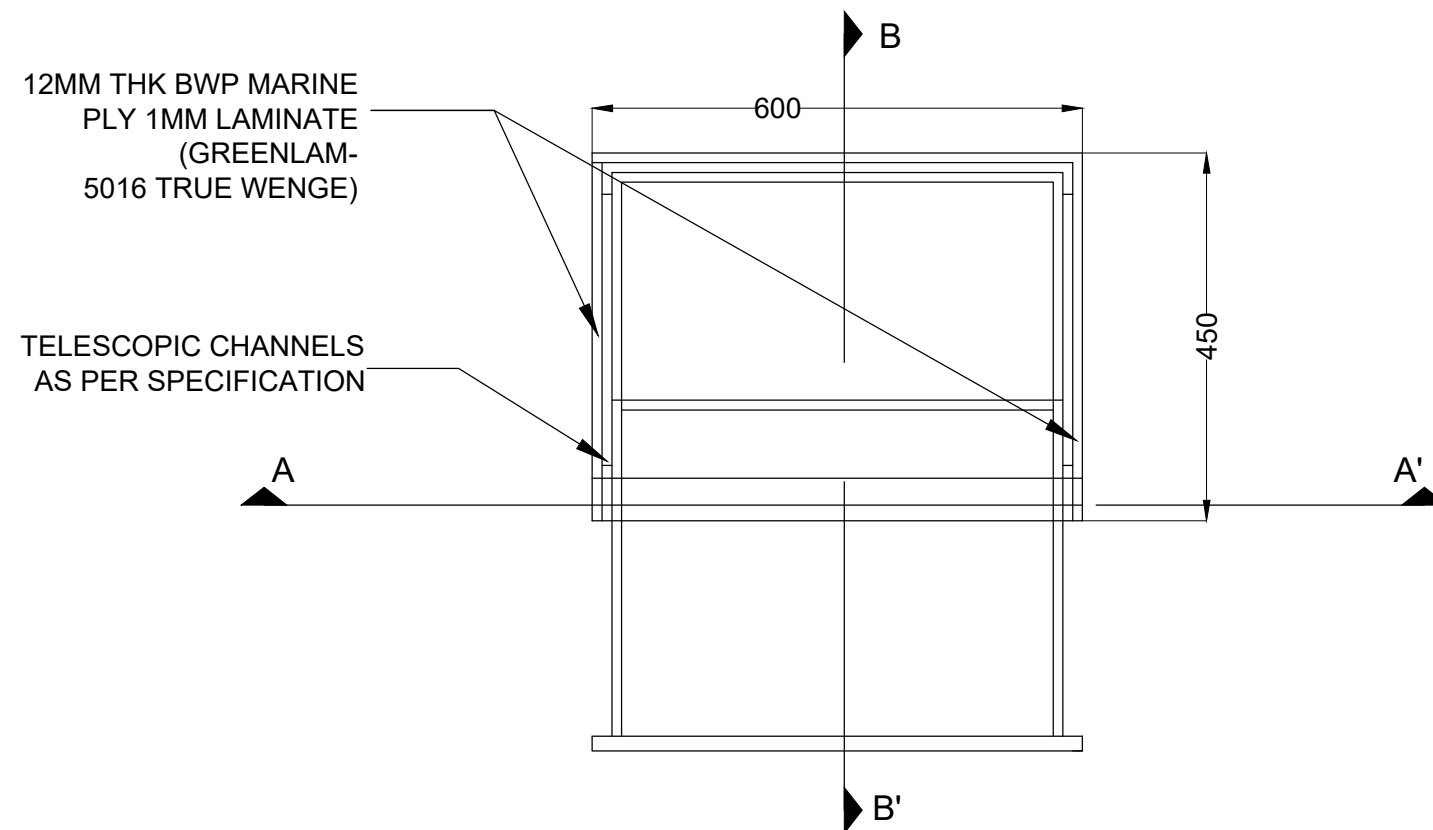


PLAN OF SIDE TABLE
SCALE=1:10 (A)

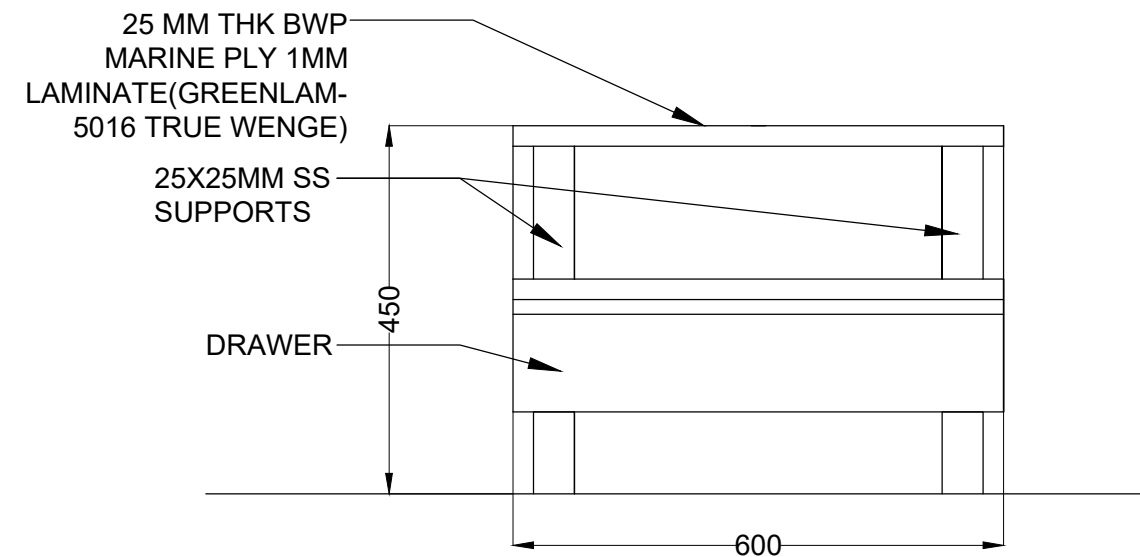


FRONT ELEVATION
SCALE= 1:10 (D)


NOTES:

1. DRAWINGS SHALL NOT BE SCALED.
2. ALL DIMENSIONS ARE IN MM.
3. ANY DISCREPANCY IN DRAWINGS AND EXISTING CONDITIONS SHOULD BE BROUGHT TO THE NOTICE OF THE ARCHITECT PRIOR TO PROCEEDING WITH THE ITEM
4. FOR SIZE OF STRUCTURAL MEMBERS REFER STRUCTURAL ENGINEER'S DRAWINGS.
5. ALL DOOR & WINDOW DIMENSIONS LISTED IN SCHEDULES MUST BE VERIFIED WITH SITE CONDITIONS BEFORE FABRICATION.
6. ALL DOOR AND WINDOW DIMENSIONS ARE MASONARY DIMENSIONS
7. CORELATE STRUCTURAL & ARCHITECT'S DWGS. AND GET BACK TO ARCHITECT WITH DISCREPANCIES IF ANY.

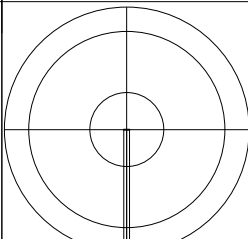
una			
	1	12.08.2022	ISSUE FOR TENDER PURPOSE
	No.	DATE	ISSUE/ REVISION
	I I T BOMBAY: VANVIHAR GUEST HOUSE		
	POWAI, MUMBAI - 400 076, INDIA		
	UPENDRA NAYAK & ASSOCIATES		
	ARCHITECTS. INTERIOR DESIGNERS		
	1, SULBHA NIWAS. DILIP GUPTA MARG. MAHIM. MUMBAI 400016 TEL: 24458473 FAX:24446223		
	DATE: 21.02.2022	SCALE: AS NOTED	DRAWN BY:HR CHECKED BY:AN
			A11

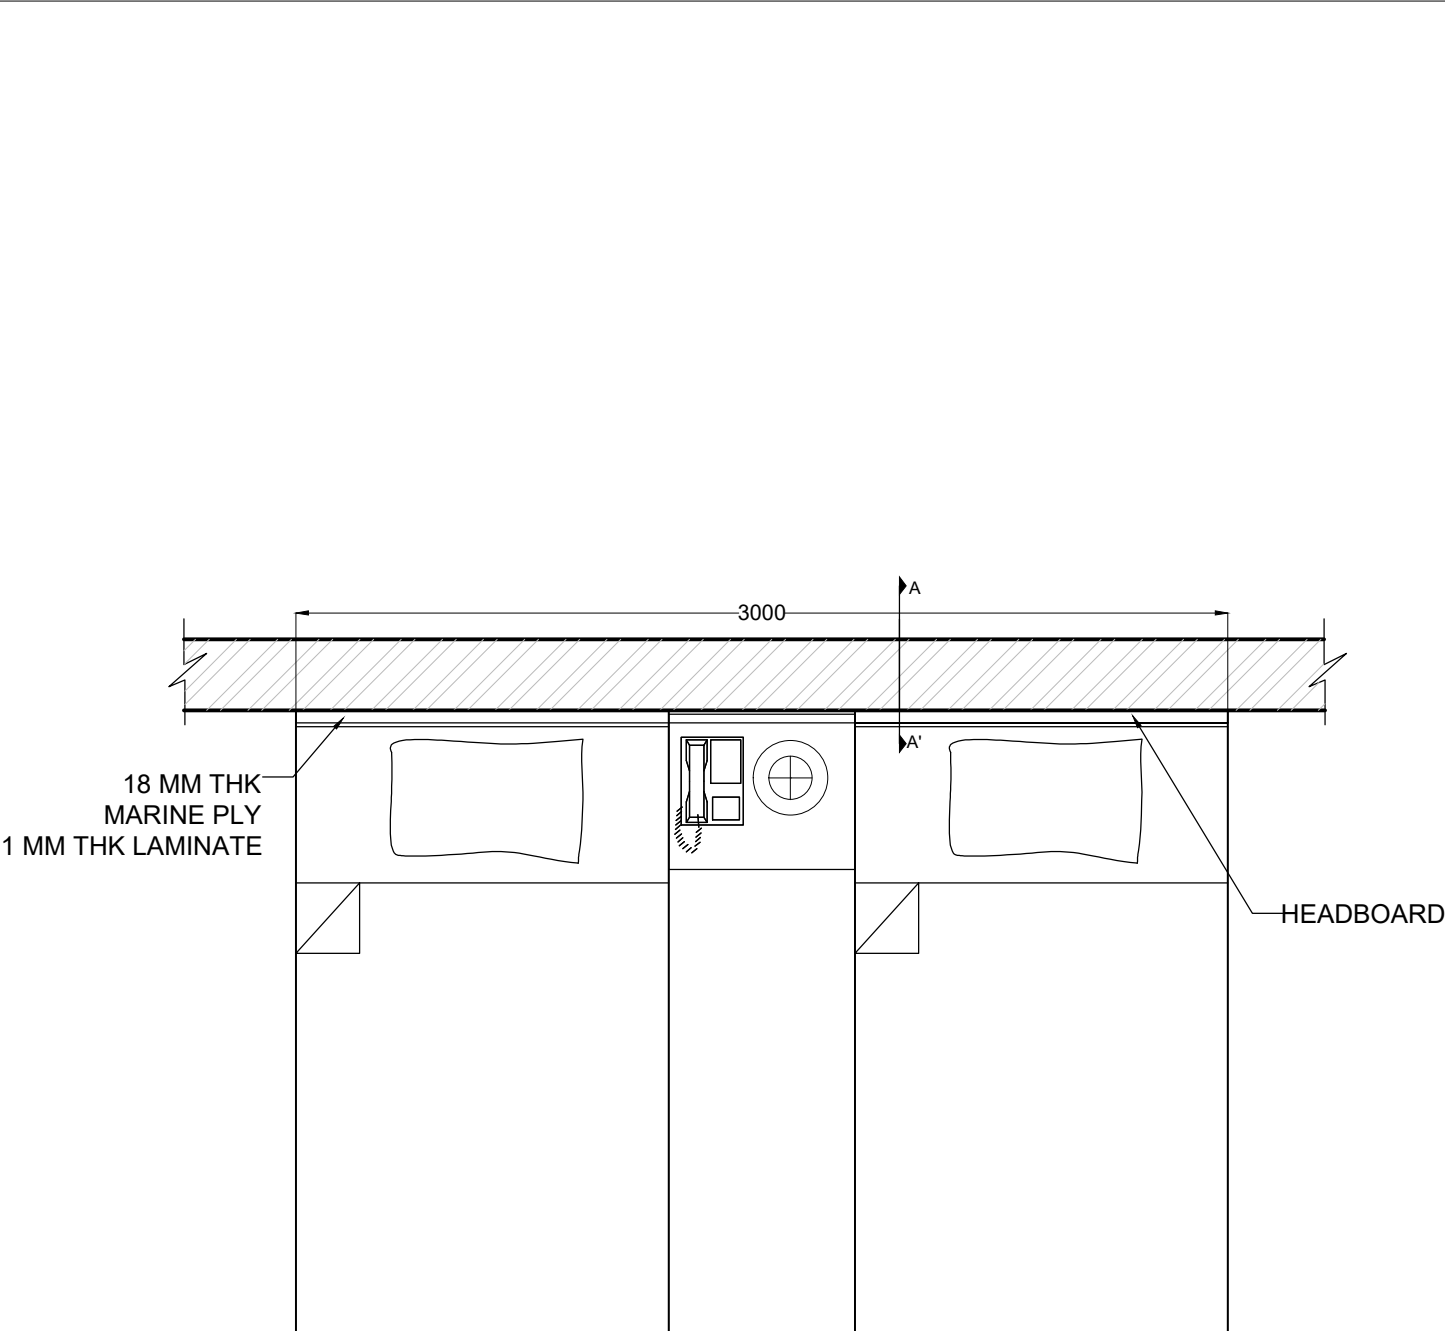

PLAN OF HEADBOARD (A)
SCALE=1:25

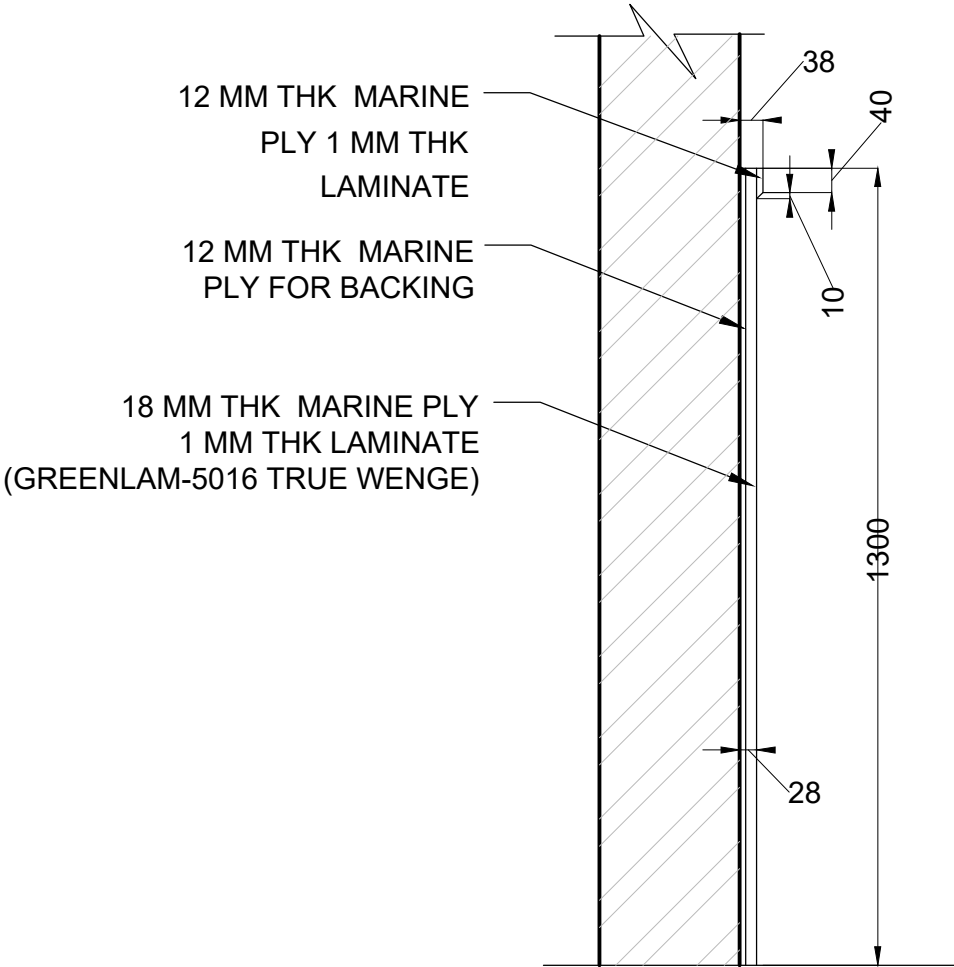

SECTION A-A' (B)
SCALE= 1:20

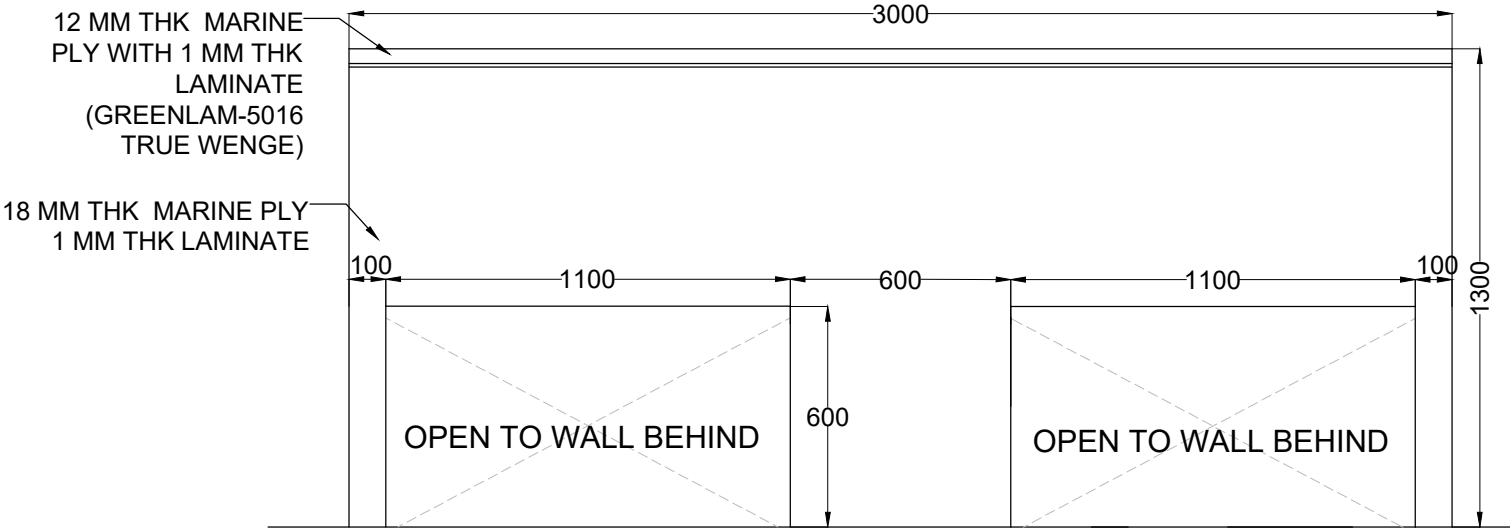


FRONT ELEVATION (C)
SCALE= 1:25


NOTES:

1. DRAWINGS SHALL NOT BE SCALED.
2. ALL DIMENSIONS ARE IN MM.
3. ANY DISCREPANCY IN DRAWINGS AND EXISTING CONDITIONS SHOULD BE BROUGHT TO THE NOTICE OF THE ARCHITECT PRIOR TO PROCEEDING WITH THE ITEM
4. FOR SIZE OF STRUCTURAL MEMBERS REFER STRUCTURAL ENGINEER'S DRAWINGS.
5. ALL DOOR & WINDOW DIMENSIONS LISTED IN SCHEDULES MUST BE VERIFIED WITH SITE CONDITIONS BEFORE FABRICATION.
6. ALL DOOR AND WINDOW DIMENSIONS ARE MASONARY DIMENSIONS
7. CORELATE STRUCTURAL & ARCHITECT'S DWGS. AND GET BACK TO ARCHITECT WITH DISCREPANCIES IF ANY.

una

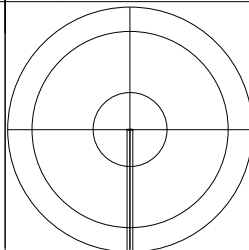

1	12.08.22	ISSUE FOR TENDER PURPOSE
No.	DATE	ISSUE/ REVISION
<u>I I T BOMBAY: VANVIHAR GUEST HOUSE</u>		
POWAI, MUMBAI - 400 076, INDIA		
UPENDRA NAYAK & ASSOCIATES		A12
ARCHITECTS. INTERIOR DESIGNERS		
1, SULBHA NIWAS. DILIP GUPTA MARG. MAHIM. MUMBAI 400016		
TEL: 24458473 FAX:24446223		
DATE: 21.02.2022	SCALE: AS NOTED	DRAWN BY:HR CHECKED BY:AN

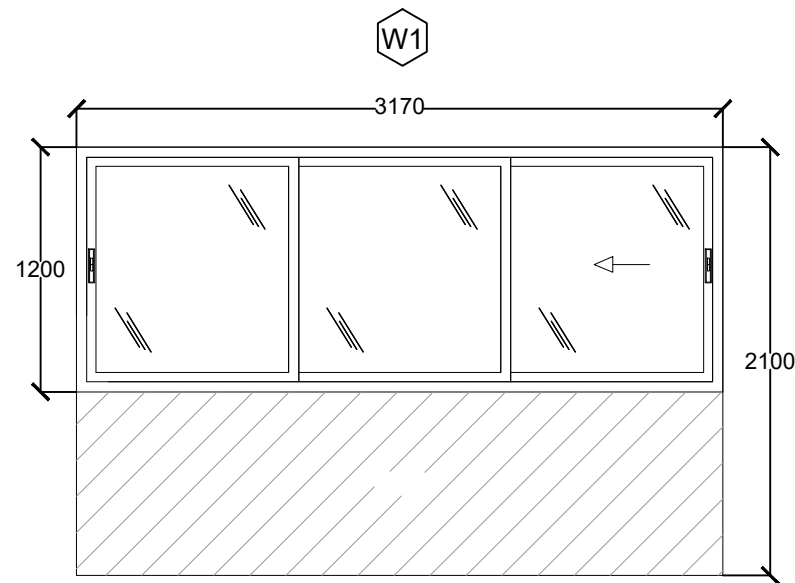


SLIDING WINDOW

WINDOW SCHEDULE OF VANVIHAR GUEST HOUSE						
SR. NO.	TYPE	NOS.	SIZE	SILL LVL.	LINTEL LVL.	DESCRIPTION
1	GUEST HOUSE TYPICAL ROOM					
1	W1	1	(3.17 x 1.2)	0.90	2.1	CASEMENT WINDOW IN UPVC SECTION WITH SLIDING WINDOW AND 6MM THICK SAINT GOBAIN CLEAR GLASS


NOTES:

- DRAWINGS SHALL NOT BE SCALED.
- ALL DIMENSIONS ARE IN MM.
- ANY DISCREPANCY IN DRAWINGS AND EXISTING CONDITIONS SHOULD BE BROUGHT TO THE NOTICE OF THE ARCHITECT PRIOR TO PROCEEDING WITH THE ITEM
- FOR SIZE OF STRUCTURAL MEMBERS REFER STRUCTURAL ENGINEER'S DRAWINGS.
- ALL DOOR & WINDOW DIMENSIONS LISTED IN SCHEDULES MUST BE VERIFIED WITH SITE CONDITIONS BEFORE FABRICATION.
- ALL DOOR AND WINDOW DIMENSIONS ARE MASONARY DIMENSIONS
- CORELATE STRUCTURAL & ARCHITECT'S DWGS. AND GET BACK TO ARCHITECT WITH DISCREPANCIES IF ANY.

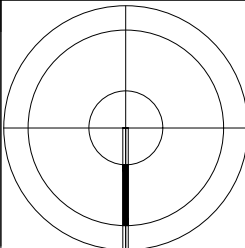			
	1	13.08.2022	ISSUE FOR TENDER PURPOSE
	No.	DATE	ISSUE/ REVISION
	<u>I I T BOMBAY: VANVIHAR GUEST HOUSE</u> POWAI, MUMBAI - 400 076, INDIA		
	UPENDRA NAYAK & ASSOCIATES ARCHITECTS. INTERIOR DESIGNERS 1, SULBHA NIWAS. DILIP GUPTA MARG. MAHIM. MUMBAI 400016 TEL: 24458473 FAX:24446223		A13
	DATE: 04.08.2022		
	SCALE: AS NOTED		DRAWN BY:HR




1. DRAWINGS SHALL NOT BE SCALED.
2. ALL DIMENSIONS ARE IN MM.
3. ANY DISCREPANCY IN DRAWINGS AND EXISTING CONDITIONS SHOULD BE BROUGHT TO THE NOTICE OF THE ARCHITECT PRIOR TO PROCEEDING WITH THE ITEM
4. FOR SIZE OF STRUCTURAL MEMBERS REFER STRUCTURAL ENGINEER'S DRAWINGS.
5. ALL DOOR & WINDOW DIMENSIONS LISTED IN SCHEDULES MUST BE VERIFIED WITH SITE CONDITIONS BEFORE FABRICATION.
6. ALL DOOR AND WINDOW DIMENSIONS ARE MASONRY DIMENSIONS
7. CORRELATE STRUCTURAL & ARCHITECT'S DWGS. AND GET BACK TO ARCHITECT WITH DISCREPANCIES IF ANY.

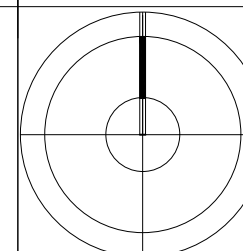

1	12.08.2022	ISSUE FOR TENDER PURPOSE	
No.	DATE	ISSUE/ REVISION	
<u>I I T BOMBAY: VANVIHAR GUEST HOUSE</u> POWAI, MUMBAI - 400 076, INDIA			
UPENDRA NAYAK & ASSOCIATES ARCHITECTS. INTERIOR DESIGNERS 1, SULBHA NIWAS. DILIP GUPTA MARG. MAHIM. MUMBAI 400016 TEL: 24458473 FAX:24446223		A14	
DATE: 21.02.2022	SCALE: AS NOTED		DRAWN BY:HR

A14

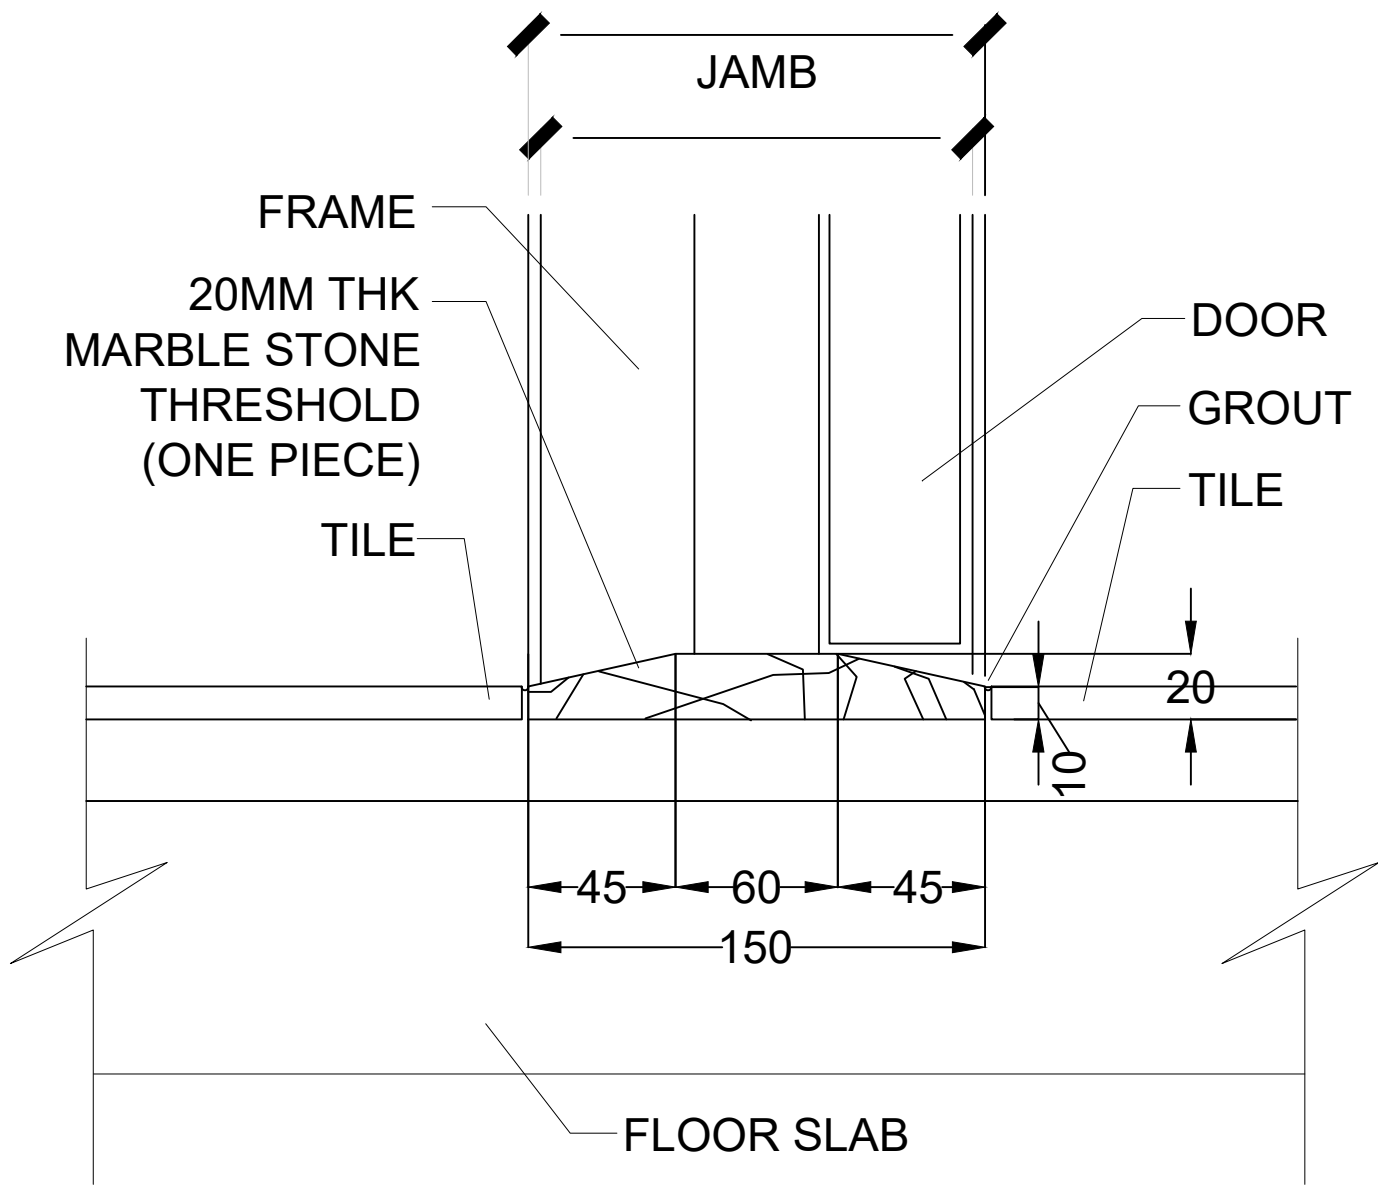


MAIN DOOR THRESHOLD DETAIL

MAIN DOOR THRESHOLD DETAIL DRAWING ^A
SCALE= 1:25


NOTES:

- 1. DRAWINGS SHALL NOT BE SCALED.
- 2. ALL DIMENSIONS ARE IN MM.
- 3. ANY DISCREPANCY IN DRAWINGS AND EXISTING CONDITIONS SHOULD BE BROUGHT TO THE NOTICE OF THE ARCHITECT PRIOR TO PROCEEDING WITH THE ITEM
- 4. FOR SIZE OF STRUCTURAL MEMBERS REFER STRUCTURAL ENGINEER'S DRAWINGS.
- 5. ALL DOOR & WINDOW DIMENSIONS LISTED IN SCHEDULES MUST BE VERIFIED WITH SITE CONDITIONS BEFORE FABRICATION.
- 6. ALL DOOR AND WINDOW DIMENSIONS ARE MASONARY DIMENSIONS
- 7.CORELATE STRUCTURAL & ARCHITECT'S DWGS. AND GET BACK TO ARCHITECT WITH DISCREPANCIES IF ANY.


una

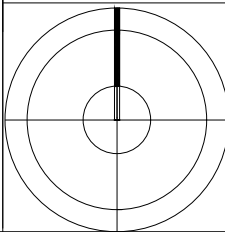


1	12.08.22	ISSUE FOR TENDER PURPOSE	
No.	DATE	ISSUE/ REVISION	
<u>I I T BOMBAY: VANVIHAR GUEST HOUSE</u>			
POWAI, MUMBAI - 400 076, INDIA			
UPENDRA NAYAK & ASSOCIATES ARCHITECTS. INTERIOR DESIGNERS 1, SULBHA NIWAS. DILIP GUPTA MARG. MAHIM. MUMBAI 400016 TEL: 24458473 FAX:24446223			A15
DATE: 04.08.2022	SCALE: AS NOTED	DRAWN BY: HR	

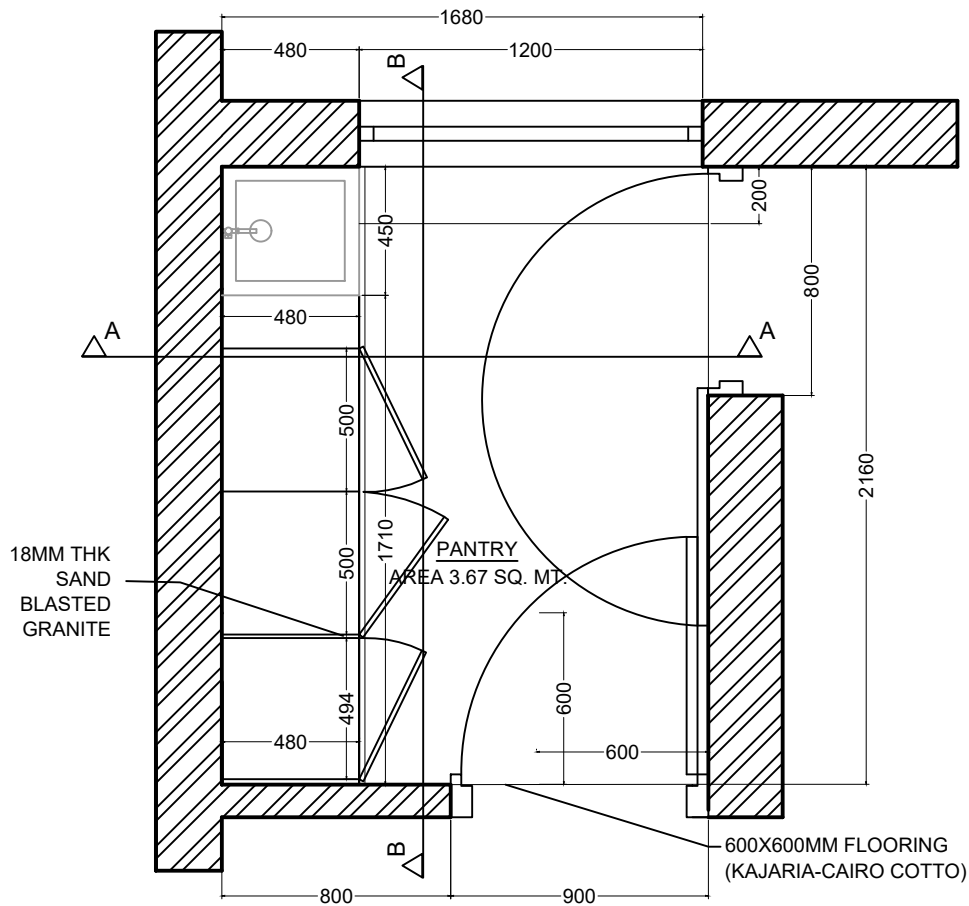

PANTRY PLAN
SCALE=1:25 (A)

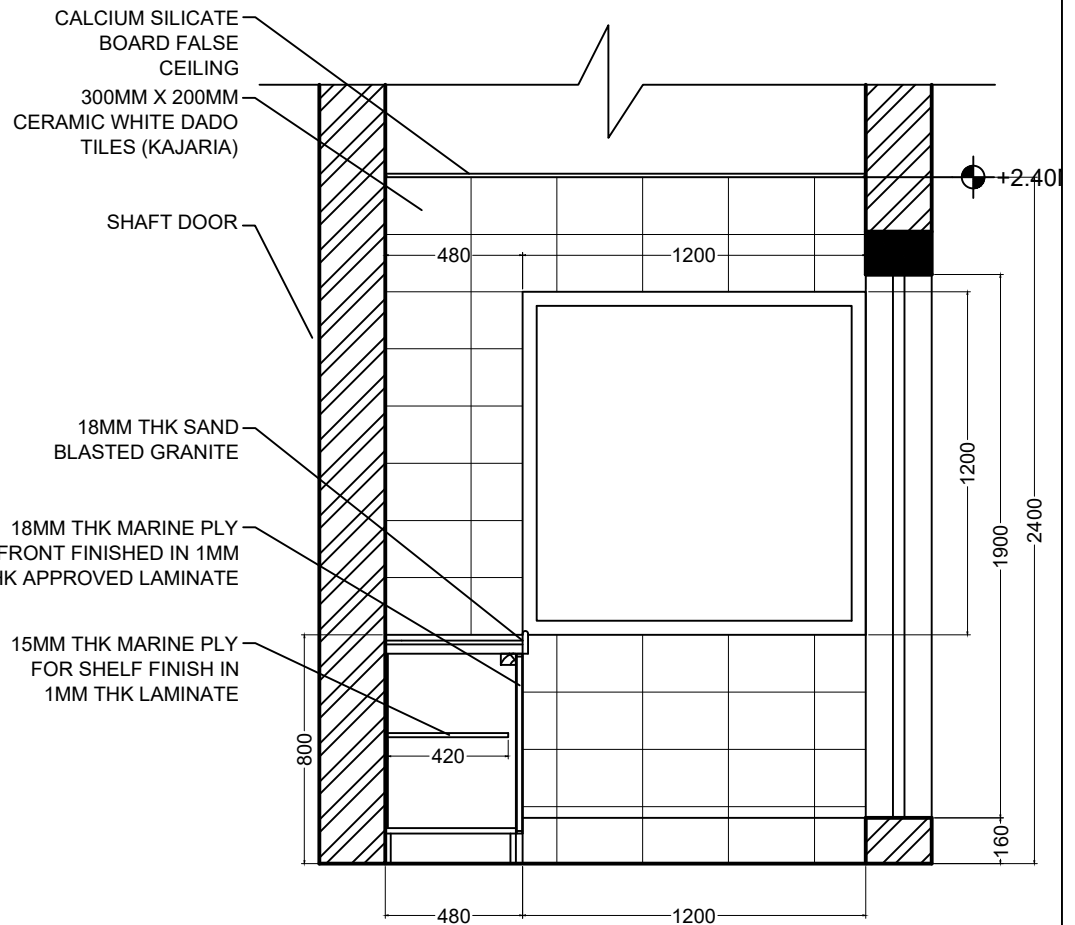


SECTION AA'
SCALE=1:25 (B)


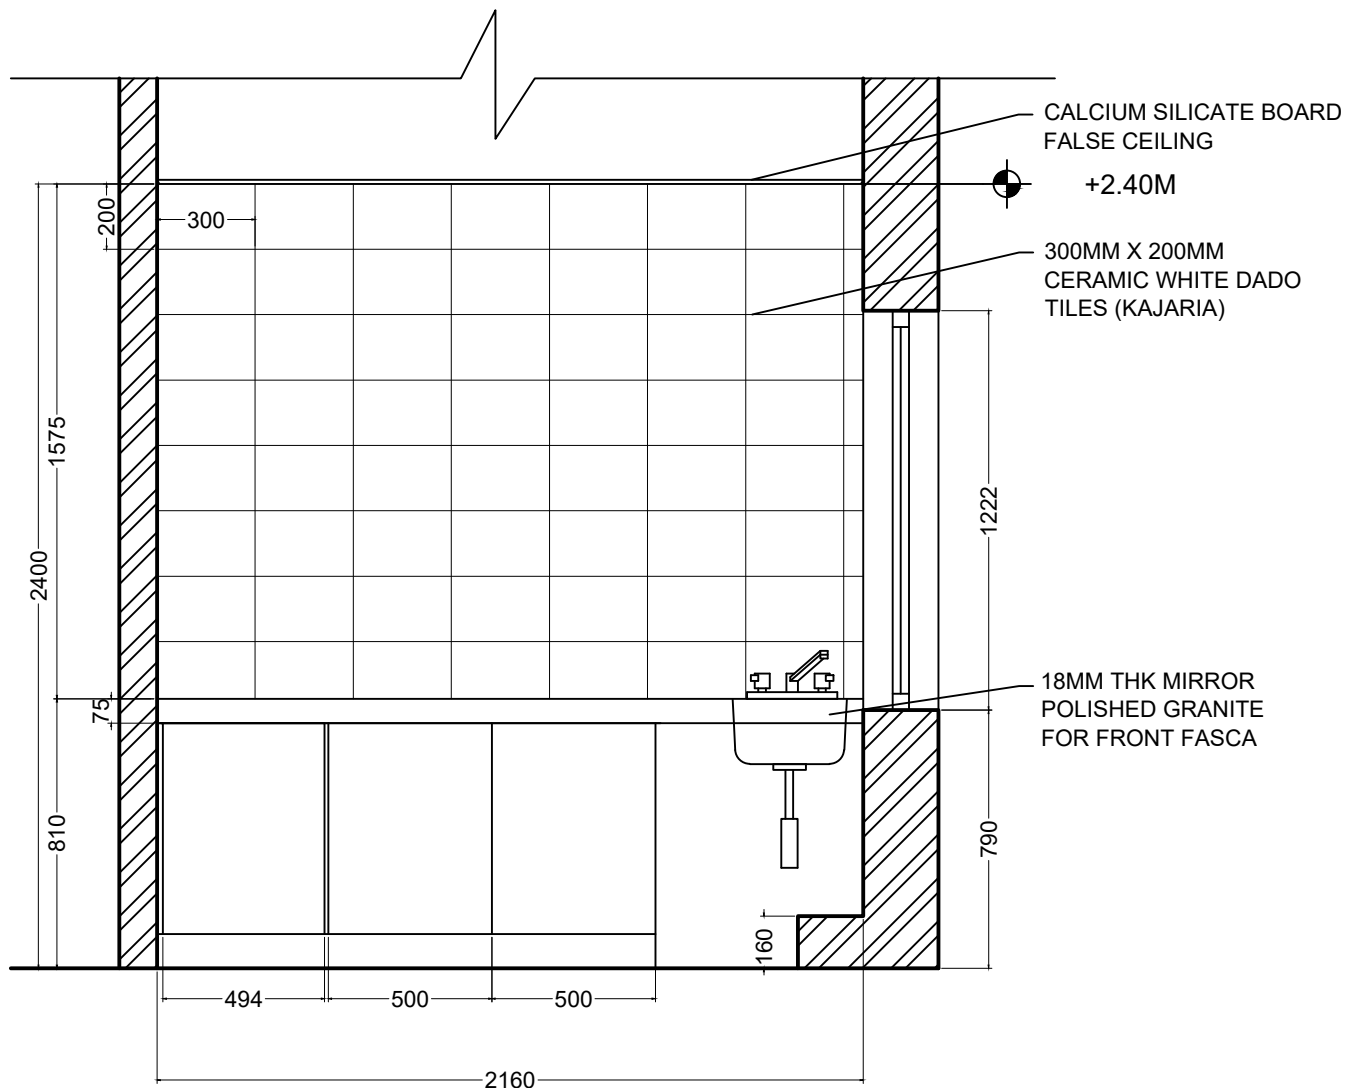


SECTION BB'
SCALE=1:25 (C)

NOTES:

- DRAWINGS SHALL NOT BE SCALED.
- ALL DIMENSIONS ARE IN MM.
- ANY DISCREPANCY IN DRAWINGS AND EXISTING CONDITIONS SHOULD BE BROUGHT TO THE NOTICE OF THE ARCHITECT PRIOR TO PROCEEDING WITH THE ITEM
- FOR SIZE OF STRUCTURAL MEMBERS REFER STRUCTURAL ENGINEER'S DRAWINGS.
- ALL DOOR & WINDOW DIMENSIONS LISTED IN SCHEDULES MUST BE VERIFIED WITH SITE CONDITIONS BEFORE FABRICATION.
- ALL DOOR AND WINDOW DIMENSIONS ARE MASONARY DIMENSIONS
- CORELATE STRUCTURAL & ARCHITECT'S DWGS. AND GET BACK TO ARCHITECT WITH DISCREPANCIES IF ANY.

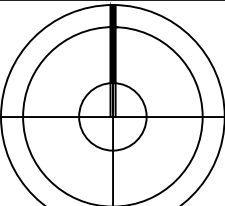
una	1	12.08.2022	ISSUE FOR TENDER PRUPOSE	
	No.	DATE	ISSUE/ REVISION	
	I I T BOMBAY: VANVIHAR GUEST HOUSE			
	POWAI, MUMBAI - 400 076, INDIA			
	UPENDRA NAYAK & ASSOCIATES			A16
	ARCHITECTS. INTERIOR DESIGNERS			
	1, SULBHA NIWAS, DILIP GUPTA MARG, MAHIM, MUMBAI 400016			
TEL: 24458473 FAX:24446223				
DATE: 21.02.22		SCALE: AS NOTED		DRAWN BY: HR

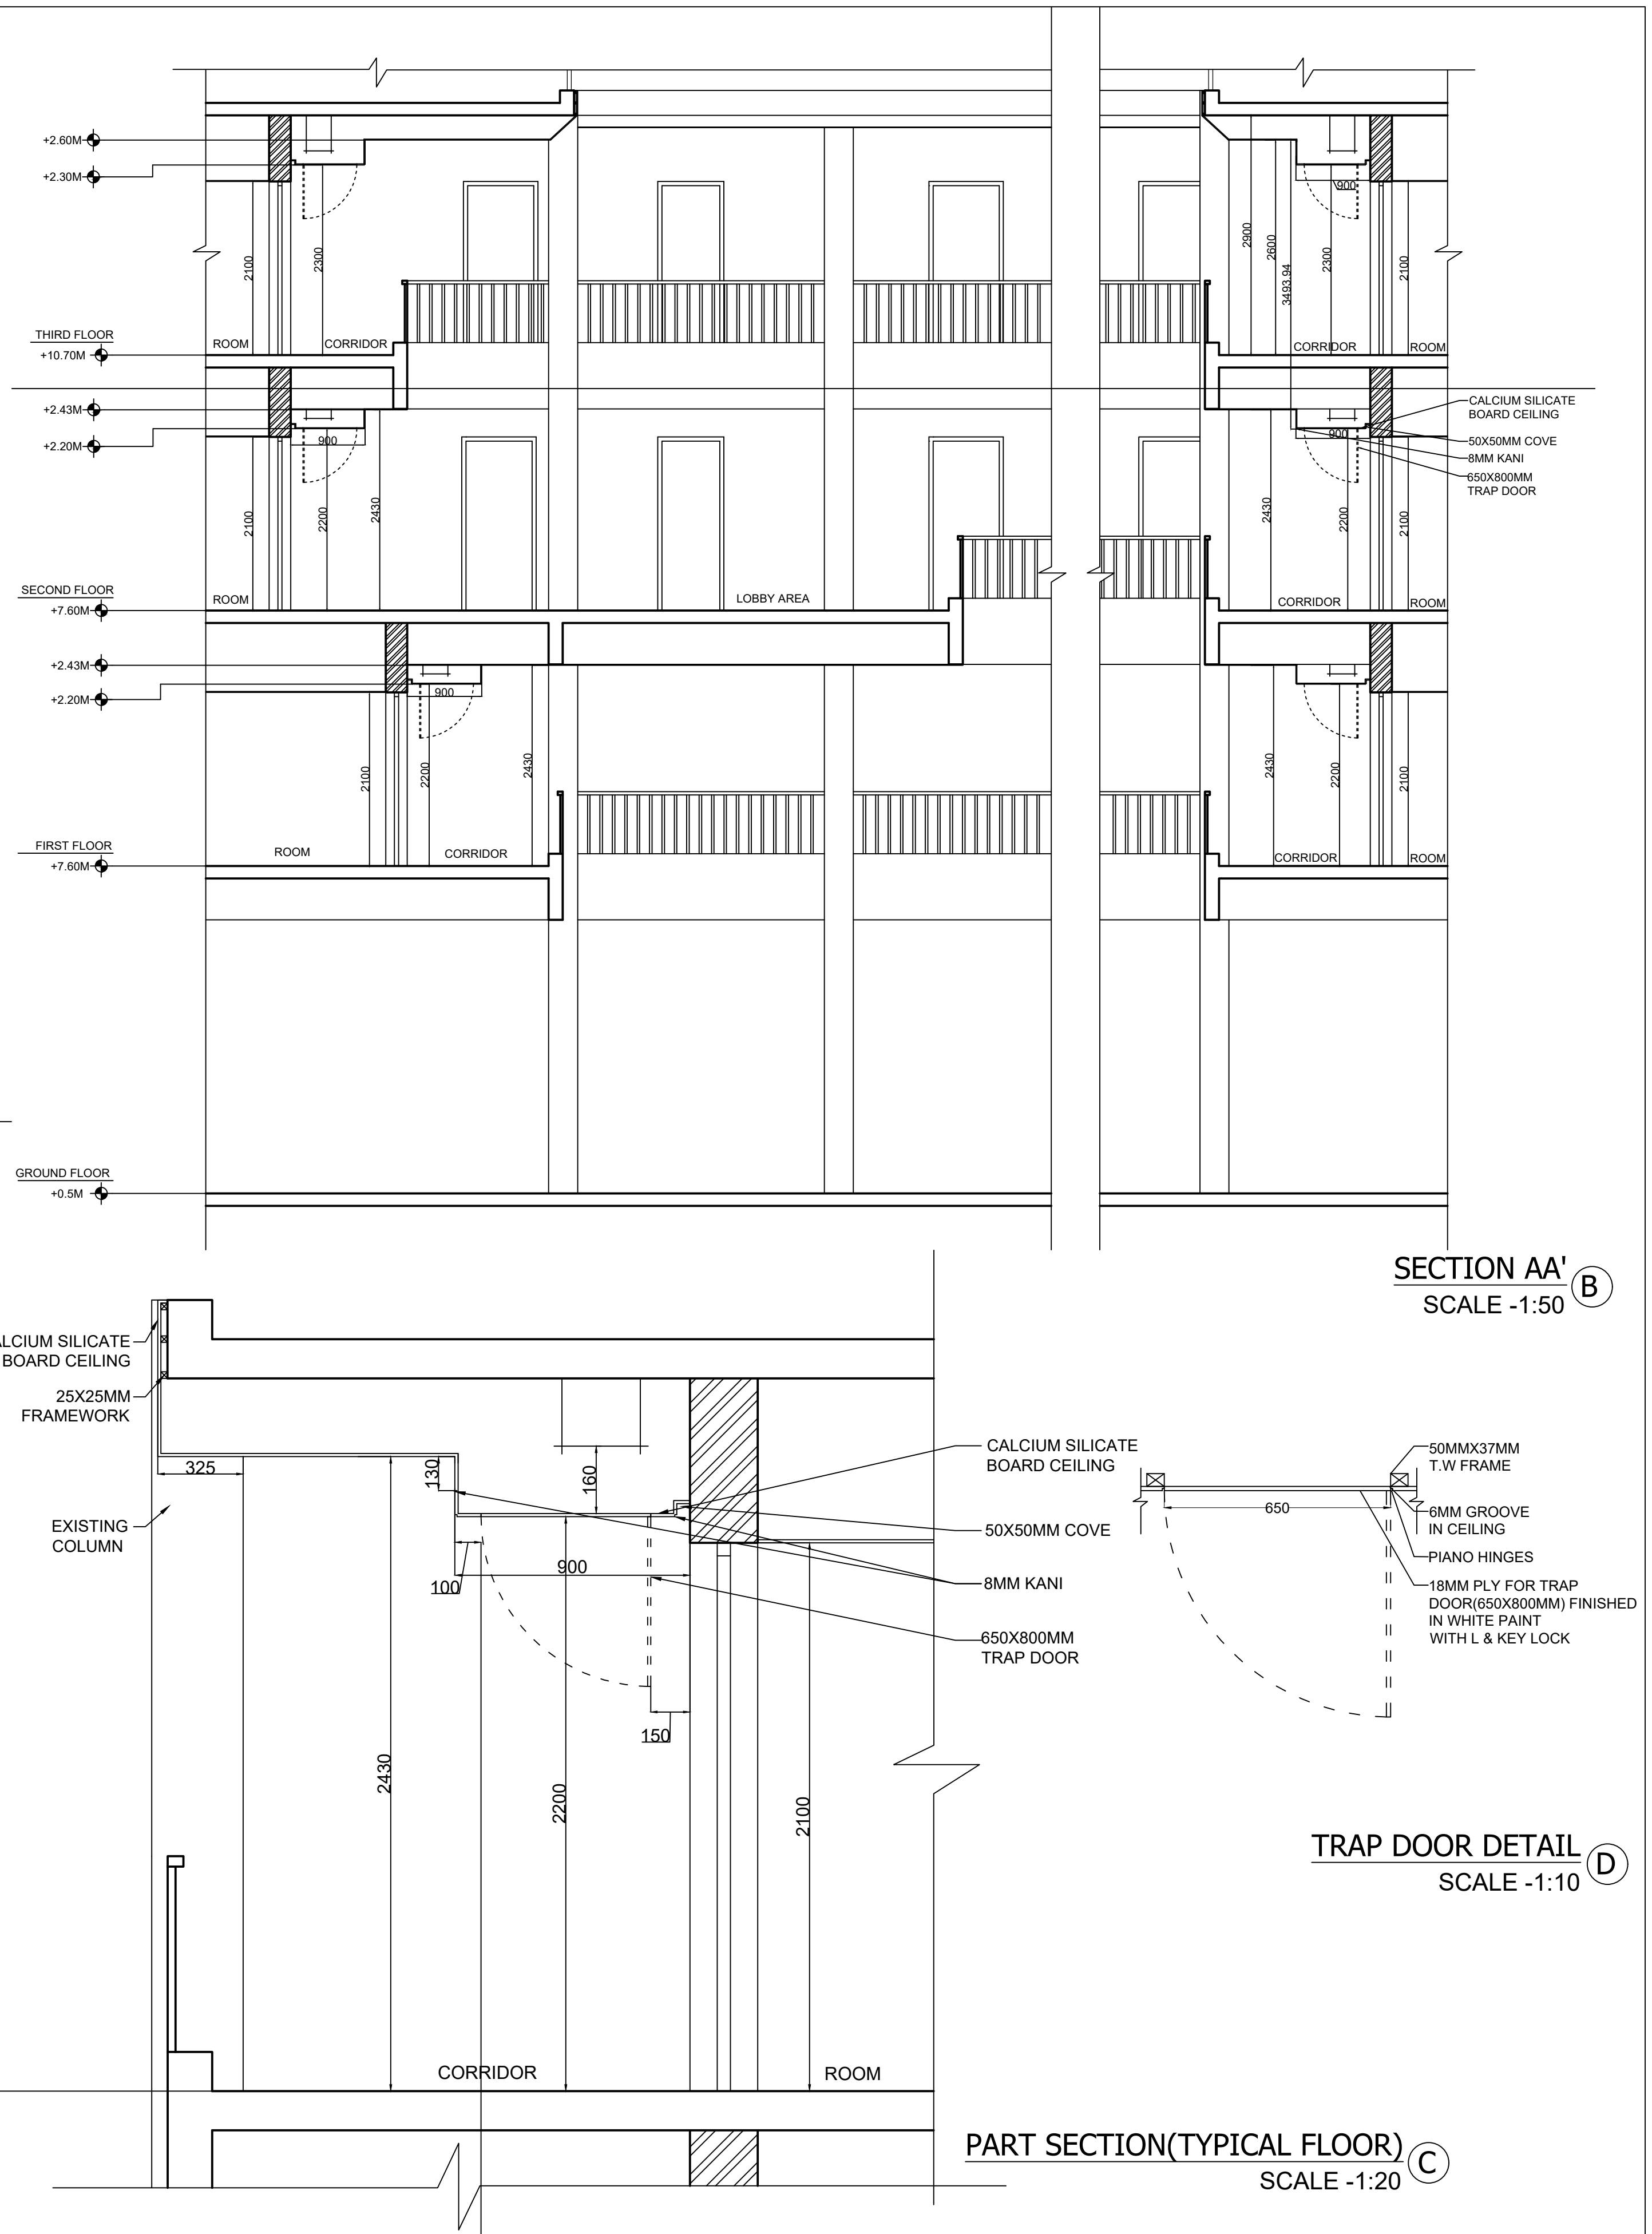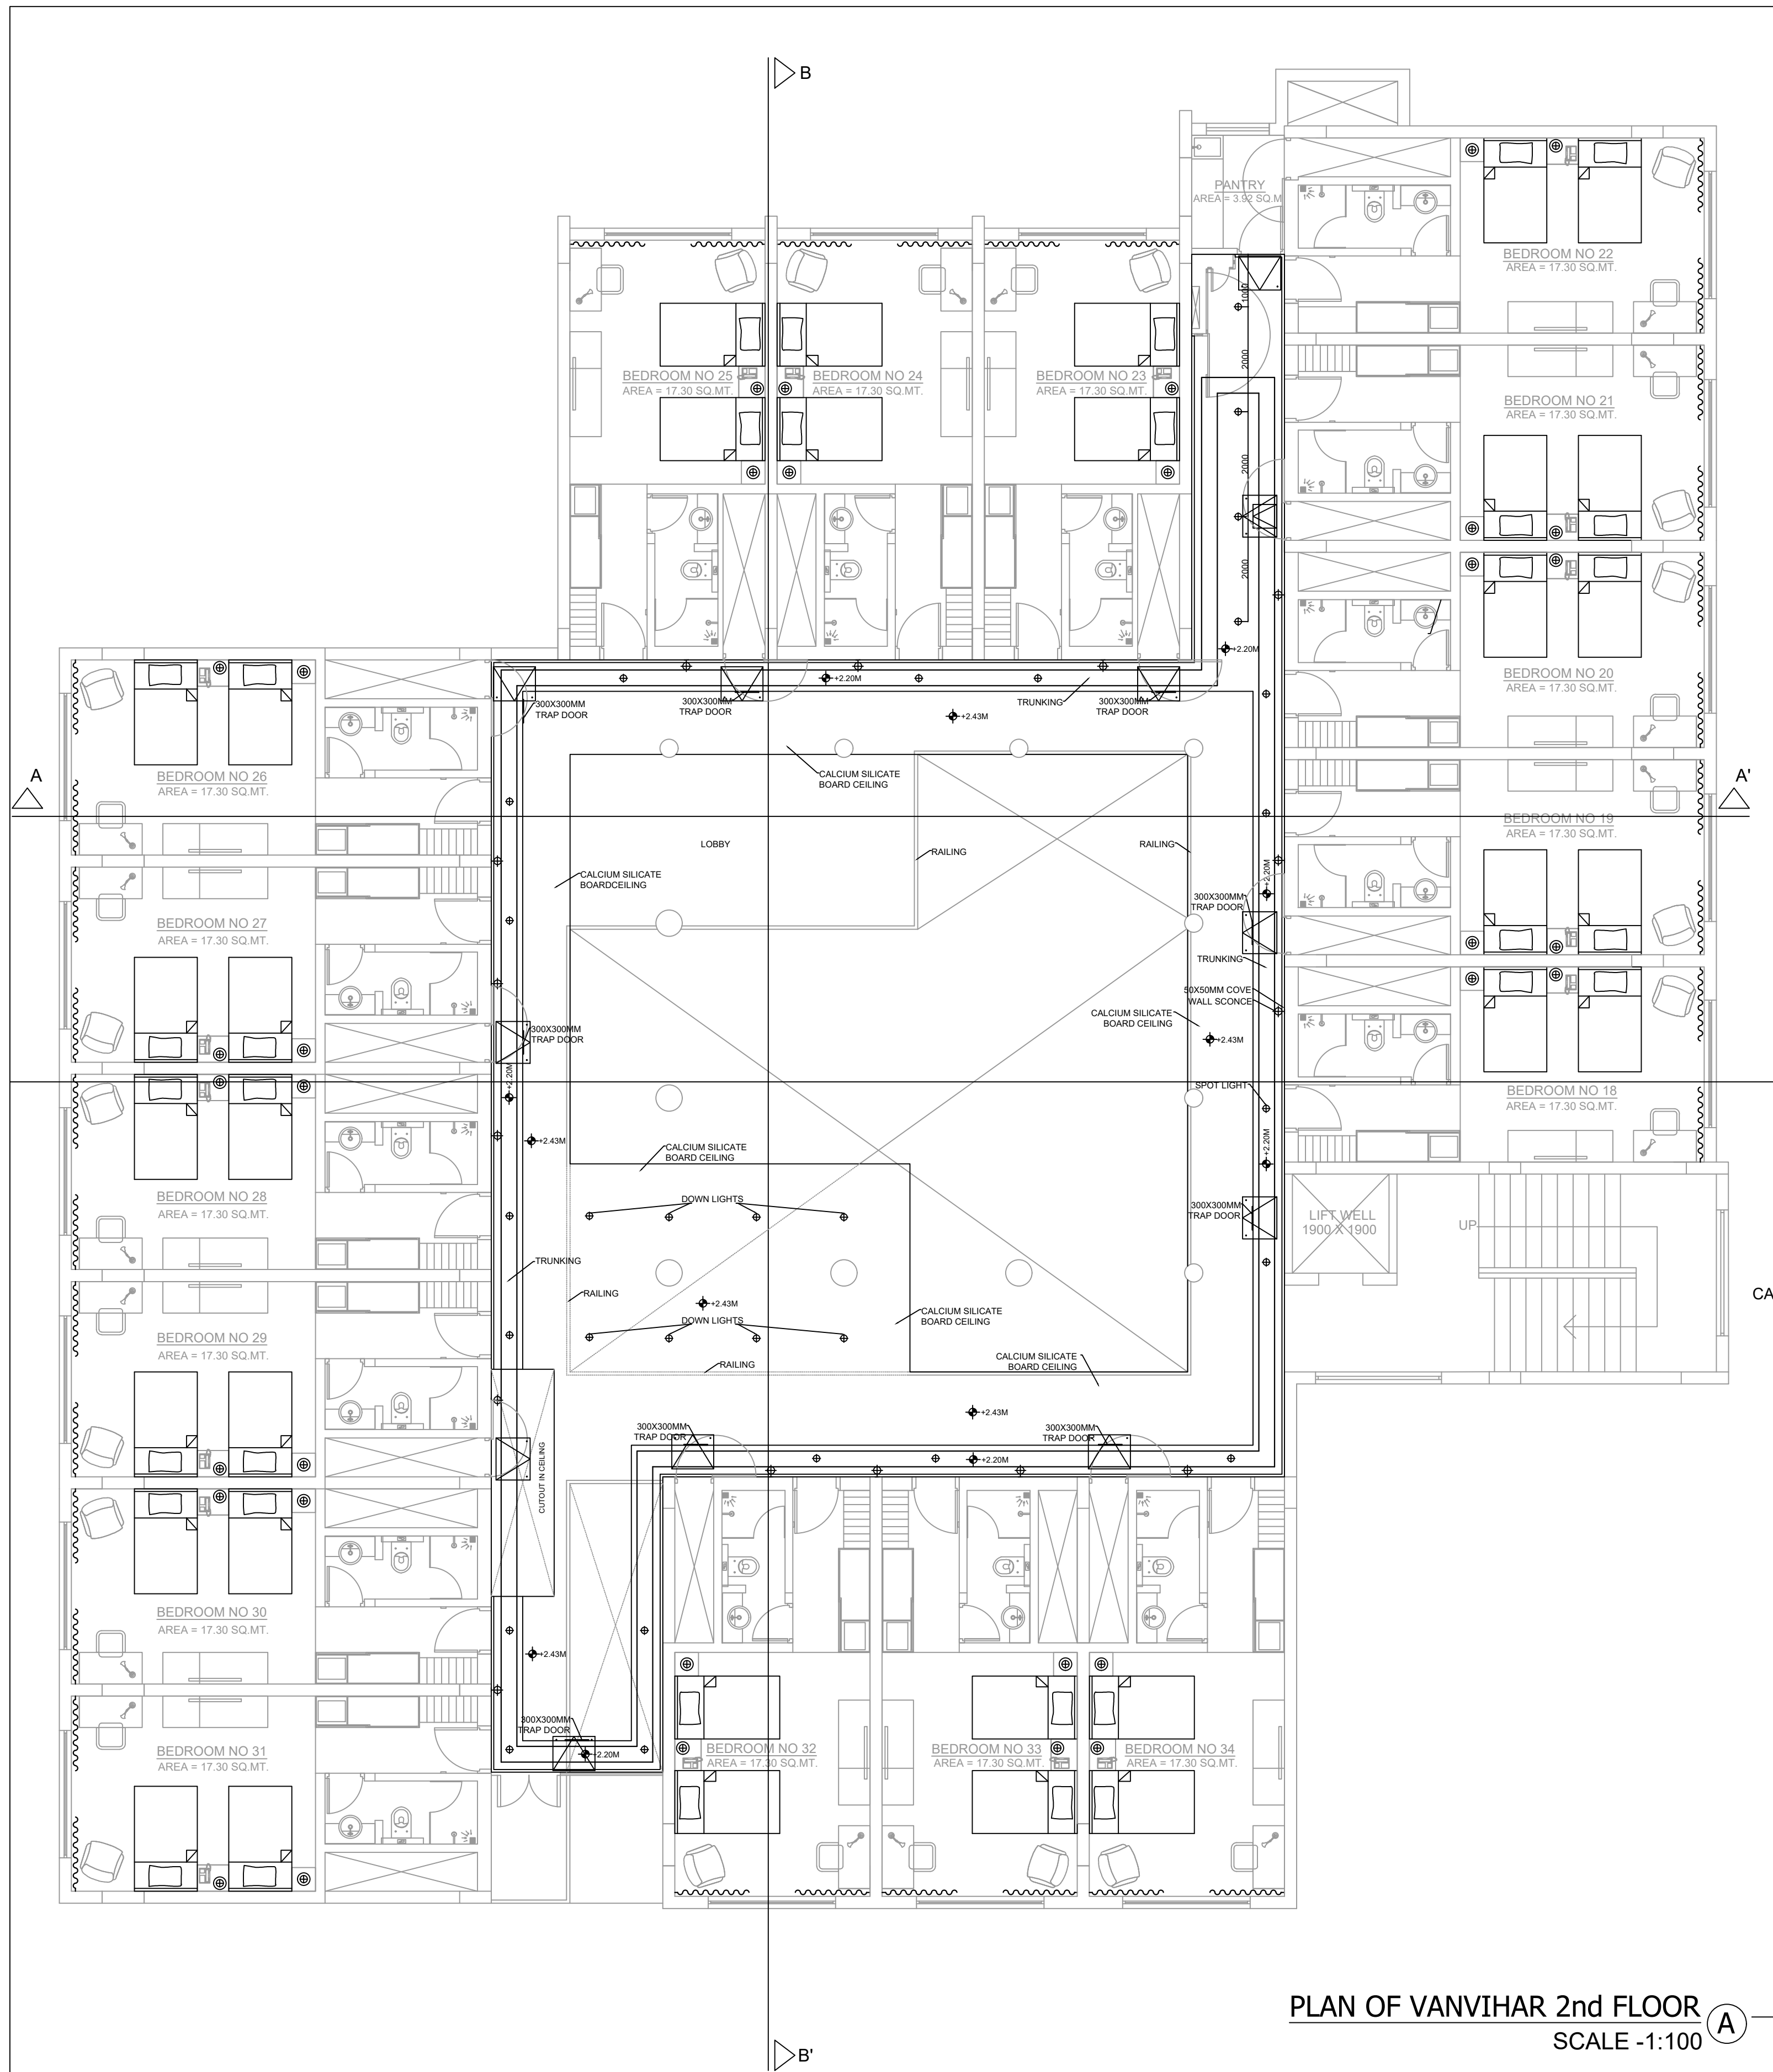

TRAP DOOR DETAIL (D)
SCALE -1:10


NOTES:

1. DRAWINGS SHALL NOT BE SCALED.
2. ALL DIMENSIONS ARE IN MM.
3. ANY DISCREPANCY IN DRAWINGS AND EXISTING CONDITIONS SHOULD BE BROUGHT TO THE NOTICE OF THE ARCHITECT PRIOR TO PROCEEDING WITH THE ITEM.
4. FOR SIZE OF STRUCTURAL MEMBERS REFER STRUCTURAL ENGINEER'S DRAWINGS.
5. ALL DOOR & WINDOW DIMENSIONS LISTED IN SCHEDULES MUST BE VERIFIED WITH SITE CONDITIONS BEFORE FABRICATION.
6. ALL DOOR AND WINDOW DIMENSIONS ARE MASONARY DIMENSIONS.
7. CORRELATE STRUCTURAL & ARCHITECT'S DWGS. AND GET BACK TO ARCHITECT WITH DISCREPANCIES IF ANY.

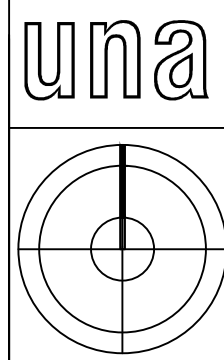

1	12.08.22	ISSUE FOR TENDER PURPOSE
NO.	DATE	ISSUE/REVISION
IIT BOMBAY: VANVIHAR GUEST HOUSE		
POWAI, MUMBAI-400 076, INDIA		
UPENDRA NAYAK & ASSOCIATES		
ARCHITECTS, INTERIOR DESIGNERS		
1, SUSHMA NIVAS, DILIP GUPTA MARG, MAHIM, MUMBAI-400016		
DATE:	21.02.2022	CHECKED BY: AN
SCALE:	AS NOTED	
DRAWN BY:	HR	


A17a

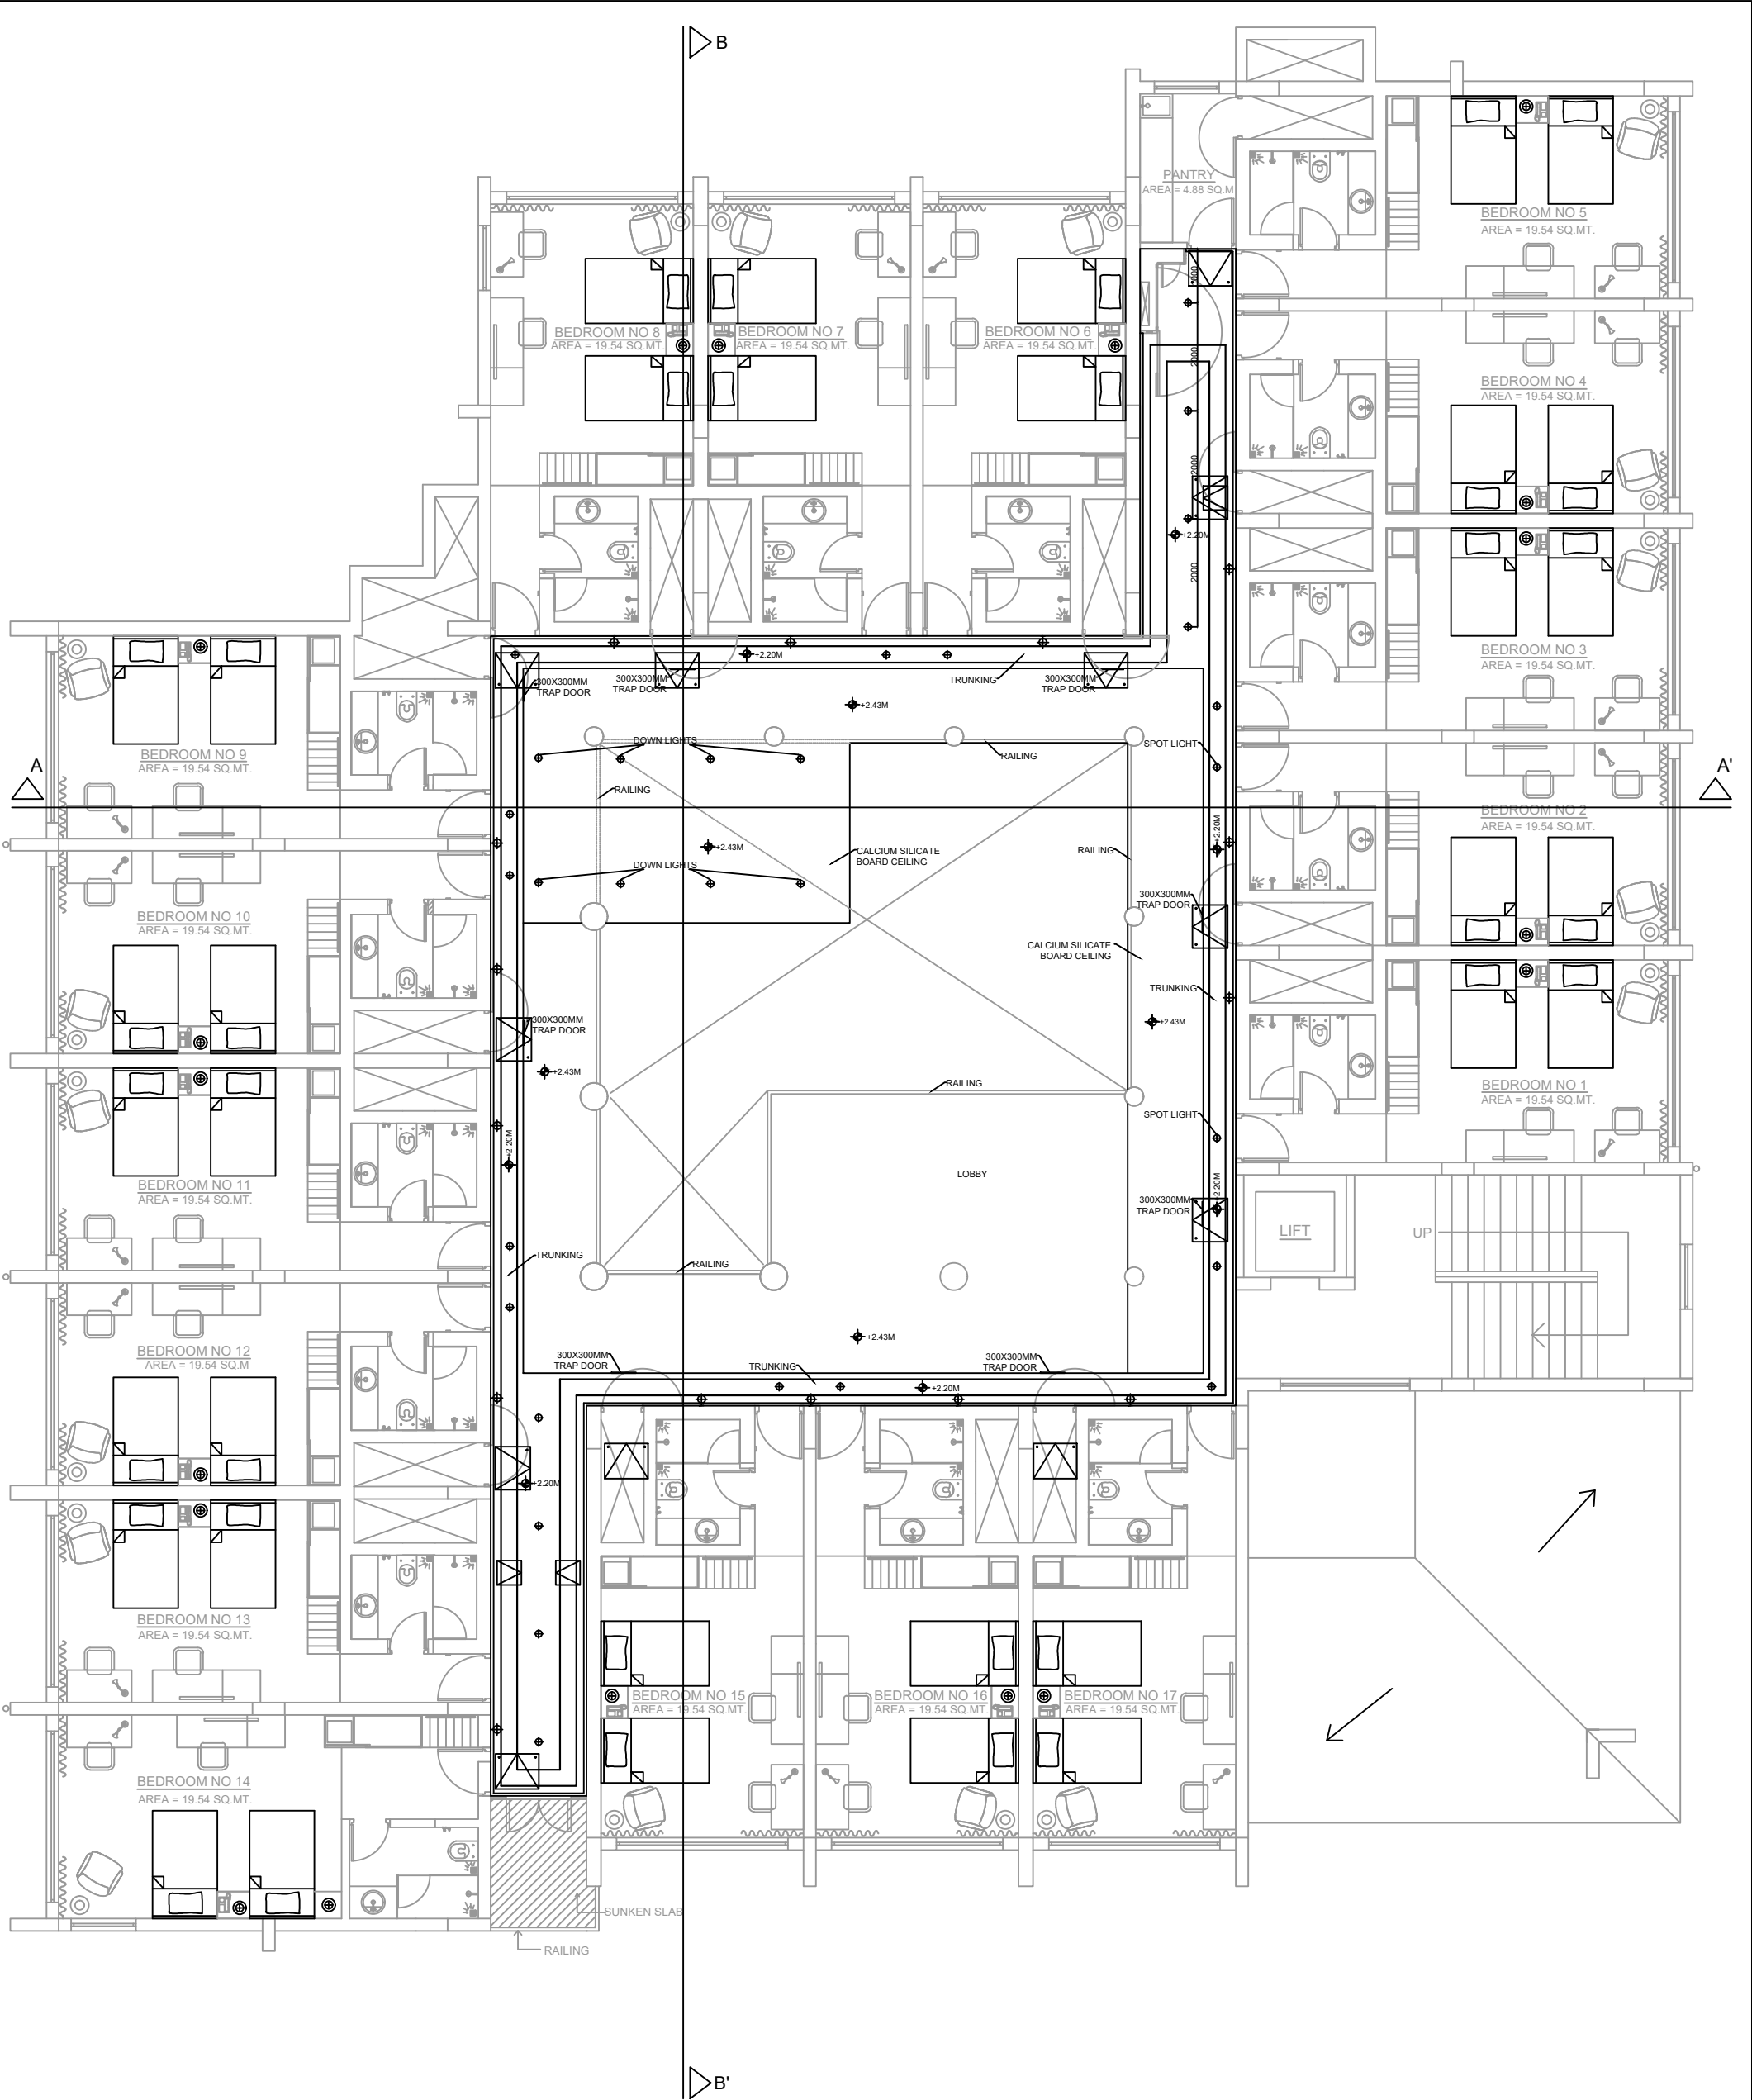

FIRST FLOOR PLAN
SCALE=1:500

NOTES:


1. DRAWINGS SHALL NOT BE SCALED.
2. ALL DIMENSIONS ARE IN MM.
3. ANY DISCREPANCY IN DRAWINGS AND EXISTING CONDITIONS SHOULD BE BROUGHT TO THE NOTICE OF THE ARCHITECT PRIOR TO PROCEEDING WITH THE ITEM
4. FOR SIZE OF STRUCTURAL MEMBERS REFER STRUCTURAL ENGINEER'S DRAWINGS.
5. ALL DOOR & WINDOW DIMENSIONS LISTED IN SCHEDULES MUST BE VERIFIED WITH SITE CONDITIONS BEFORE FABRICATION.
6. ALL DOOR AND WINDOW DIMENSIONS ARE MASONARY DIMENSIONS
7. CORELATE STRUCTURAL & ARCHITECT'S DWGS. AND GET BACK TO ARCHITECT WITH DISCREPANCIES IF ANY.

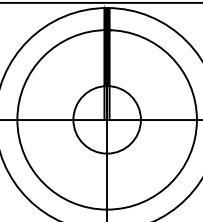	1	12.08.2022	CONCEPT DESIGN
	No.	DATE	ISSUE/ REVISION
	<u>I I T BOMBAY: VANVIHAR GUEST HOUSE</u>		
	POWAI, MUMBAI - 400 076, INDIA		
	UPENDRA NAYAK & ASSOCIATES		A17b
	ARCHITECTS. INTERIOR DESIGNERS		
	1, SULBHA NIWAS. DILIP GUPTA MARG. MAHIM. MUMBAI 400016 TEL: 24458473 FAX:24446223		
DATE: 21.02.22		SCALE: AS NOTED	DRAWN BY: HR




NOTES:

1. DRAWINGS SHALL NOT BE SCALED.
2. ALL DIMENSIONS ARE IN MM.
3. ANY DISCREPANCY IN DRAWINGS AND EXISTING CONDITIONS SHOULD BE BROUGHT TO THE NOTICE OF THE ARCHITECT PRIOR TO PROCEEDING WITH THE ITEM
4. FOR SIZE OF STRUCTURAL MEMBERS REFER STRUCTURAL ENGINEER'S DRAWINGS.
5. DOOR & WINDOW DIMENSIONS LISTED IN SCHEDULES MUST BE VERIFIED WITH SITE CONDITIONS BEFORE FABRICATION.
6. ALL DOOR AND WINDOW DIMENSIONS ARE MASONRY DIMENSIONS
7. CORRELATE STRUCTURAL & ARCHITECT'S DWGS. AND GET BACK TO ARCHITECT WITH DISCREPANCIES IF ANY.

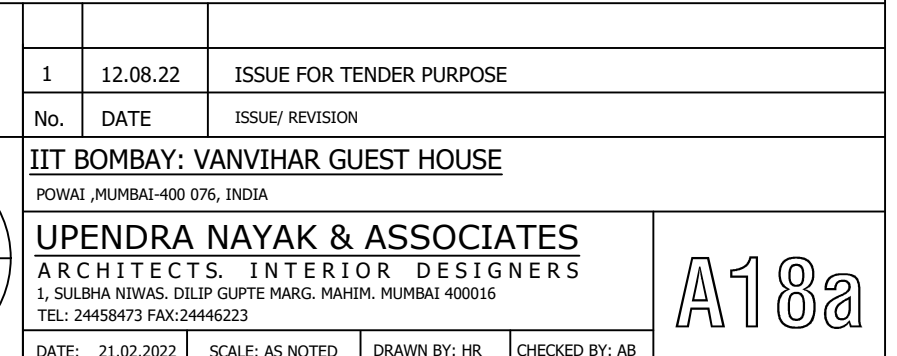


A18a

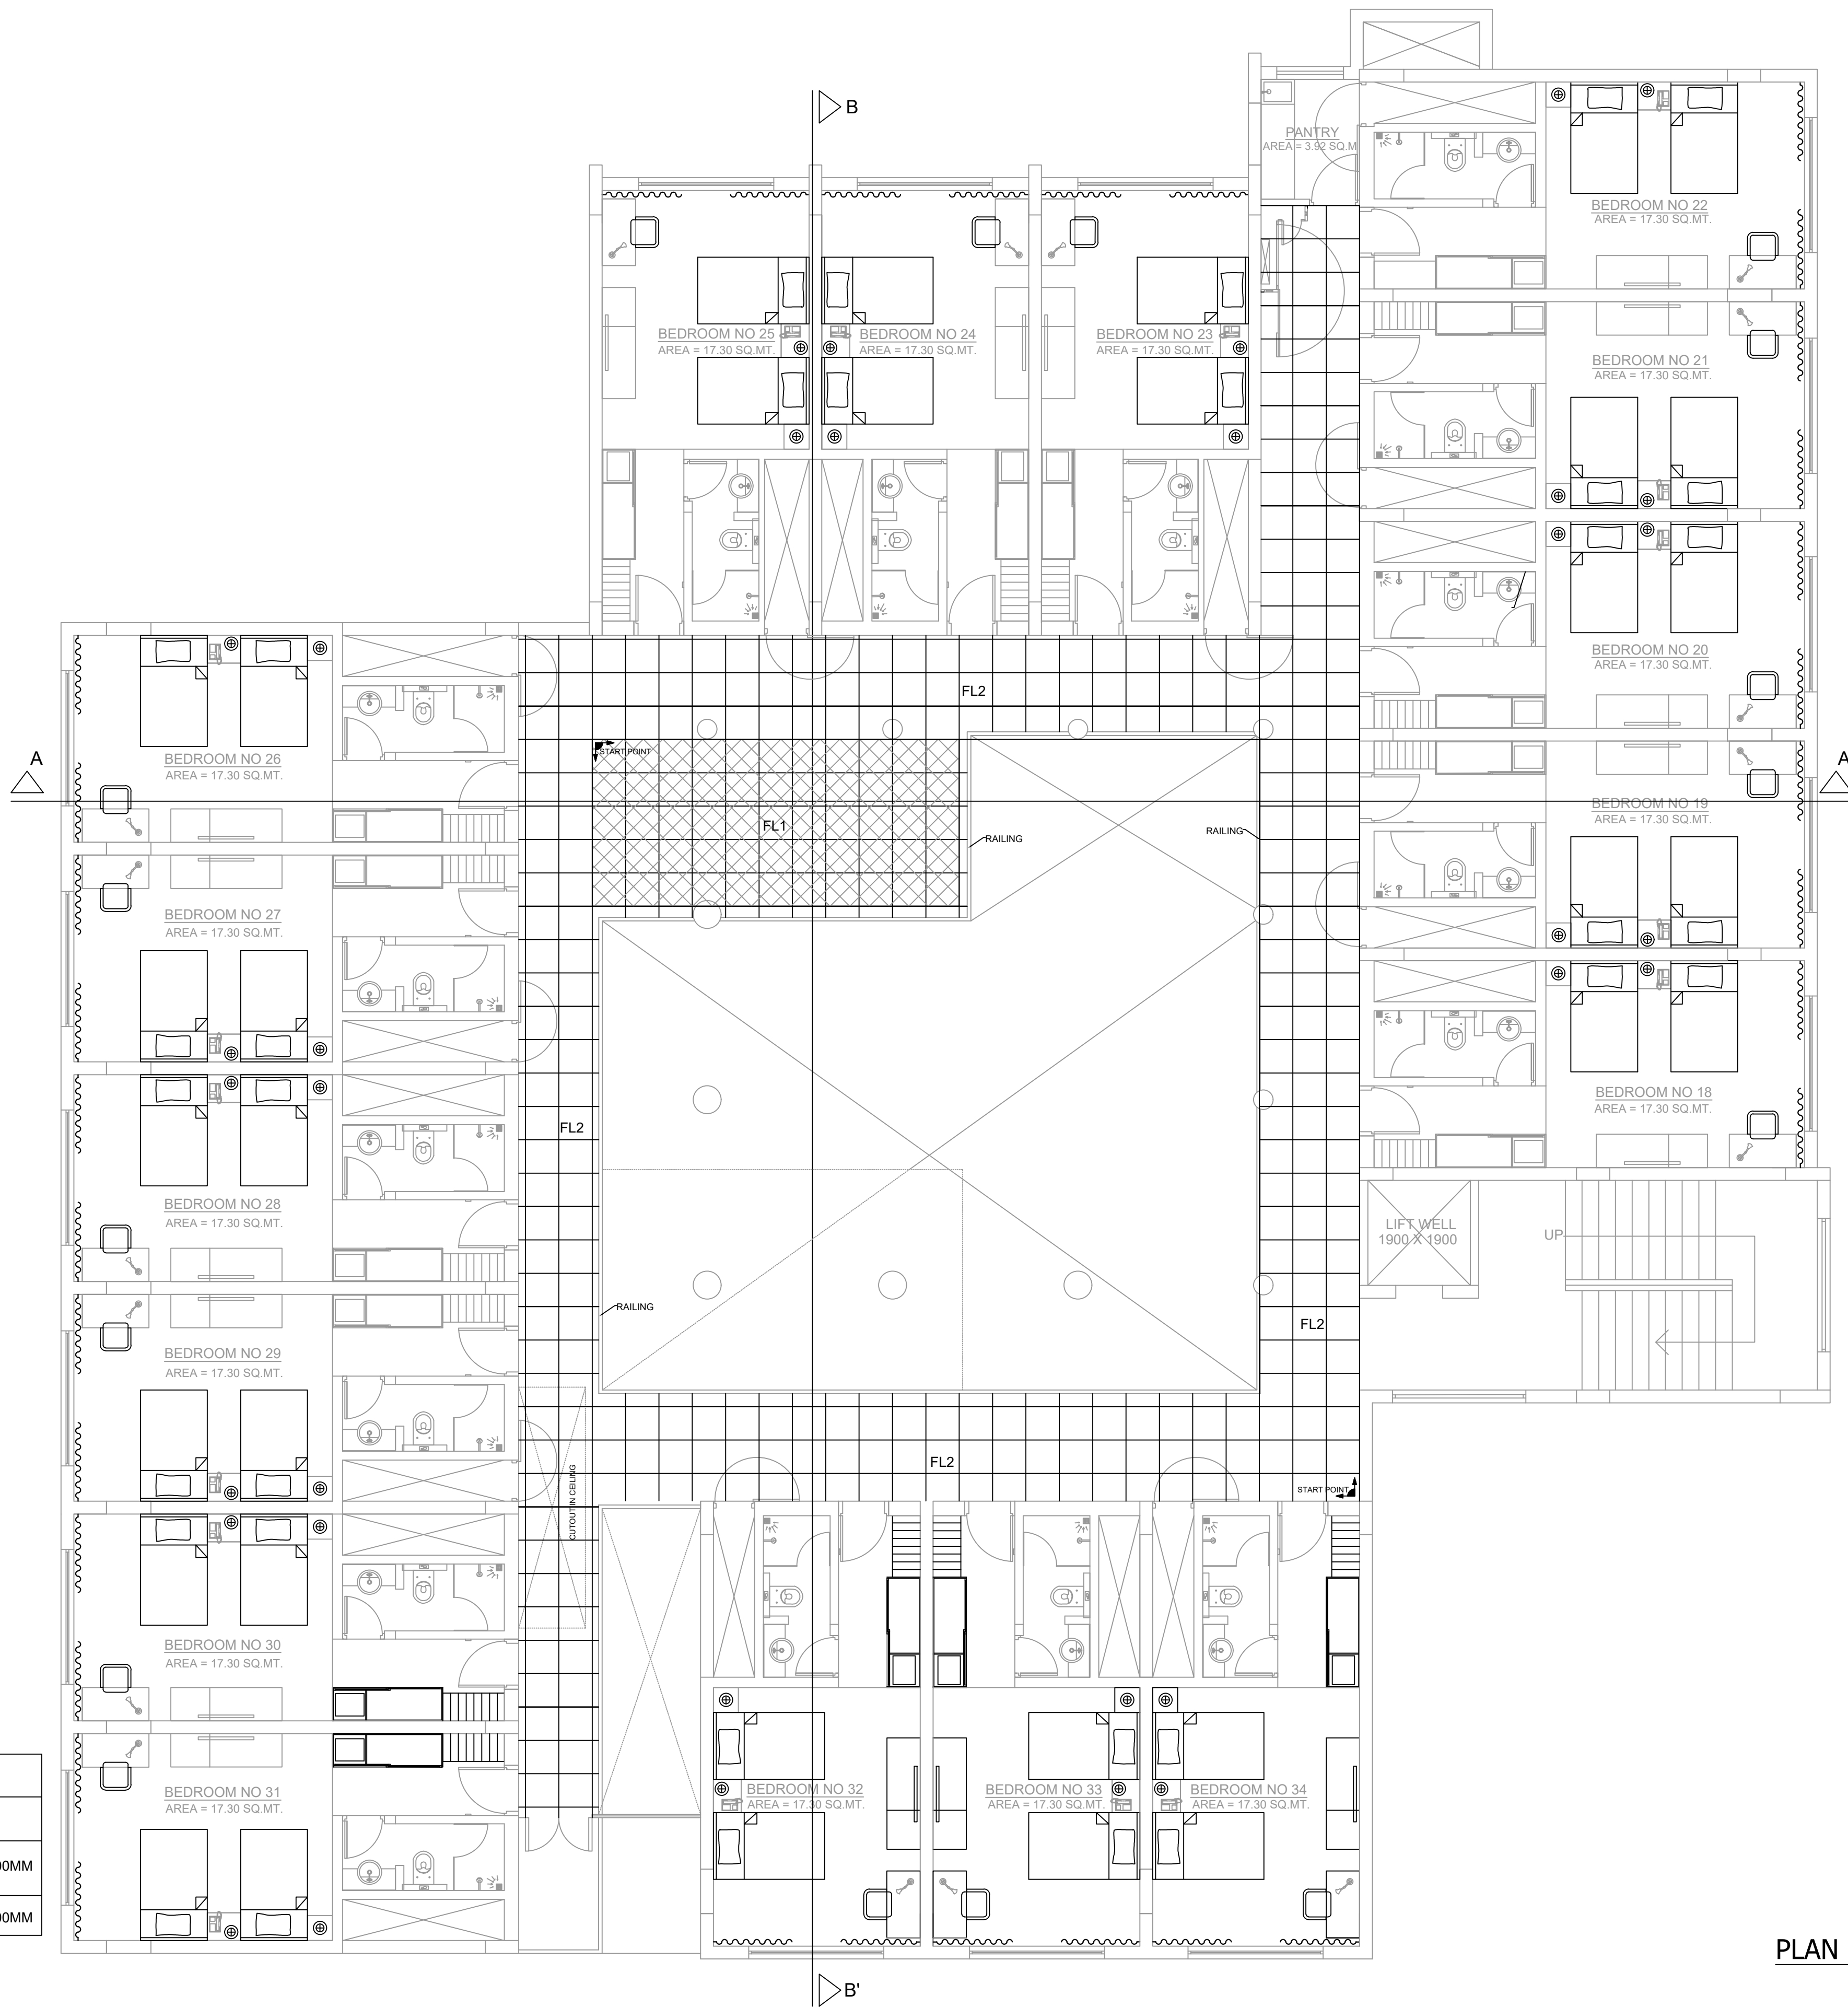

FLOORING DETAIL		
TYPE	ITEMS	SIZE
FL1	KAJARIA: TELAVERA GOLD - DECOR FINISH	600MMX600MM
FL2	KAJARIA: ETERNITY CAIRO COTTO	600MMX600MM

PLAN OF VANVIHAR 2nd FLOOR CORRIDOR FLOORING
SCALE -1:100

- NOTES:
- DRAWINGS SHALL NOT BE SCALED.
 - ALL DIMENSIONS ARE IN MM.
 - ANY DISCREPANCY IN DRAWINGS AND EXISTING CONDITIONS SHOULD BE BROUGHT TO THE NOTICE OF THE ARCHITECT PRIOR TO PROCEEDING WITH THE ITEM.
 - FOR SIZE OF STRUCTURAL MEMBERS REFER STRUCTURAL ENGINEER'S DRAWINGS.
 - ALL DOOR & WINDOW DIMENSIONS LISTED IN SCHEDULES MUST BE VERIFIED WITH SITE CONDITIONS BEFORE FABRICATION.
 - ALL DOOR AND WINDOW DIMENSIONS ARE MASONARY DIMENSIONS.
 - CORRELATE STRUCTURAL & ARCHITECT'S DWGS. AND GET BACK TO ARCHITECT WITH DISCREPANCIES IF ANY.

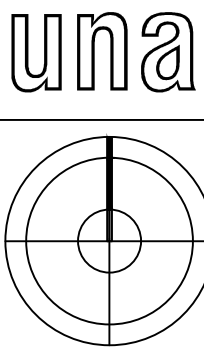

1	12.08.22	ISSUE FOR TENDER PURPOSE
No.	DATE	ISSUE/ REVISION
IIT BOMBAY: VANVIHAR GUEST HOUSE		
POWAI, MUMBAI-400 076, INDIA		
UPENDRA NAYAK & ASSOCIATES		
ARCHITECTS, INTERIOR DESIGNERS		
1, SULOCHA NIWAS, DILIP GUPTA MARG, MAHIM, MUMBAI-400016		
TEL: 24458473 FAX: 2446223		
DATE: 21.02.2022	SCALE: AS NOTED	DRAWN BY: HR
		CHECKED BY: AB

A18b